נספח

מרץ-גרה 01
10-07-2013
עותק זה בוצע בתאריך

20

חוק התכנון והבניה התשכ"ה-1965
בקשה להיתר בניה או לשימוש במקרקעין

טופס 1
תקנה 2(א)

חוק התכנון והבניה, התשכ"ה-1965
תקנות התכנון והבניה (בקשה להיתר
תנאיו ואגרות), התשל"-1970

לרשיון

ועדה מקומית לתכנון ובניה רשות רישוי	מס בקשה:	מס תיק:
הרצליה	21030304	5848

תאור הנכס

שם הישוב:	שם הרחוב:	מס בית	גוש	חלקה	מגרש	התכנית/יות החלה/ות במקום
הרצליה	השושנים	4	6529	167		
סמל ישוב	סמל רחוב					

מיפרט

	השם	מס זהות או רישומו של תאגיד	המען: רחוב	מס בית	ישוב+מיקוד	מס	טלפון / פקסימיליה
המבקש	כהן מרדכי	301644	השושנים	4	הרצליה	ט.	0547688250
בעל הזכות בנכס (בעלות ☐ חכירה ☐ אחר ☐)	לפי רשימתבטלי דירות מצורפת לטיל					ט. פ.	
עורך הבקשה הראשי	יוסף סיון, אדריכל	001436112	בארי	36	תל אביב, 64233	ט. פ.	050-2547164 03-6960757
מתכנן שלד הבנין	יבגני ז'יטומירסקי	30429638	כחנור	10,	ראש העין	ט. פ.	03-9211699

תאור הבקשה: תוספות ושינויים לבית מגורים משותף בן שלש קומות טל עמודים, 6 יח' דיור:
1. תוספת מטלית פנימית+הריסת מדרגות ובנית מדרגות חדשות
2. הגדלת לובי כניסה
3. אישור מיוחד של מהנדס הוטדה ומכבי אש לרחב מדרגות 80 ס"מ
4. אישור מיוחד של מהנדס הוטדה לרוחב פרוזדור מול דלת המטלית90 ס".

שימוש עיקרי: ☒ מגורים ☐ מסחרי ☐ בידור ☐ תעשיה ☐ מלאכה ☐ חקלאי ☐ משרדים ☐ מלונאות ☐ נופש וספורט ☐ בניני ציבור ☐ שמוש אחר ______

סוג העבודה או השימוש המוצעים: ☐ בנין חדש ☐ תוספת לבנין ☒ שינוי בבנין ☐ תיקונים ☐ הריסה ______ ☐ שינוי בשימוש ממטרה ______ למטרה ______

האם הבניה היא עבור: ☒ גורם פרטי ☐ משרד ממשלתי ☐ רשות מקומית ☐ מוסד ציבורי ☐ בנה ביתך ☐ אחרת ______

שטח: המגרש/החלקה: 1232 מ"ר. שטח הבניה הכולל המבוקש: מ"ר ______ % בניה ______

חומרי הבניה

סוג הבניה: ☐ רגילה ☐ מתועשת ☐ להרכבה ☐ בית מוכן ☐ אחר ______

קירות חיצוניים: ☒ בטון מזויין ☐ בלוקים ☐ אבן טבעית ☐ לבנים שרופות ☐ חומר אחר ______

חומר גימור: ☐ אבן מלאכותית ☐ אבן טבעית ☐ טיח ☐ זכוכית ☒ חומר אחר גבס

תקרות: ☐ בטון מזויין ☐ עץ ☐ חומר אחר ______

גג: ☒ בטון מזויין ☐ רעפים ☐ אסבסט ☐ טיח ☐ חומר אחר ______

גדרות: ☐ אבן טבעית ☐ אבן מלאכותית ☐ בטון ☐ בלוקים ☐ ברזל ☐ עץ ☐ רשת ☐ חומר אחר ______
קיימות ______ מ"א מוצעת ______ מ"א סה"כ ______ מ"א

פרטי הבנין - לשימוש הלשכה המרכזית לסטטיסטיקה

היעוד	שטח הבניה ברוטו - לפי יעוד: פירוט היעוד (כגון דירות למגורים, בית מלון וכו.)	השטח בהתאם להיתר	גודל הדירות לפי מספר חדרים: דירות בנות	מספר דירות	מספר מגורים
למגורים					
להארחה					
לעסקים ומשרדים					
לבניני ציבור					
לתעשיה ולמלאכה					
למשק חקלאי					
מקלט או מרתף					
מבני עזר					
סה"כ שטח הבניה					

מס. היתר הבניה: תאריך	חודש	שנה
היתר בניה		
התחלת הבניה		
גמר הבניה		
מספר הקומות (קומת עמודים מפולשת)		

-- 1 --

השטחים המבוקשים לבניה בכל מפלס בנפרד (עיפי תכנית הבניה)

הקומה והמפלס בבנין **	מקלט	מתקנים חדר מכונות	אחסנה	חניה	מבואות הרחבת לובי	קומת עמודים מפולשת	מעברים לכלל הציבור	בליטות	אחר	בנייה קיימת
קרקע		1.65			3.62			ת.ג.שפ' קיים 7.15	גוזל 2.60	
א'										
ב'										
ג'										
גג										
סה"כ										
מעל הקרקע										
מתחת הקרקע										

השימושים העיקריים (מ"ר) א — קוד / שימוש (קיים, מוצע); סה"כ שטח קיים; סה"כ מ"ר, % משטח המגרש. חלקי שירות (מ"ר) ב — סה"כ מ"ר, % משטח המגרש. סה"כ הבנין ג — מ"ר, %. משטחים לא מקורים.

* יש לרשום קוד ושם השימוש המבוקש בכותרת הדף.
** פירוט נוסף נמצא בדפי ההסבר

הערות: 1. במידה שקיימים יותר משלושה שימושים יש להשתמש בטופס נוסף.
2. במידה ואין מספיק שורות למספר קומות או מפלסים יש להשתמש בטופס נוסף.

הערה
סה"כ השטחים המבוקשים א+ב = ג
חייבים להיות שווים לשטחים המותרים א1 + ב1 = ג1

השטחים המותרים לבניה בכל המפלסים יחד (עיפי אסמכתא: חוק, תקנות, תכנית)

אסמכתא	מקלט	מתקנים ומערכות טכניות	אחסנה	חניה	מבואות וחדרי מדרגות	קומת עמודים מפולשת	מעברים לכלל הציבור	בליטות	אחר (פטיו)	בנייה קיימת מרתף קיים
תכנית ראשית										
מעל הקרקע										
מתחת הקרקע										

השימושים העיקריים (מ"ר): קוד, קוד, קוד; סה"כ מ"ר, % משטח המגרש. חלקי שירות (מ"ר): סה"כ מ"ר, % משטח המגרש. סה"כ השטחים המותרים לבניה: מ"ר, %.

הנני מצהיר על נכונות הפרטים דלעיל:
15.5.13 — יוסף סיון, אדריכל
תאריך — שם וחתימת עורך הבקשה הראשי

יוסף סיון
אדריכל ומתכנן ערים
בארי 36, תל אביב 64233
050-2547164,0508963003. פקס

חתימות נוספות:

	תאריך	שם	חתימה
המבקש	15.5.13	כהן מרדכי	
בעל הזכות בנכס			
מתכנן שלד הבנין	15.5.13	יבגני ז'יטומירסקי	ז'יטומירסקי יבגני מהנדס, מ.ר. 43494 טלפון:

במקרה של בקשה להקלה או לשימוש חורג יש לחתום גם על פירוט הבקשה להלן:

פירוט הבקשה להקלה / לשימוש חורג	נמוקי הבקשה

הנני מצהיר על נכונות הפרטים דלעיל:
______ תאריך ______ שם וחתימת עורך הבקשה הראשי

חותמת הועדה המקומית
רשות הרישוי:

הועדה המקומית לבניה ולתכנון ערים
הרצליה
רשיון מס' 20130304 תאריך 04.08.13
אושר ע"י הועדה המקומית
בישיבה מס' 417
בתאריך 05.06.13
מזכיר
הועדה המקומית לבניין ערים

נבדק מטעם הוועדה / רשות הרשוי ע"י:
שם ______ תאריך ______
תפקיד ______ חתימה ______

חותמות אחרות:

-- 2 --

א. מינויים והצהרת המבקש *
1(א). מינוי עורך הבקשה הראשי
אני ממנה בזה את ______ בעל/ת מס. זהוי ______ להיות עורך הבקשה הראשי להיתר. ולייצגני בפני מוסדות התכנון והרשויות המוסמכות בכל הנוגע לטיפול בבקשה להיתר וקבלתו. לרבות התיקונים ככל שידרשו על ידי הרשויות הניל.
1(ב). מינוי עורכי בקשה (לפי תחומים)
אני ממנה בזאת את:

שמות עורכי הבקשה	תחום פעולה	מען	טלפון	פקס.
1. יוסף סיון	אדריכל	בארי 36 תל אביב	0502547164	036960757
.2				
.3				
.4				
.5				
.6				
.7				
.8				
.9				
.10				

להיות עורך הבקשה להיתר בתחום הפעולה הניל. ולייצגני בתחום פעולתו בפני מוסדות התכנון והרשויות המוסמכות. בכל הנוגע לטיפול בבקשה להיתר ולקבלתו. לרבות התיקונים ככל שידרשו על ידי הרשויות הניל.

2. מינוי מתכנן השלד
אני ממנה בזה את יבגני ז'יטומירסקי בעל/ת מס. זהוי 30429638
כתובת כינור 10 ראש העין טל 03-9014047 פקס.
להיות מתכנן השלד של הבנין שעליו מבוקש ההיתר. להגיש לועדה המקומית/רשות הרישוי המקומית את החישובים הסטטיים לגבי הבניה שעליה מבוקש ההיתר. ולקיים פיקוח עליון על הקמת השלד.

3. מינוי הקבלן האחראי לביצוע הבנין
אני ממנה בזה את ירטל הנדסה בעל/ת מס. זהוי ח.פ. 513764748
ובעל תעודת רישום מס 14294 בפנקס הקבלנים במדור הנדסה בנאית
ובעל רשיון לביצוע העבודה בתוקף עד 31.12.14? לבצע את העבודה נשוא ההיתר כמתחייב לפי כל דין.
(אם טרם נתמנה קבלן לביצוע העבודה:)
אני מצהיר כי טרם מסרתי את ביצוע העבודה נשוא ההיתר לידי קבלן. ומתחייב כי אמסור אותה לידי קבלן רשום בפנקס הקבלנים. ככל המתחייב על פי כל דין. ולהודיע זאת לרשות הרישוי המקומית טרם התחלת ביצוע העבודה. וחתימתו של הקבלן תצורף להודעה המפרטת את פרטי רישומו של הקבלן.

4. מינוי האחראי לביצוע השלד
אני ממנה בזה את ירטל הנדסה בעל/ת מס. זהוי ח.פ. 513764748
כתובת ______ טלפון 03-9211699 פקס. 03-9211540
להיות האחראי/ת לביצוע שלד הבנין.
(אם טרם מונה האחראי לביצוע שלד הבנין:)
אני מצהיר כי טרם מיניתי אחראי/ת לביצוע עבודות הבניה בתחומים (לפרט:) החרושת 11 רמת השרון ומתחייב לעשות זאת כמפורט בתקנות. ולהודיע על כך לרשות הרישוי המקומית טרם התחלת ביצוע העבודה. תאריך ______ חתימת המבקש ______

5. מינוי אחראים לביקורת
אני ממנה את הרשומים להלן להיות אחראים לביקורת ביצוע עבודות הבניה. כל אחד בתחום המצויין ליד שמו:

שם האחראי לביקורת	תחום פעולה	מען	טלפון	פקס.
.1				
.2				
.3				
.4				
.5				
.6				
.7				
.8				
.9				
.10				

(אם טרם נתמנו אחראים לבקורת. כולם או חלקם:)
אני מצהיר כי טרם מיניתי אחראי/ים לביקורת ביצוע עבודות הבניה בתחומים (לפרט:) ______ ומתחייב לעשות זאת כמפורט בתקנות. ולהודיע על כך לרשות הרישוי המקומית טרם התחלת ביצוע העבודה. תאריך ______ חתימת המבקש ______

ב. הצהרות
1. הצהרת עורכי הבקשה
אנו החתומים מטה מצהירים בזה:
(1) כל אחד מאתנו מאשר שהאמור לגביו ברשימה שבפיסקא א.1(ב) למעלה הוא נכון.
(2) כל אחד מאתנו מסכים לקבל על עצמו את התפקיד המיועד לו בפיסקא הניל.
(3) אנו מצהירים. כל אחד לגבי תחום פעולתו. שיש לנו את הכישורים המקצועיים לערוך בקשה זו וכי בדקנו את המסמכים הנוגעים לבקשה. לרבות כל תכנית המתייחסת לבקשה. וידוע לנו כי אם הצהרה זו אינה נכונה. הרי היא תחשב כמסירת ידיעה שהיא כוזבת או מטעה בפרט חשוב. כמשמעותה בסעיף 214 לחוק והננו צפויים לעונשים הקבועים לפי כל דין.
אני ______ (עורך הבקשה הראשי) אחראי/ת לכך שהבקשה על נספחיה נערכה לפי מיטב הידיעה המקצועית ובהתאם לכל חיקוק החל על הבנין או העבודה המוצעת. שכל הנתונים שנמסרו על ידי בבקשה זו נכונים ושהתכנון המוצע תואם את כל התכניות. פרט לסטיות שפורטו לעיל.
תאריך ______

* נתמנה אדם אחד ליותר מתפקיד אחד. ימלא פרטיו וחתימתו ליד כל אחד מהתפקידים שהוא ממלא או מצהיר לגביהם. בכפוף להוראות כל דין.

שמות עורכי הבקשה	חתימת עורכי הבקשה	מס. רשיון
1. יוסף סיון	יוסף סיון אדריכל ומתכנן ערים בארי 36, תל אביב 64233 050-2547164,0508963003. פקס	05955
.2		
.3		
.4		
.5		
.6		
.7		
.8		
.9		
.10		

2. הצהרת מתכנן שלד הבנין
אני החים יבגני ז'יטומירסקי מס. זהוי 30429638
שם משפחה פרטי
מהנדס רישוי מס. 43494
הנדסאי בעל רשיון מס. ______ (לימבנה פשוט)
מצהיר בזאת כדלקמן:
(1 אני מסכים להיות מתכנן שלד הבנין נשוא הבקשה ולקיים פיקוח עליון על הקמת השלד.
(2 אני מתחייב להגיש לפני מתן ההיתר נשוא הבקשה את החישובים הסטטיים בדבר הבניה נשוא ההיתר.
(3 ידוע לי שאם אחרי הגשת החישובים הסטטיים יתגלה צורך בשינוי מהותי בהם אני מתחייב להגיש חישובים סטטיים מתוקנים מיד עם גילוי הצורך בכך.
(4 אני מצהיר כי יש לי הכישורים המקצועיים לערוך בקשה זו וכי בדקתי את כל המסמכים הנוגעים לבקשה לרבות כל תכנית המתייחסת לבקשה וידוע לי כי אם הצהרה זו אינה נכונה הרי היא תחשב כמסירת ידיעה שהיא כוזבת או מטעה בפרט חשוב כמשמעותה בסעיף 214 לחוק והנני צפוי לעונשים הקבועים לפי כל דין.
(5 ידוע לי כי עלי לשמור את תכניות הקונסטרוקציה בתקופה של לא פחות מ-10 שנים לאחר גמר הבניה.

ז'יטומירסקי יבגני מהנדס מ.ר. 43494 טלפון:

** 3. הצהרת האחראי לביצוע שלד הבנין (כאשר מונה)
אני החים יבגני ז'יטומירסקי מס. זהוי 30429638
מהנדס רשוי מס. 43494 (למבנה פשוט) הנדסאי בעל רשיון מס. ______ מצהיר בזה כדלקמן:
(1 אני מסכים להיות האחראי לביצוע שלד הבנין.
(2 יש לי את הכישורים המקצועיים להיות אחראי לביצוע שלד הבנין ואני מתחייב לדאוג לביצוע שלד הבנין על פי תכניות והוראות מתכנן השלד כפי שינתנו בכתב וכן לבצע תפקידי על פי שנקבע בכל חיקוק הנוגע לה.
תאריך ______ חתימה ______

ז'יטומירסקי יבגני

** 4. הצהרת האחראים לביקורת (כאשר מונו)
אנו החתומים מטה מצהירים בזה
(1 כל אחד מאיתנו מאשר שהאמור לגביו ברשימה שבפסקא א.(5) לעיל הוא נכון.
(2 כל אחד מאיתנו מסכים לקבל על עצמו את התפקיד המיועד לו בפיסקא הניל.
(3 אנו מצהירים כל אחד לגבי תחום פעולתו שיש לנו את הכישורים המקצועיים לערוך את הביקורת כהלכה ולדווח על תוצאותיה לרשות הרשוי המקומית כמתחייב על פי כל דין.
אני יבגני ז'יטומירסקי (עורך הבקורת הראשי) אחראי/ת לכך שהבקורת תערך על פי מיטב הידיעה המקצועית ושכל הדווחים לרשות הרשוי המקומית יערכו על פי כל דין.

שמות האחראים לבקורת	חתימת אחראים לבקורת	מס. רשיון
1. יבגני ז'יטומירסקי	ז'יטומירסקי יבגני מהנדס, מ.ר. 43494 טלפון:	43494
.2		
.3		5955
.4		
.5		
.6		
.7		
.8		
.9		
.10		

** ניתן להגשה בנפרד לפני התחלת הבניה.

-- 3 --

טבלת חתימות בעלי הנכסים
גוש 6529 חלקה 167

שם	מס זיהוי	מס' תת חלקה	חתימה
ניר שרי	6970756	1	
ניר יעקב	143871	1	
אברהם דרנוב	**0304582**	2	
דרנוב בילה	**787527**	2	
ליפשיץ שלמה	02237744	3	
כהן רחל מריאנה	216620/ד	4	
כהן מרדכי	301644	4	
דוכנה חנה	**6952162**	5	
שקבסקי ילנה	306680455	6	
שקבסקי אלכסנדר	306 680281	6	

הוראות לסידורי כבאות- היתר בנייה למעלית בבנין קיים

1 התקנת גלגלוני כיבוי באורך 25 מ בקומת הכניסה ובקומה העליונה, כאשר
2 אספקת המים לגלגלוני הכיבוי תהיה לפחות 45 ל/ד

התקנת מטפי כיבוי 6 ק"ג בכל קומה ובחדר מכונות המעלית

3 ארונות חשמל – תקשורת:
א- ארונות עץיוחלפו לארונות מתכת על פי תקנות החשמל
ב- במקרים בהם לא ניתן להתקין ארונות חשמל ממתכת על פי תקנות החשמל מסיבות שונות (לדוגמא: כאשר גב הארון בנוי בקיר רביץ ועליו לוחות עץ) ניתן לבצע כמפורט:
 1 התקנת גבס חסין אש שיכסה את כל גב הארון העשוי אש
 2 יש לאטום את כל שטח הארון לרבות החריצים וכניסת חוטי החשצל בחומר איטום מעכב בעירה
 3 מסגרת הארון והדלתות יהיו ממתכת כפי שנדרש בלוח החשמל לפי תקנות החשמל

4 בחדר המדרגות –
בחלקו העליון של קיר חדר המדרגות יש להתקין פתח קבוע לשחרור חום ועשן הפתוח לאויר החיצון שגודלו לא יפחת מ 1.6 מ"ר או שני פתחים דשגודל כל פתח לא יפחת מ 0.8 מ"ר
5 התקנת תאורת חרום על פי תקן ישראלי 20 בכל קומה וחדר מכונות המעלית
6 בחדר המכונות של המעלית הנמצא על גג המבנה יש להתקין בקיר חיצון חלון אוורור בחלקו העליון שלא יפחת מ 1 מ"ר בנוסף לדלת וכאשר חדר המכונות של המעלית נמצא בתוך המבנה יש להתקין פתח שיוביל לחלל החיצון
7 המעלית תעמוד בדרישות התקן הישראלי 24
8 חדר הגז יהיה בהתאם לתקן ישראלי 158
9 התכנון, הפיקוח והביצוע באחריות נורך הבקשה והיזם

בגמר הבניה יש להגיש את אישורים הבאים:
א- מעבדה מוסמכת ת"י 24
ב- חשמלאי בודק מערכת חשמל
ג- מעבדה מוסמכת ת"י 158
ד- ציוד כיבוי אש הרשום לעיל

מקרא מרכיבי כיבוי אש

120 דק'	אלמנט בעל עמידות אש 120 דקות
▤	גלגלון כיבוי אש "3/4 מתאים לת"י 2206
⊗	מטפה כיבוי ידני עם אבקה יבשה 6 ק"ג
◎	איזור עם גופי תאורת חרום
⊡	מפסק חשמל ראשי
✳	מתז (ספרינקלר)

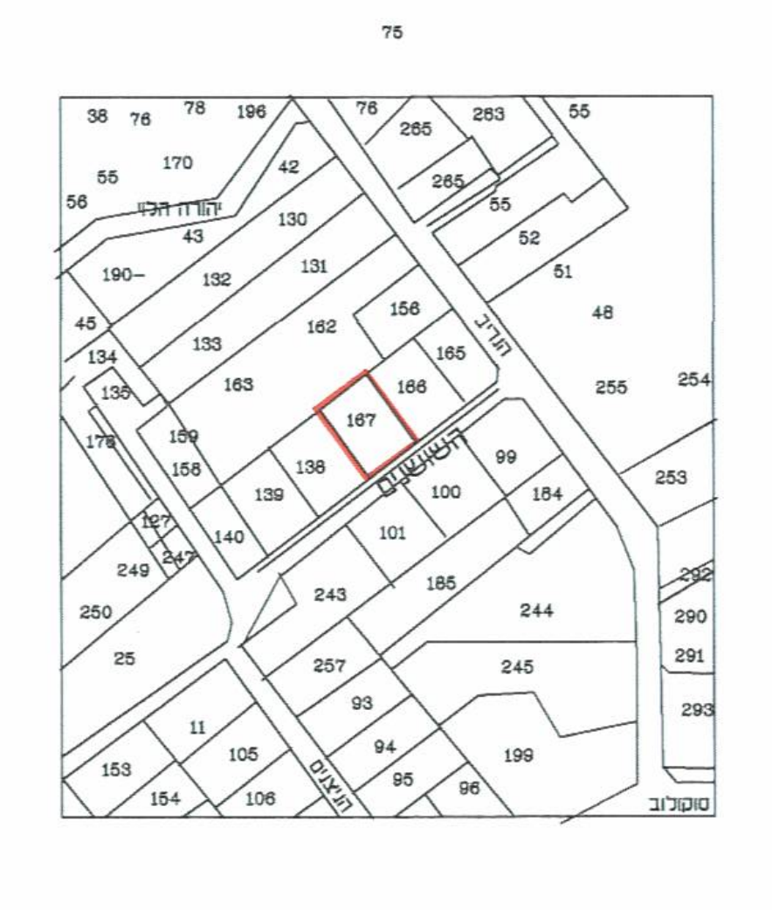

תרשים הסביבה

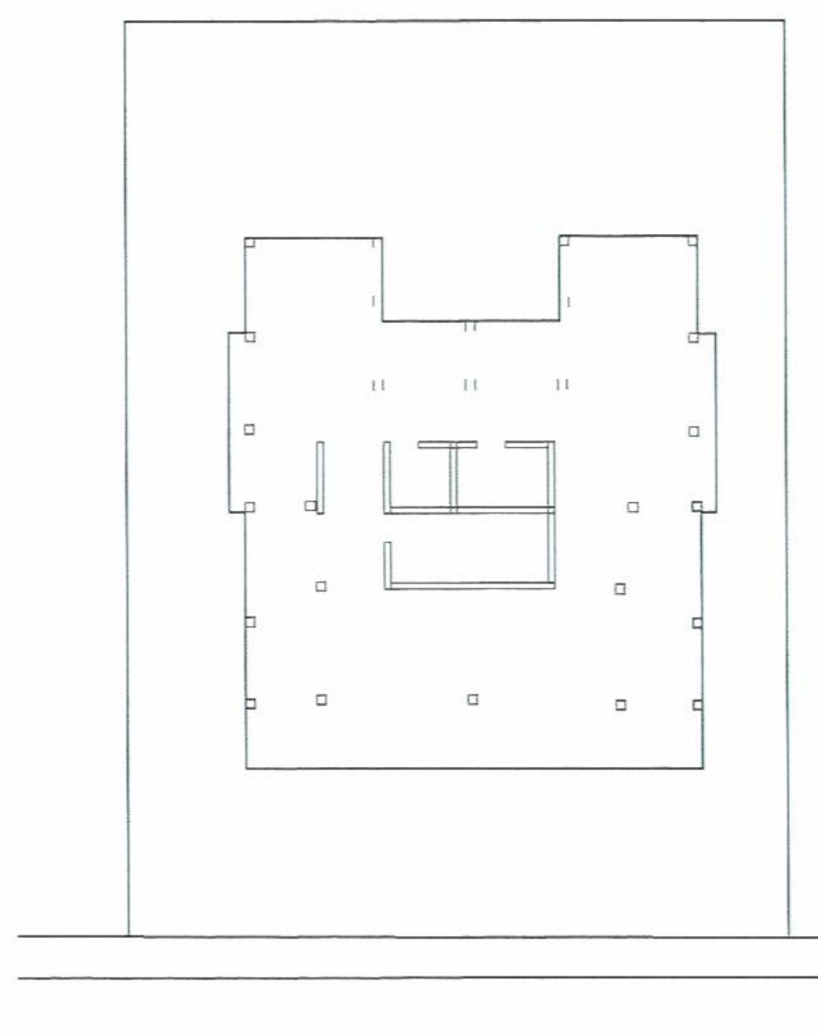

תרשים המגרש 1:250

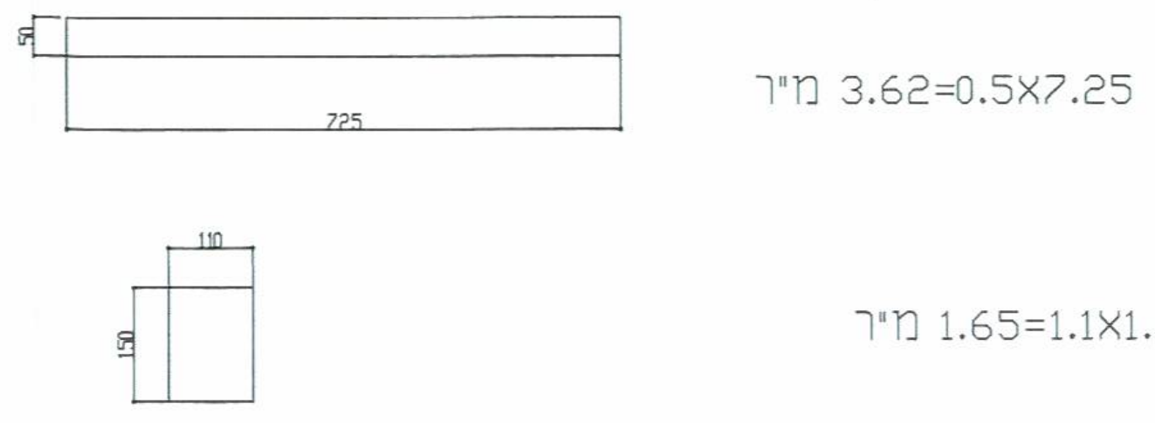

חשוב הרחבת לובי 3.62=0.5X7.25 מ"ר

חשוב חדר מכונות 1.65=1.1X1.5 מ"ר

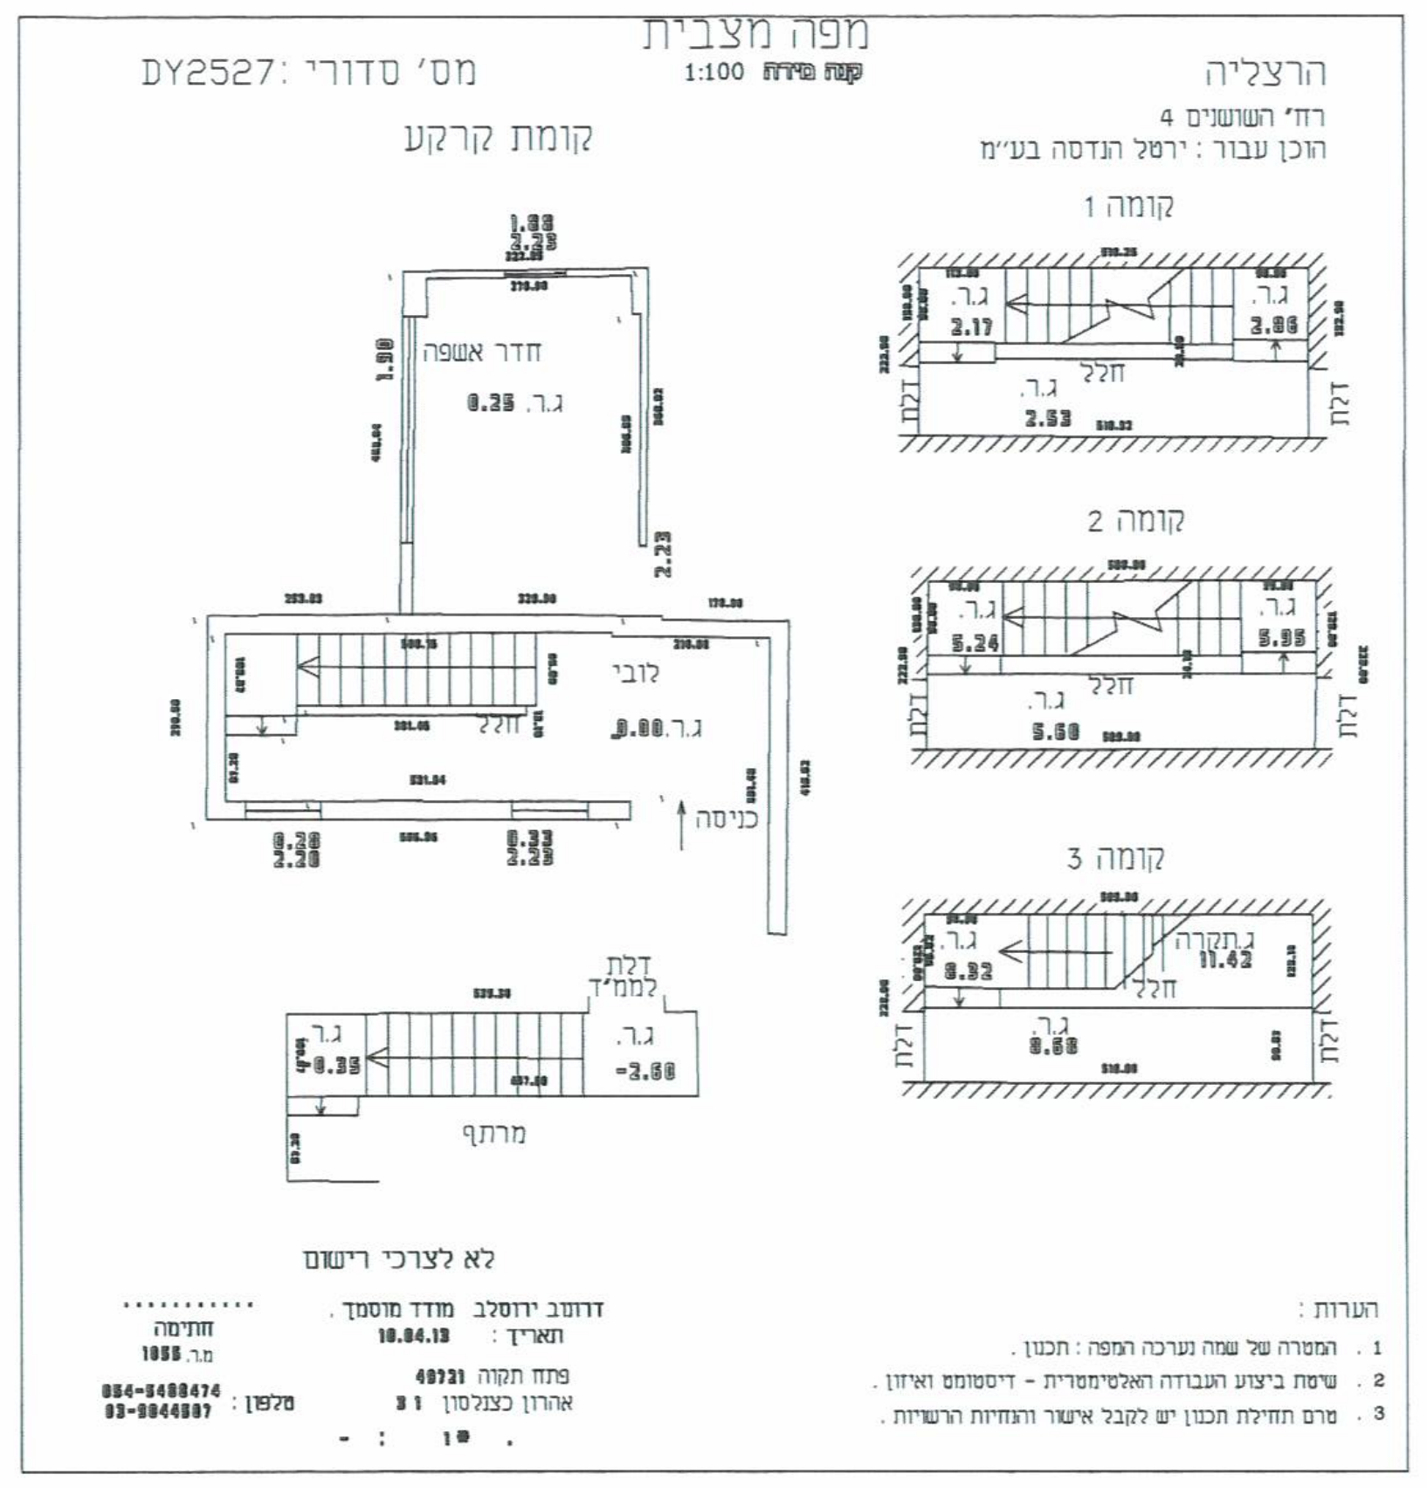

מפה מצבית
1:100 קנה מידה

הרצליה
רח' השושנים 4
הוכן עבור : ירטל הנדסה בע"מ

מס' סדורי: DY2527

לא לצרכי רישום

דרובב ירוסלב מודד מוסמך .
תאריך : 10.04.13
פתח תקוה 49721
אהרון כצנלסון 31
חתימה
מ.ר. 1055
טלפון : 054-5488474
03-9044597

הערות :
1 . המטרה של שמה נערכה המפה : תכנון .
2 . שיטת ביצוע העבודה האלטימטרית - דיסטומט ואיזון .
3 . טרם תחילת תכנון יש לקבל אישור והנחיות הרשויות .

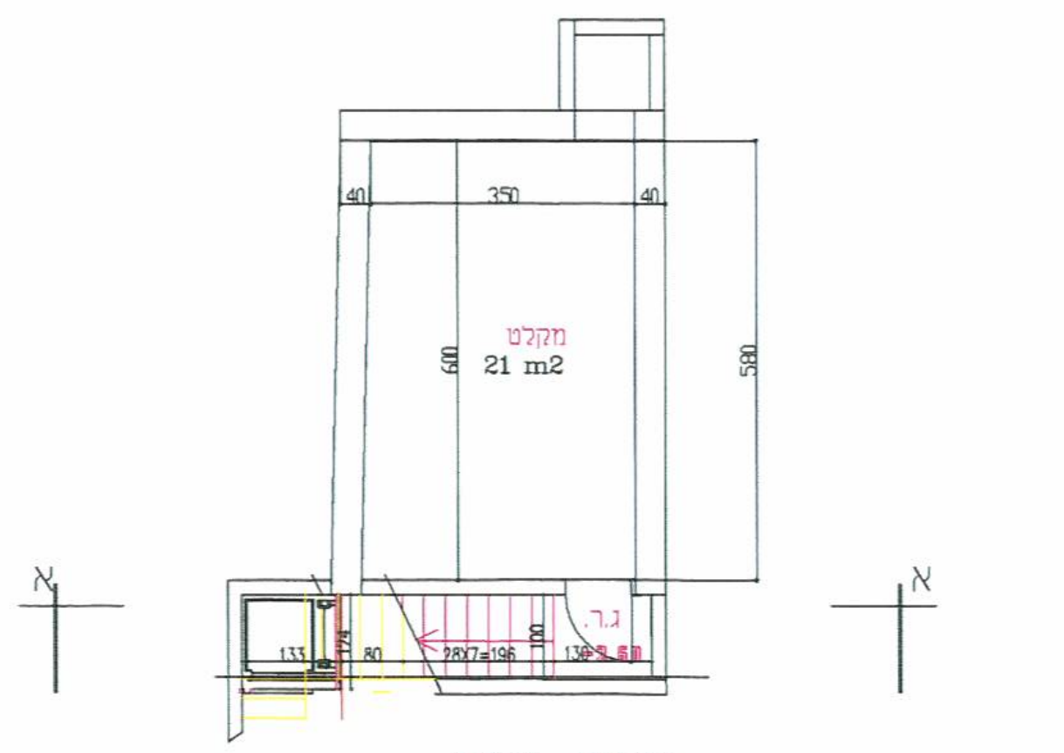

מרתף 1:100

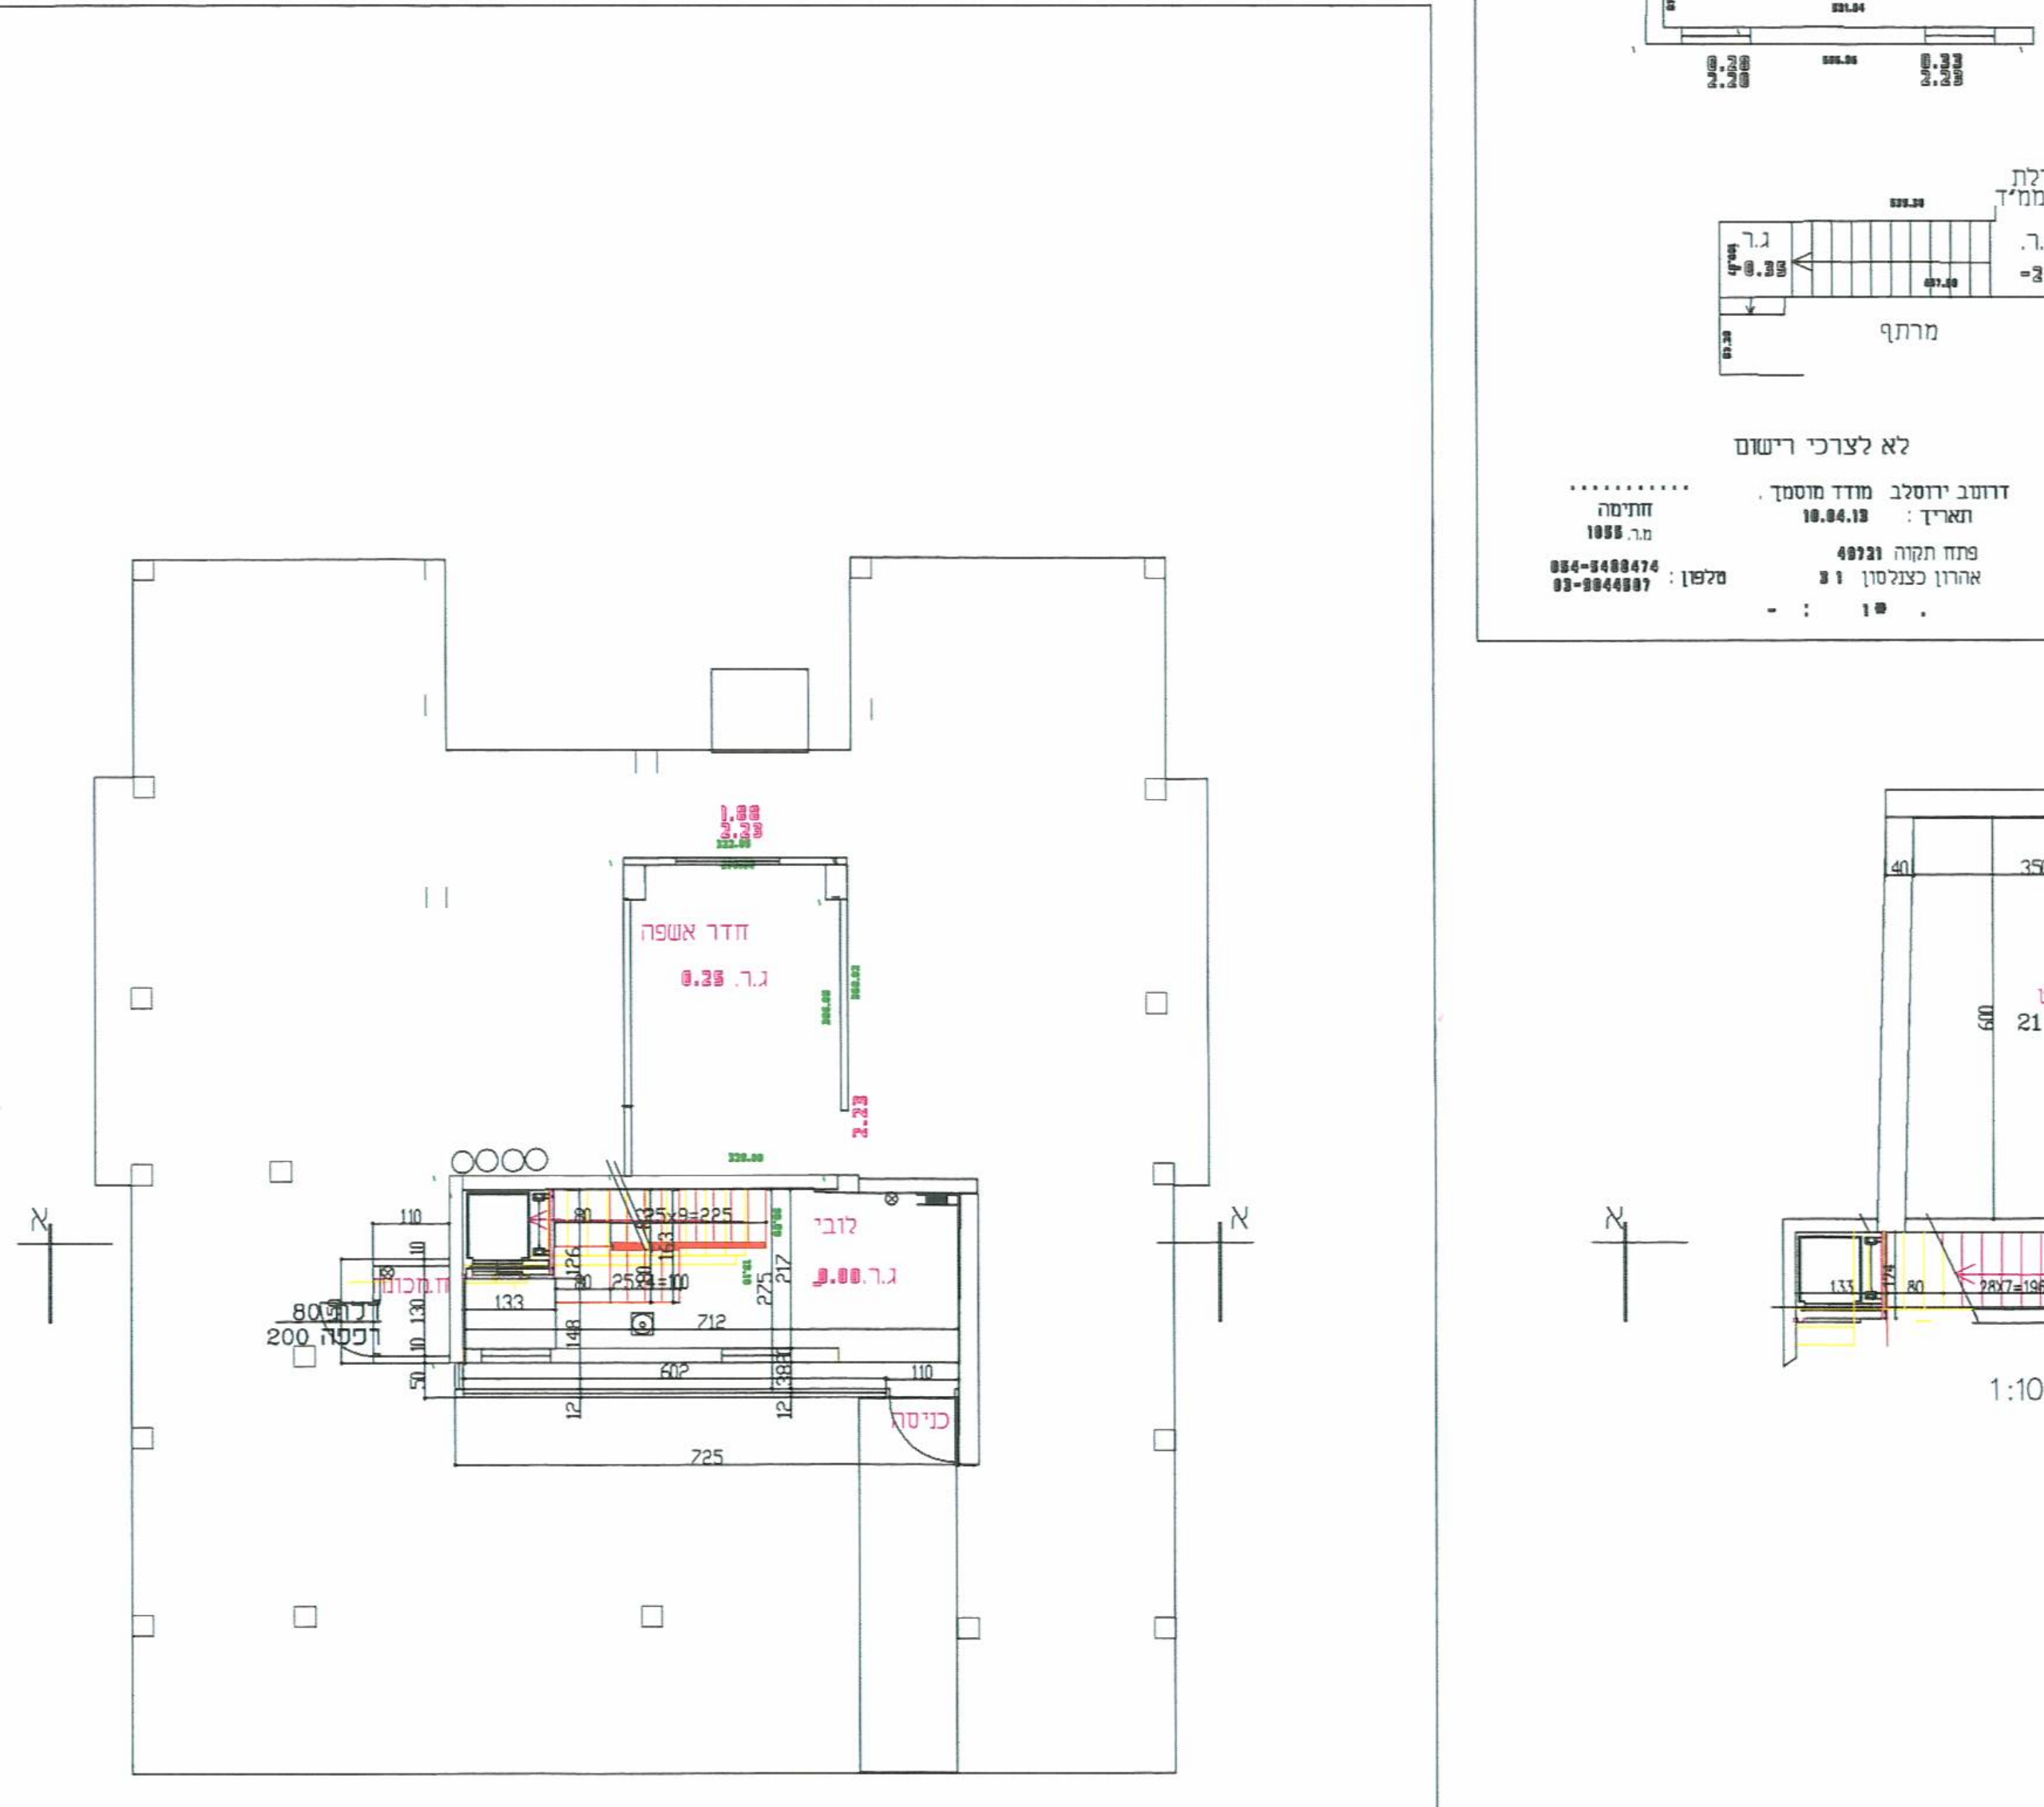

רח' השושנים
קומת קרקע 1:100

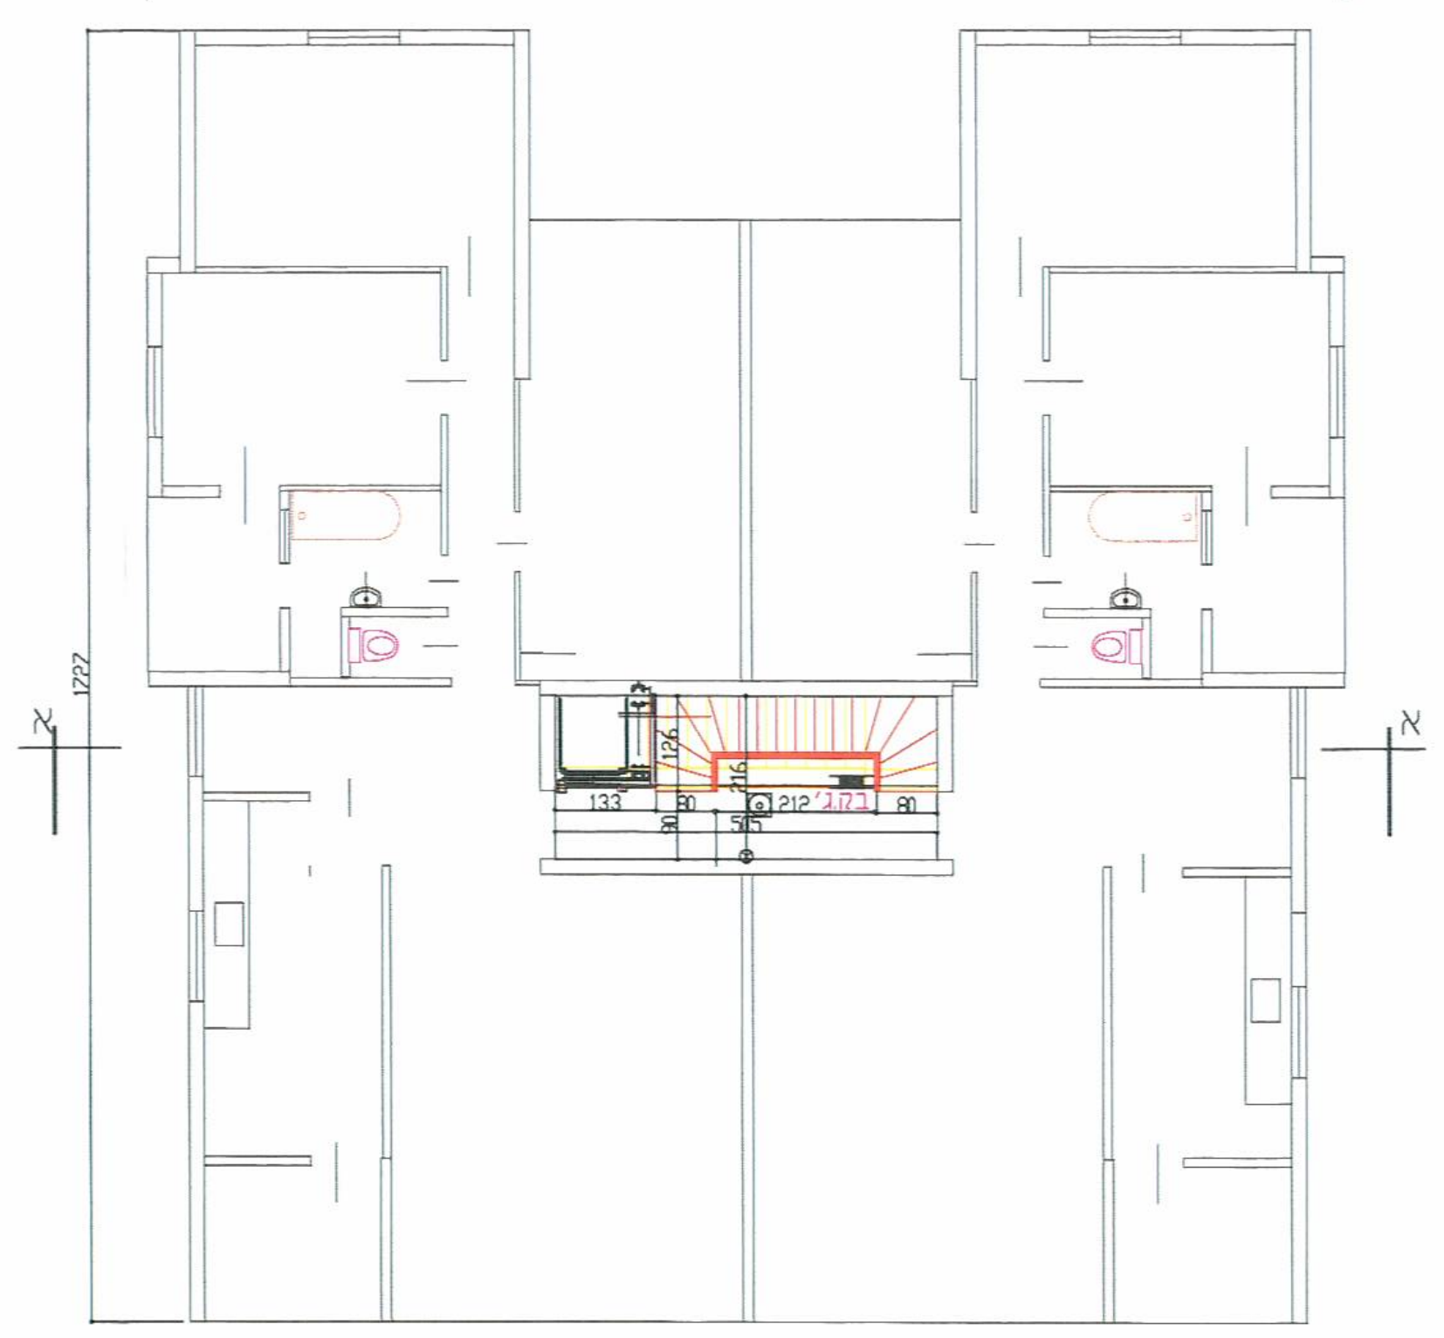

קומה טיפוסית 1:100

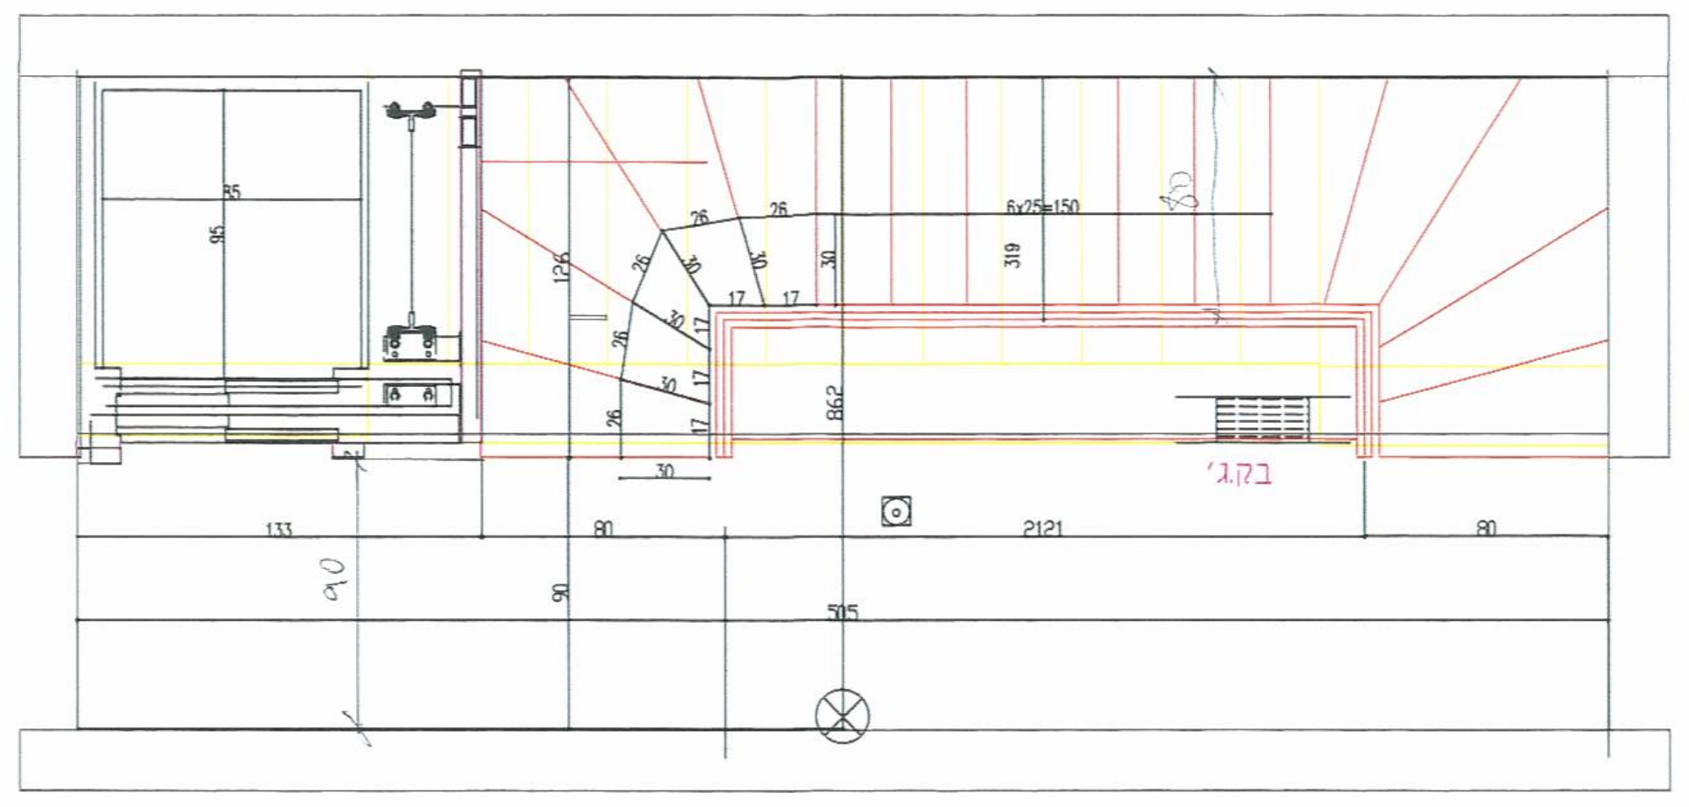

קומה טיפוסית 1:25

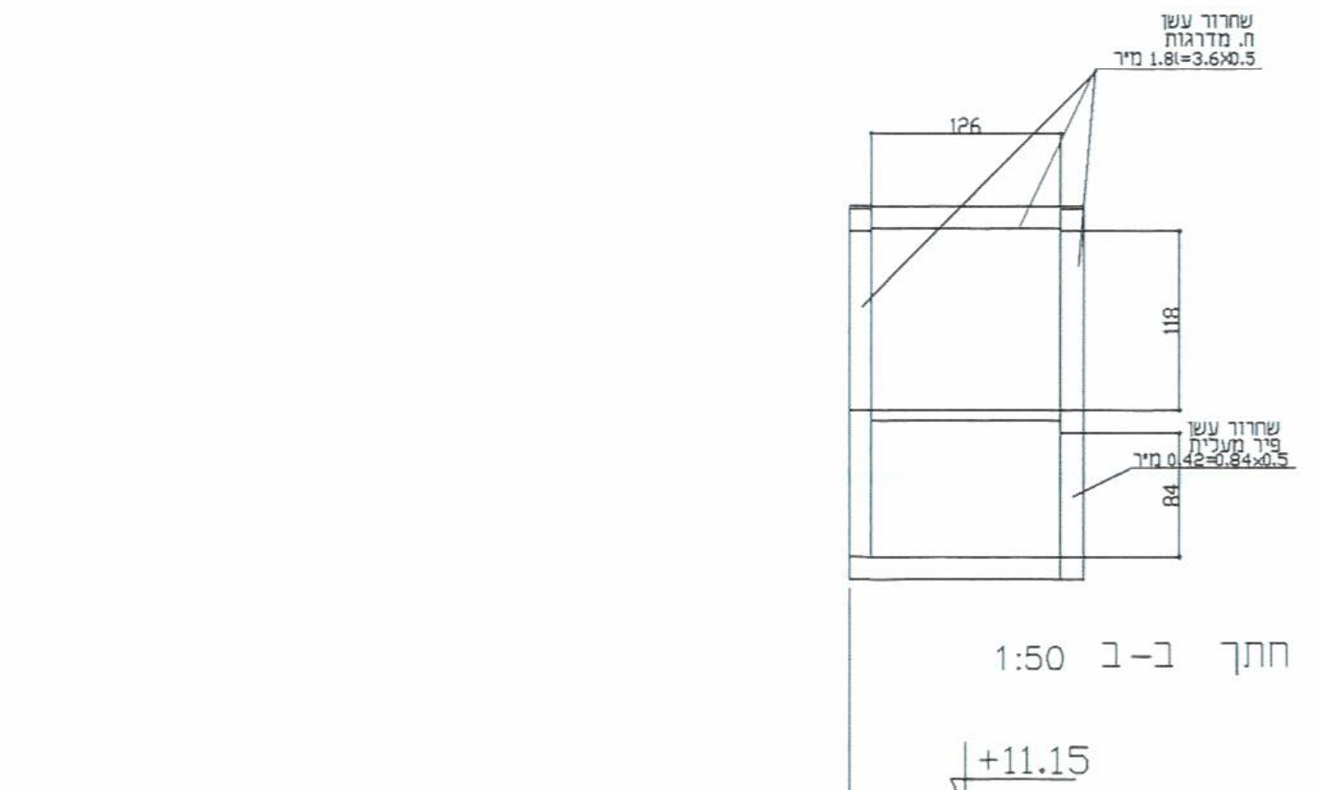

חתך ב-ב 1:50

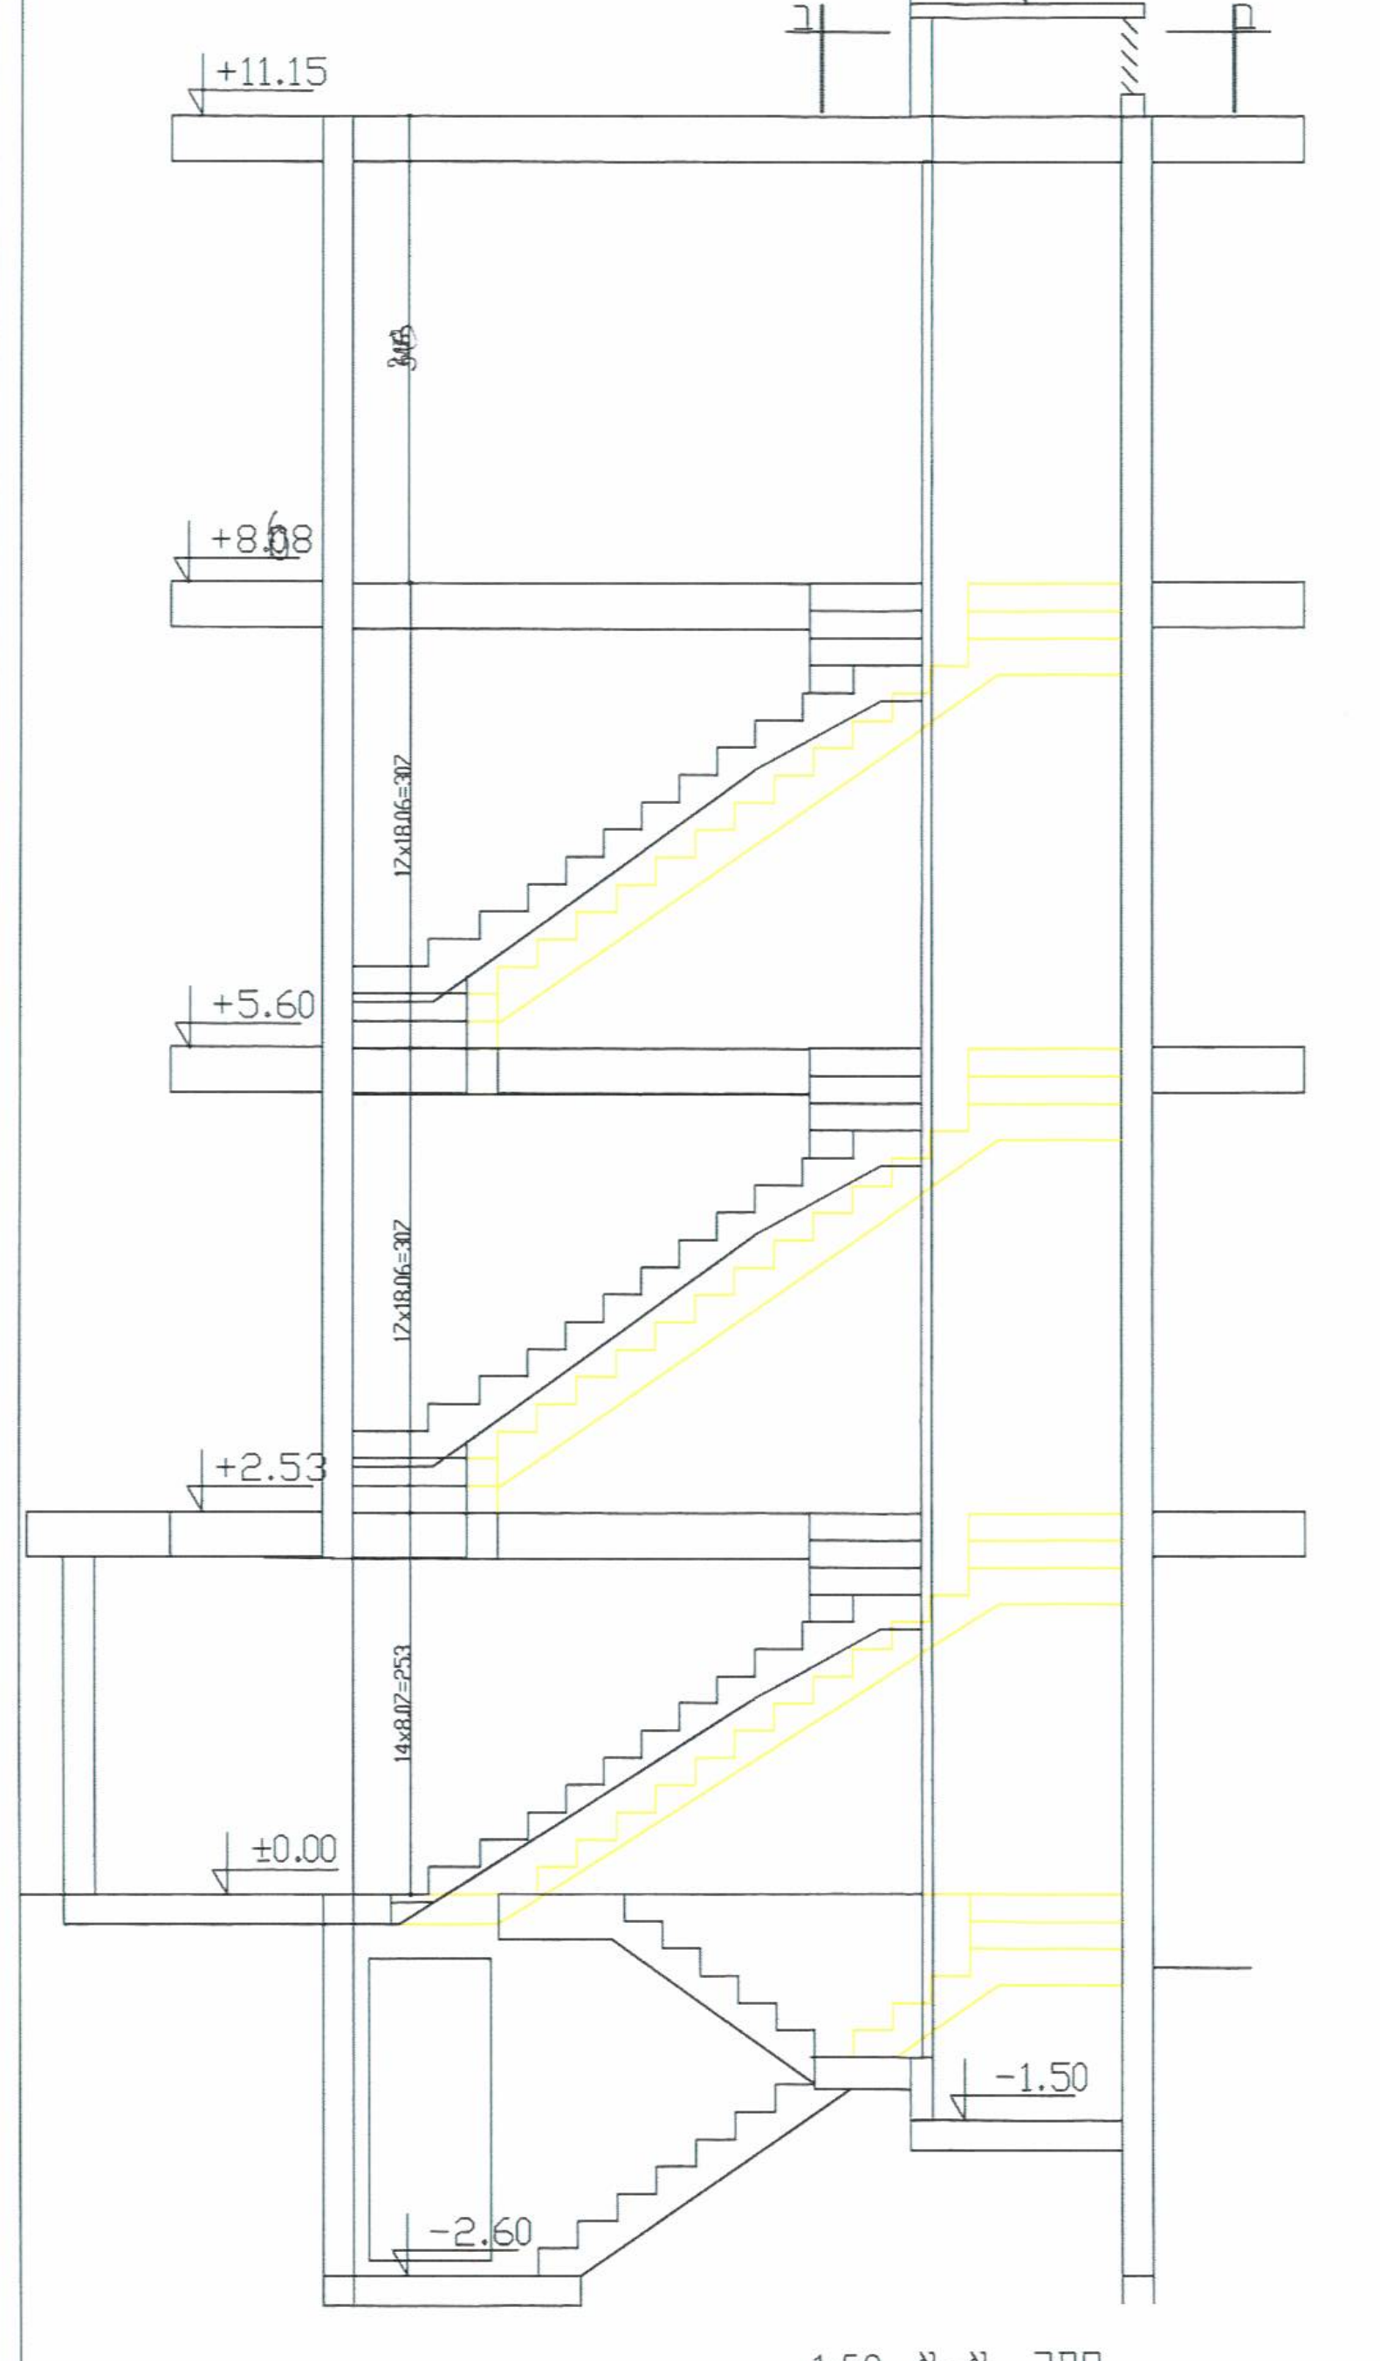

חתך א-א 1:50

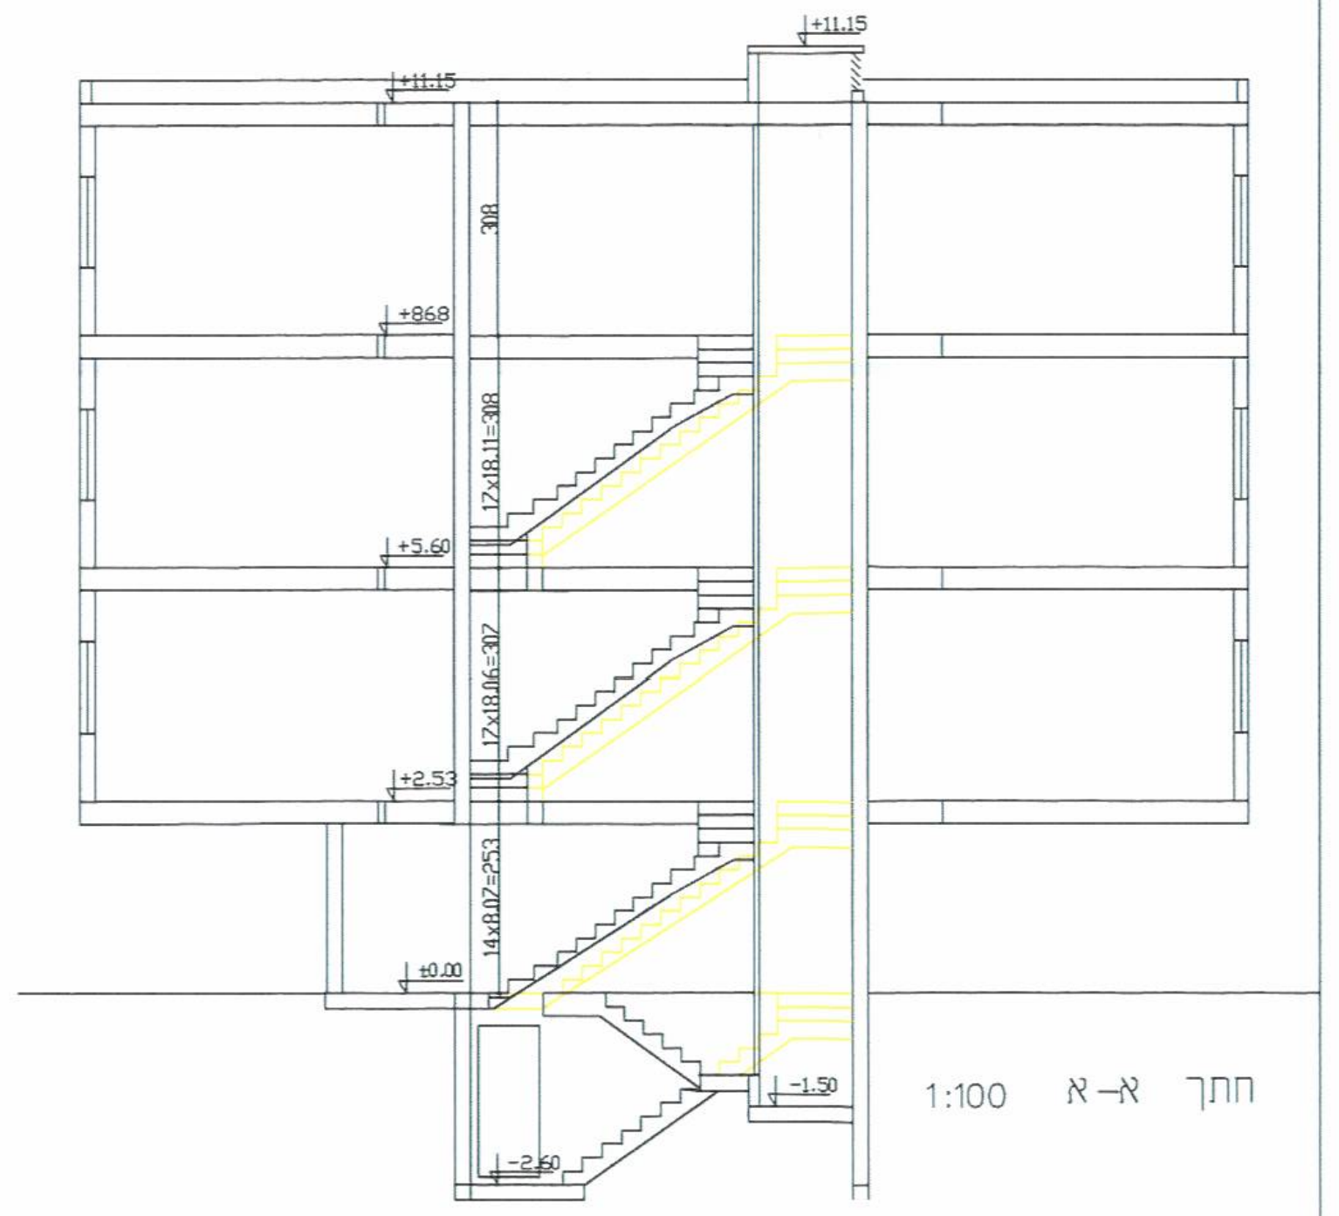

חתך א-א 1:100

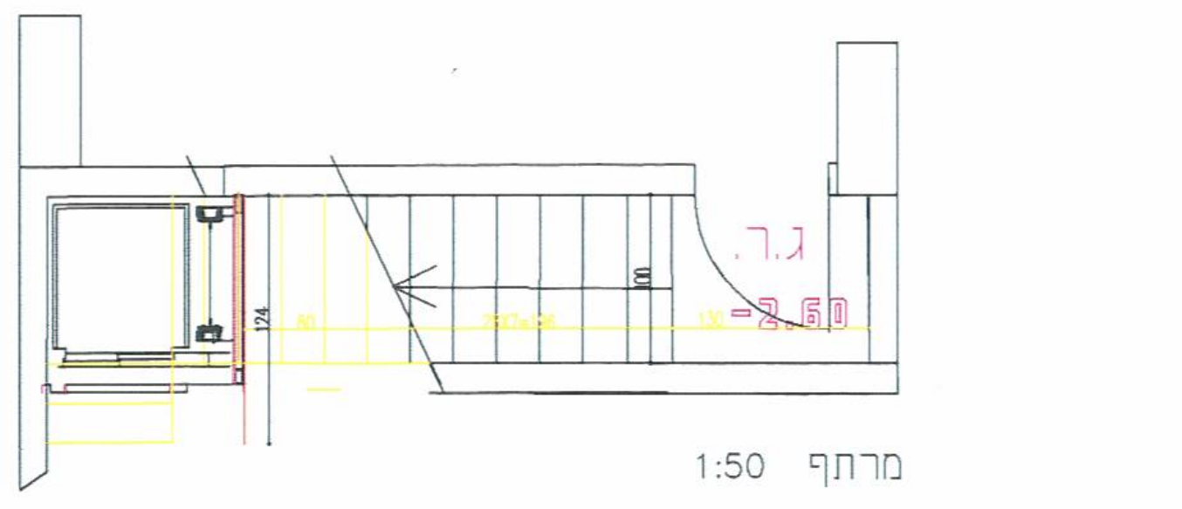

מרתף 1:50

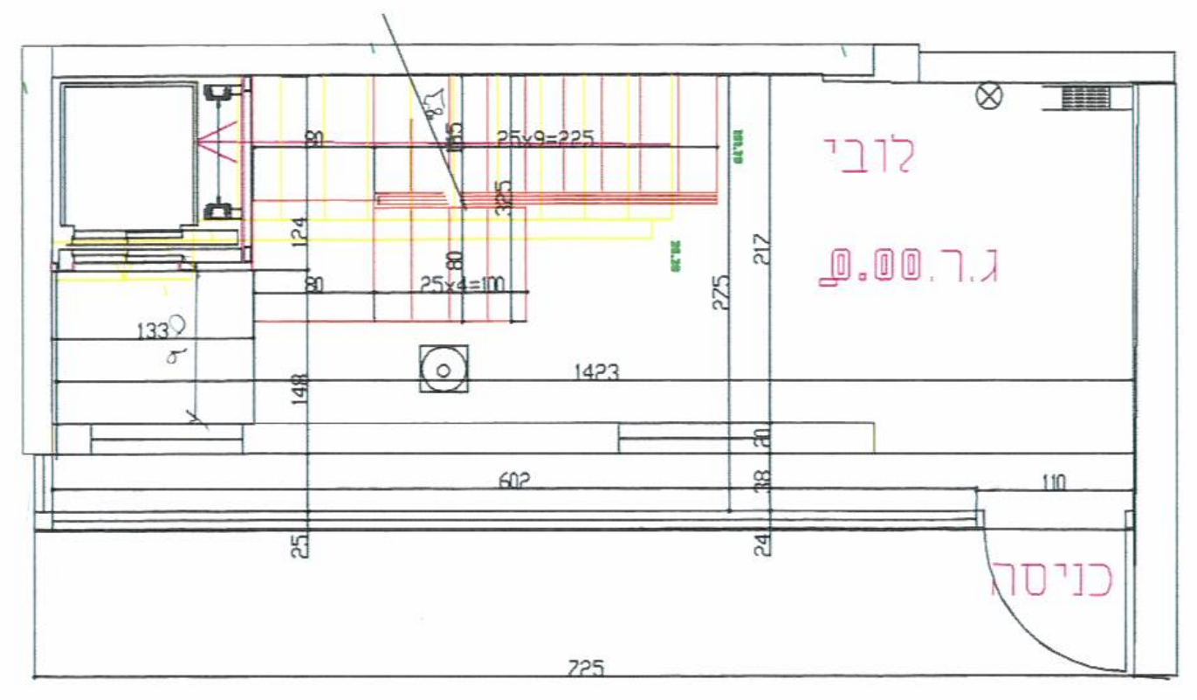

קומת קרקע 1:50

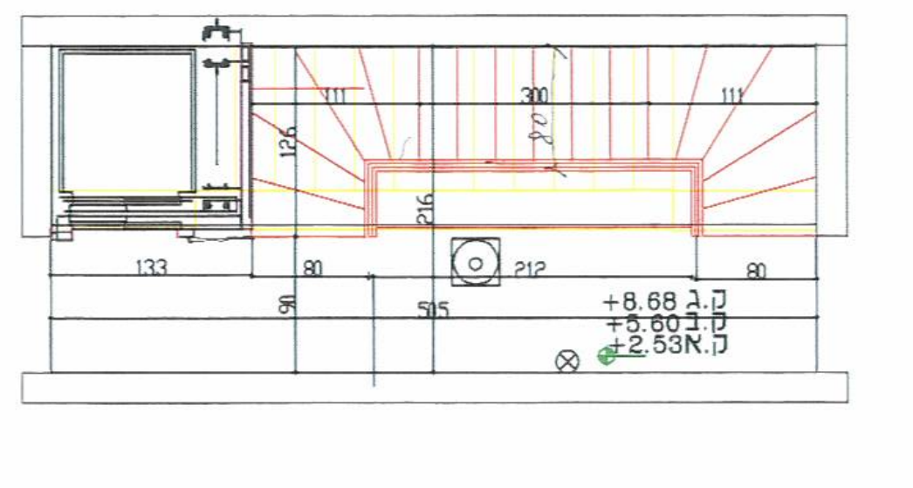

קומה טיפוסית 1:50