016

20

26

הועדה המקומית לבנין ערים הרצליה

שטח תכנון ובנין עיר ....

תיק בניה מס׳ ....

הגשה ....

הרשות המקומית ....

גוש 6529 חלקה 12 רחוב (תחרה 162 ש) בית מס׳ ....

תכנית בנין עיר מפורטת מס׳ .... שהודעה בדבר מתן תוקף לה׳ פורסמה בילקוט פרסומים מס׳ ....

מיום .... האזור לפי תכנית עיר מפורטת ....

בעל הבנין עג׳דגמן כתובתו הרצליה

בעל הקרקע .... כתובתו ....

הבונה .... כתובתו ....

עורך התכנית .... כתובתו ....

מטרת הבקשה סגירת מרפסת ורצוף בגן

שטח החלקה	4604 ממ״ר		
שטח הבניה המותר	ממ״ר		
שטח בניה קיים	159.56 ממ״ר	נפח קיים	ממ״ק
שטח בניה מבוקש	19.00 ממ״ר	נפח מבוקש	ממ״ק
ס״ה	ממ״ר	ס״ה	ממ״ק
שטח לבניני עזר קיים	ממ״ר	נפח לבניני עזר	ממ״ק
שטח לבניני עזר מבוקש	ממ״ר	נפח לבניני עזר מבוקש	ממ״ק
ס״ה	ממ״ר	ס״ה	ממ״ק

יסודות ב״מ מחיצות .... קירות ....

טיח חיצוני או צבע בחוץ

גג קיים עמודים קיימים קירות בלוקים

אני מצהיר בזה כי הפרטים המוגשים לעיל נכונים.

בעל הקרקע (א) מאיר גניקרמן

בעל הבנין x מאיר גניקרמן

הבונה ....

עורך התכנית

24.IV.61

הועדה המקומית לבניה ולתכנון ערים
הרצליה
רשיון מס׳ 3446 תאריך 4.6.61
נתאשר ע״י הועדה
בישיבה מס׳ 24
בתאריך 18.5.61
מהנדס העיריה

הערה: (א) קרקע בבעלות קרן הקיימת לישראל, החתם הבקשה גם על ידה.

״אמנוגרף״ בע״מ, ת״א, רח׳ הר־סיני 2, טל. 63964

נסרק

תרשים המגרש קנ.מ. 1:250

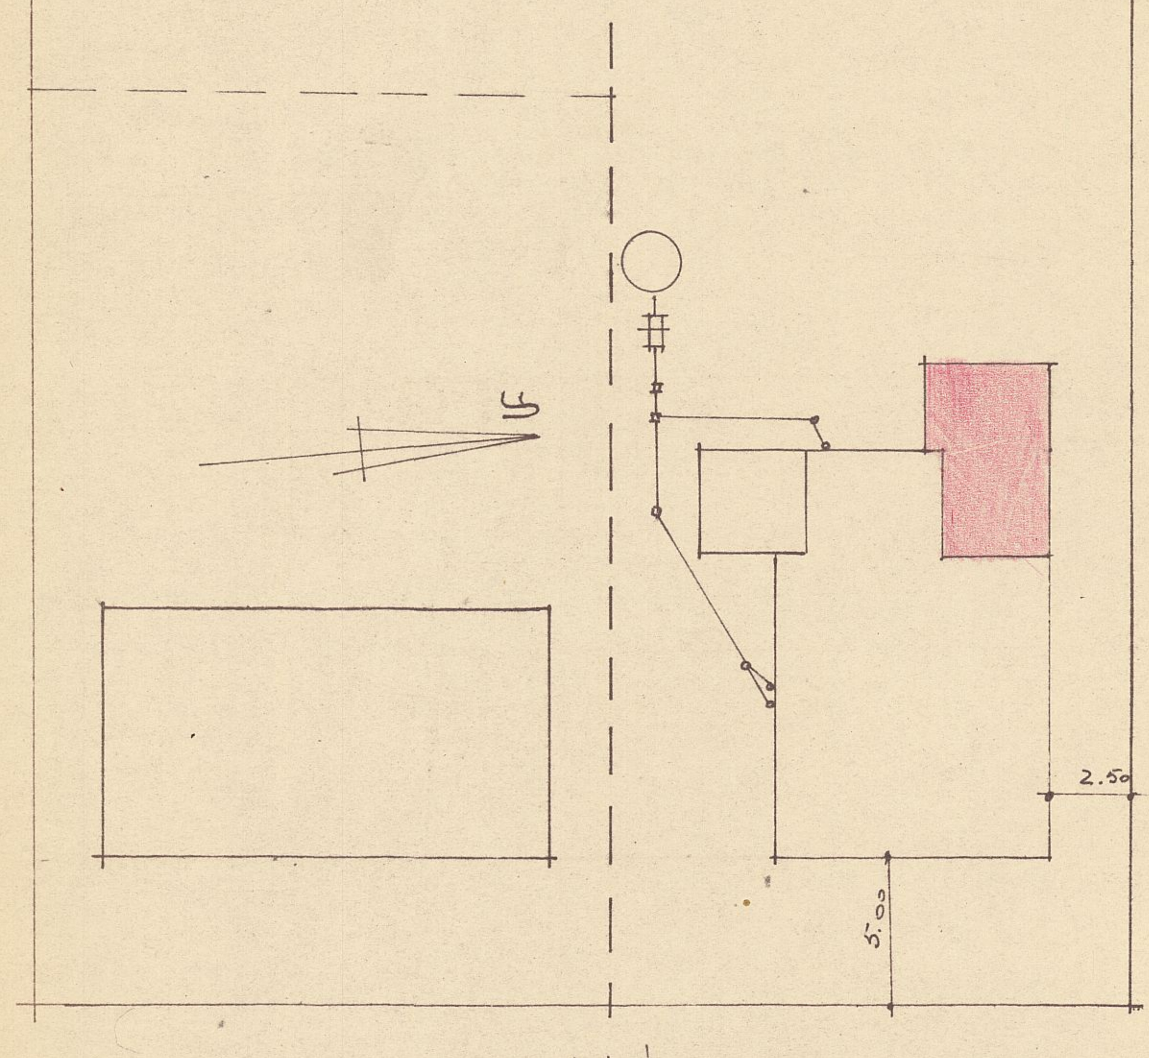

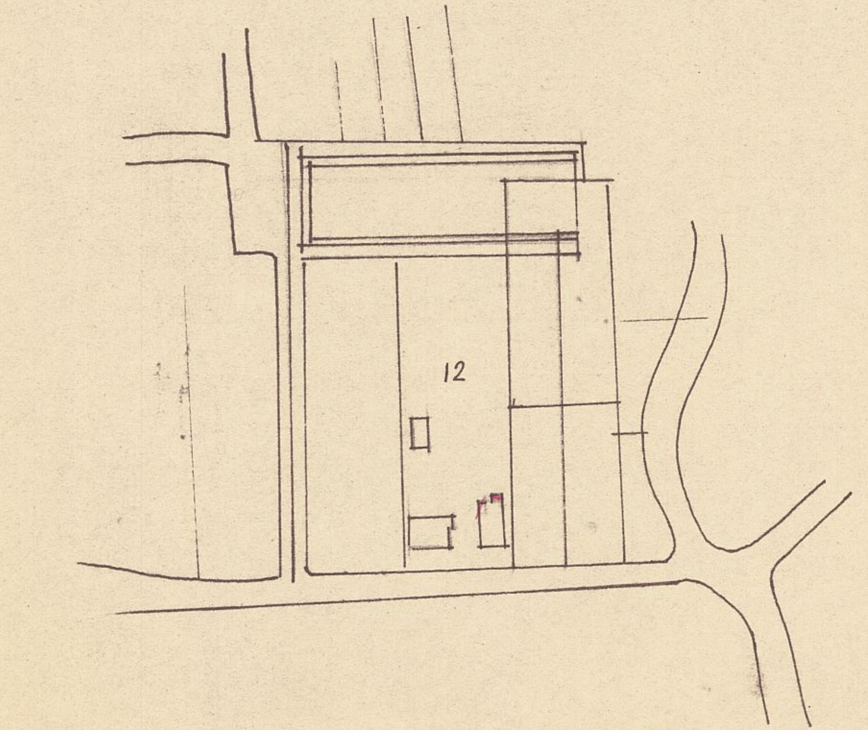

תרשים הגוש קנ.מ. 1:500

תכנית קומה א.
1:100

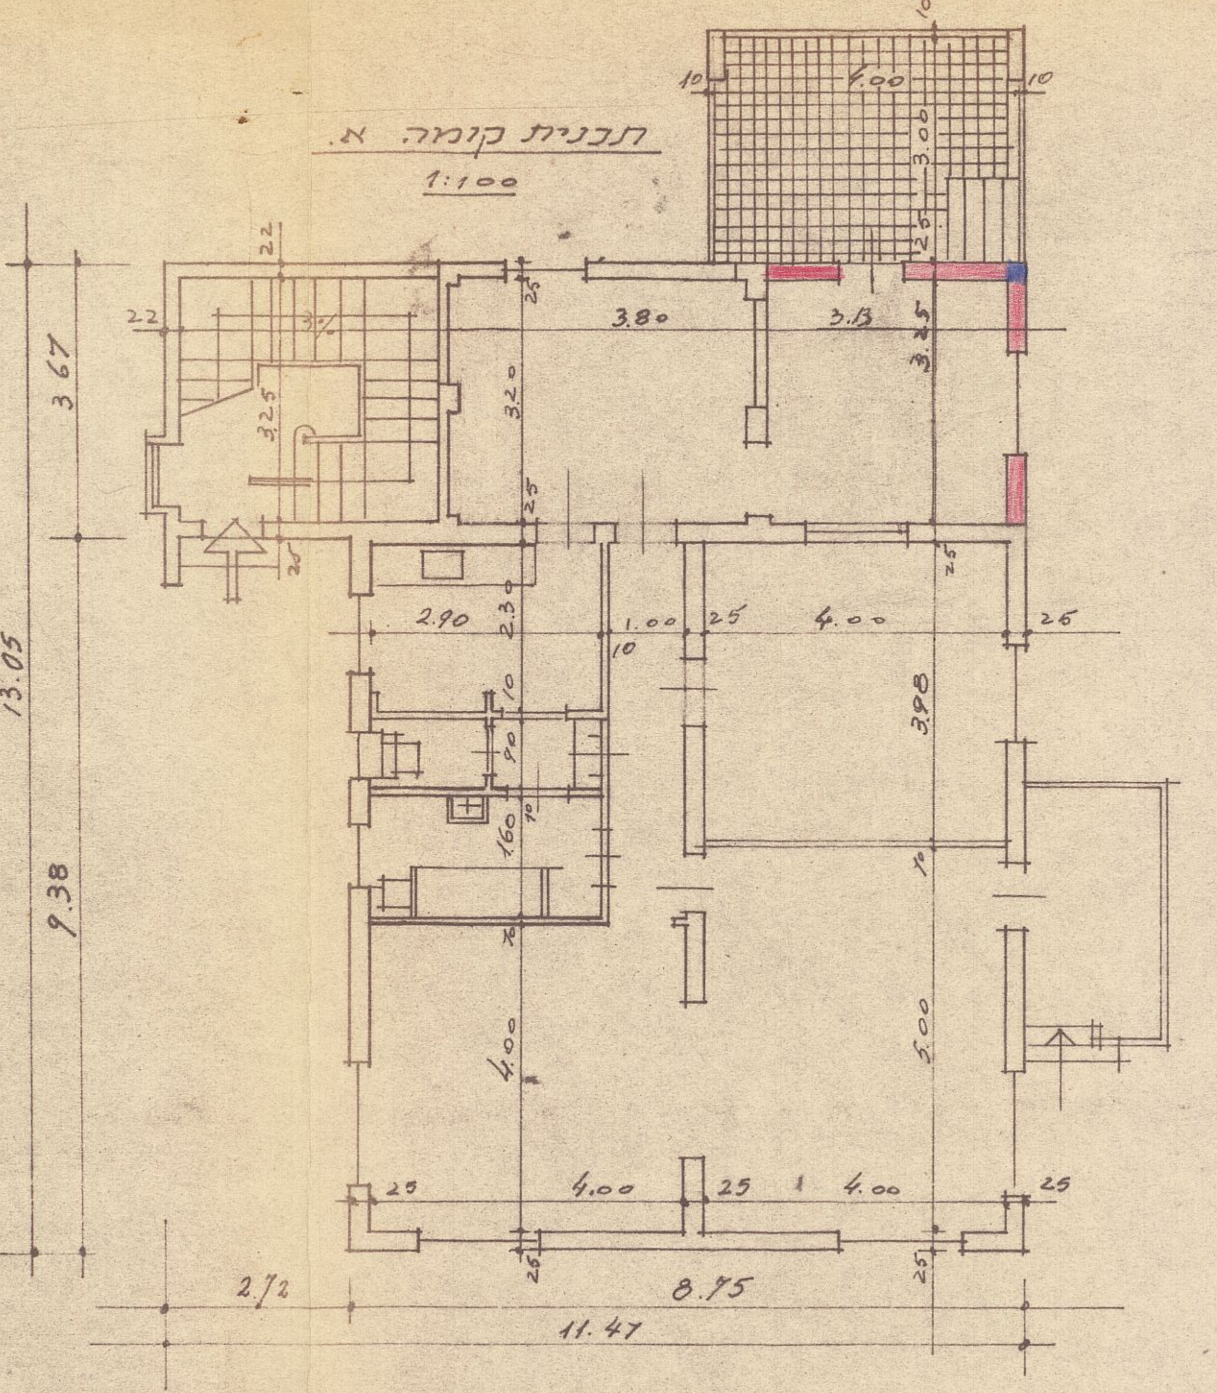

תכנית קומה ב
1:100

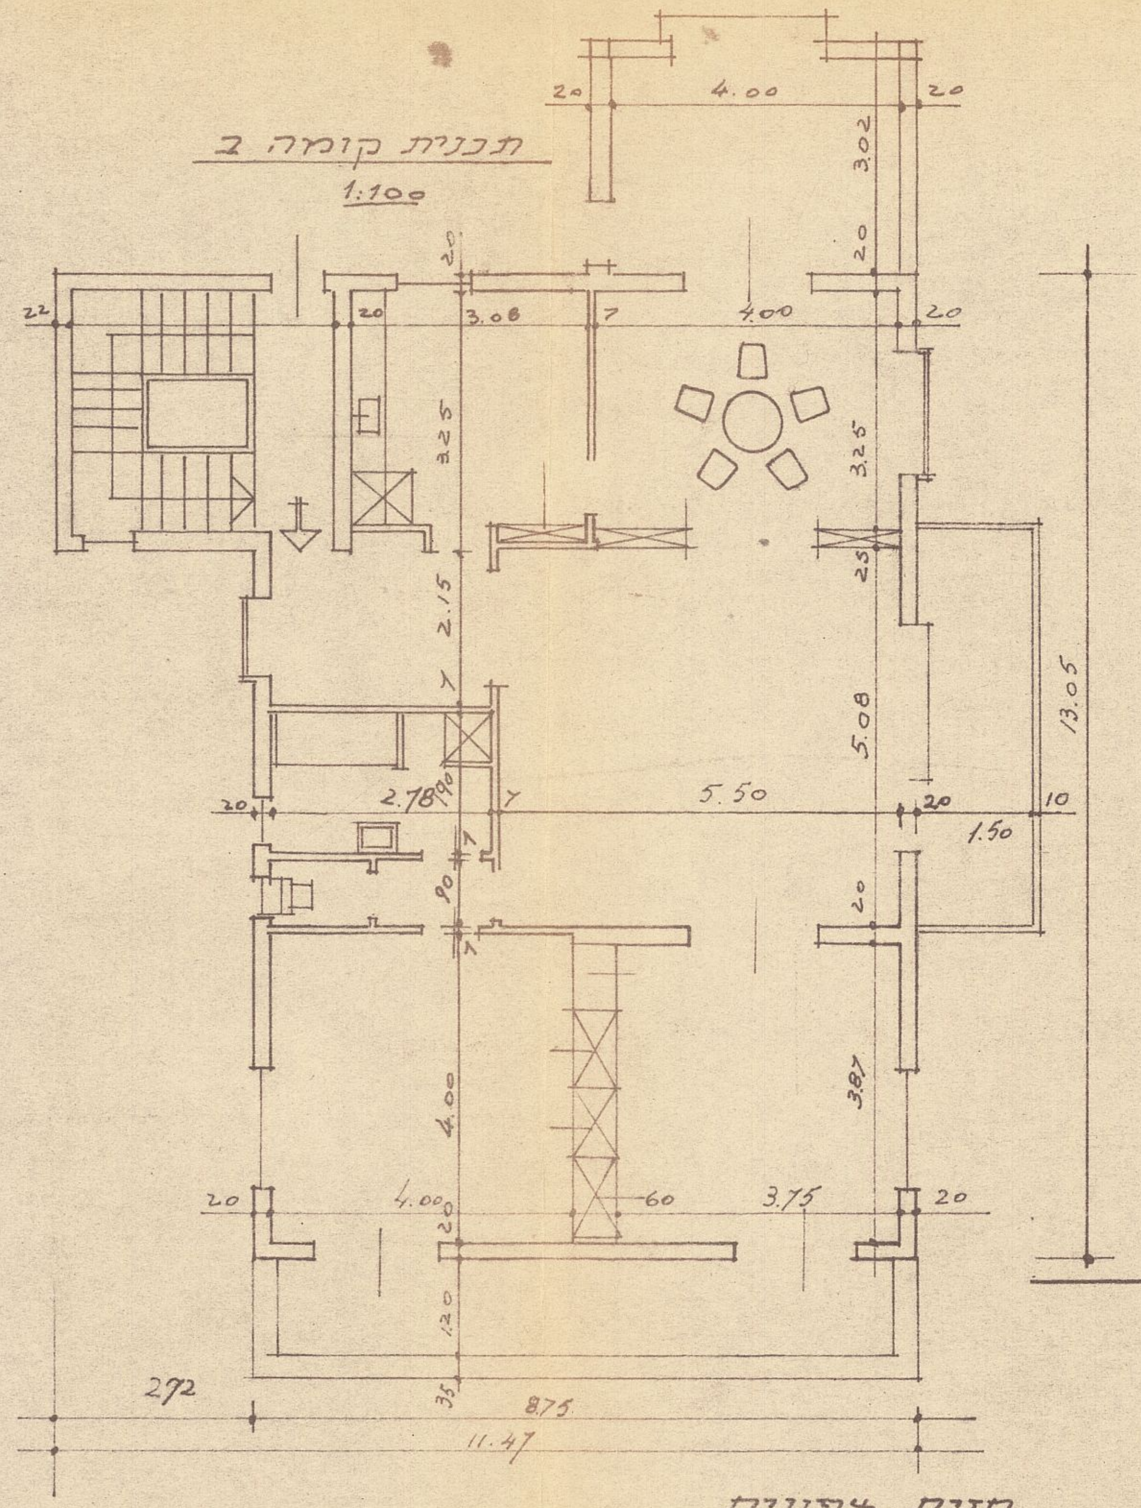

חתך א-א

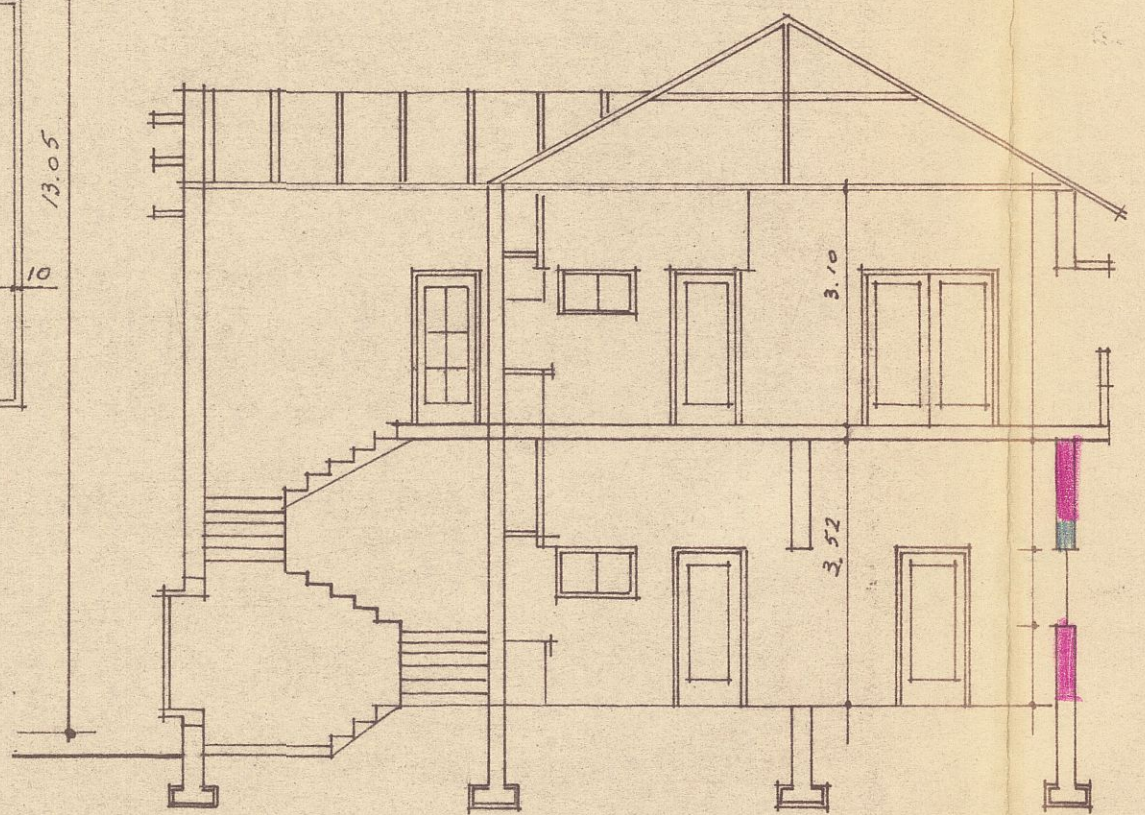

חזית מערבית

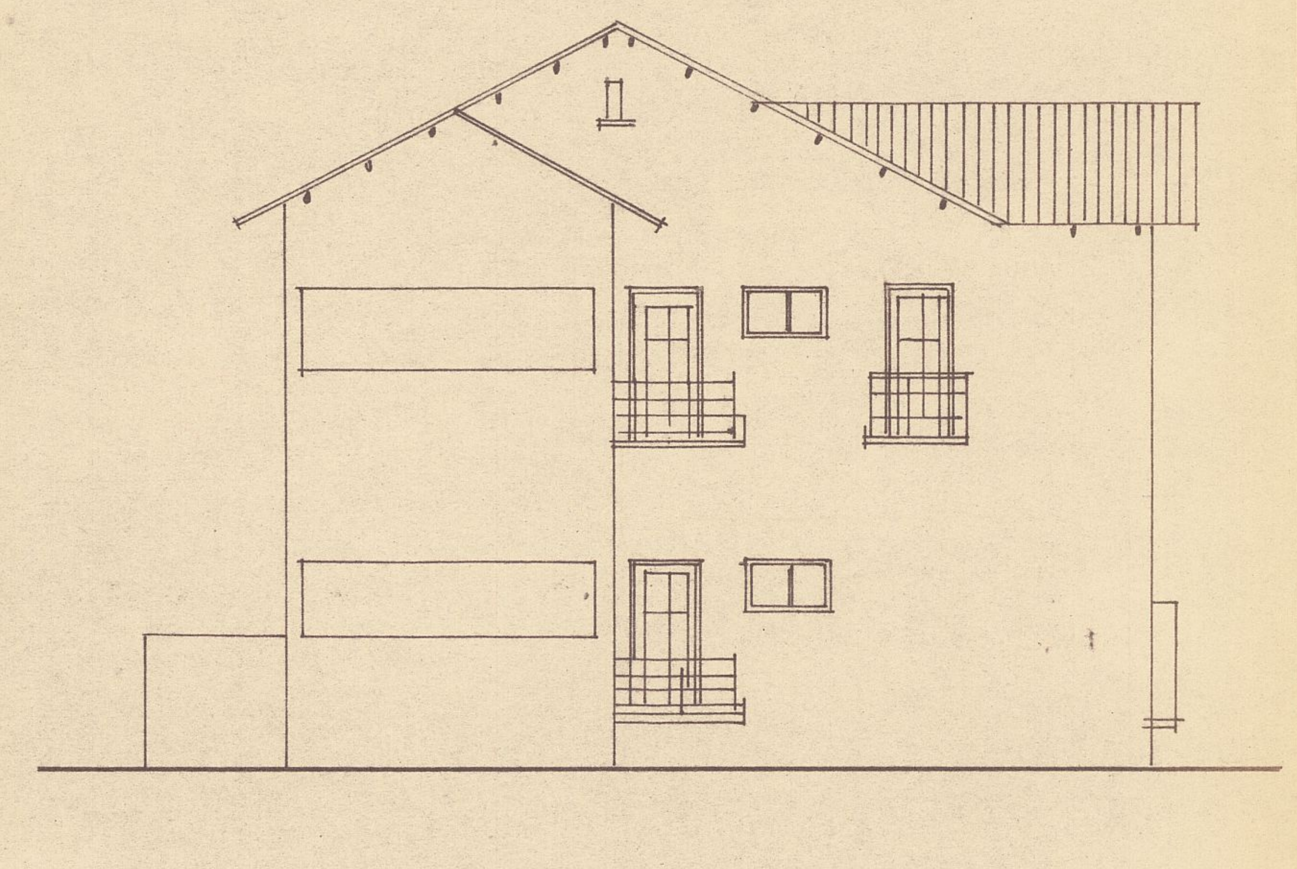

חזית מזרחית

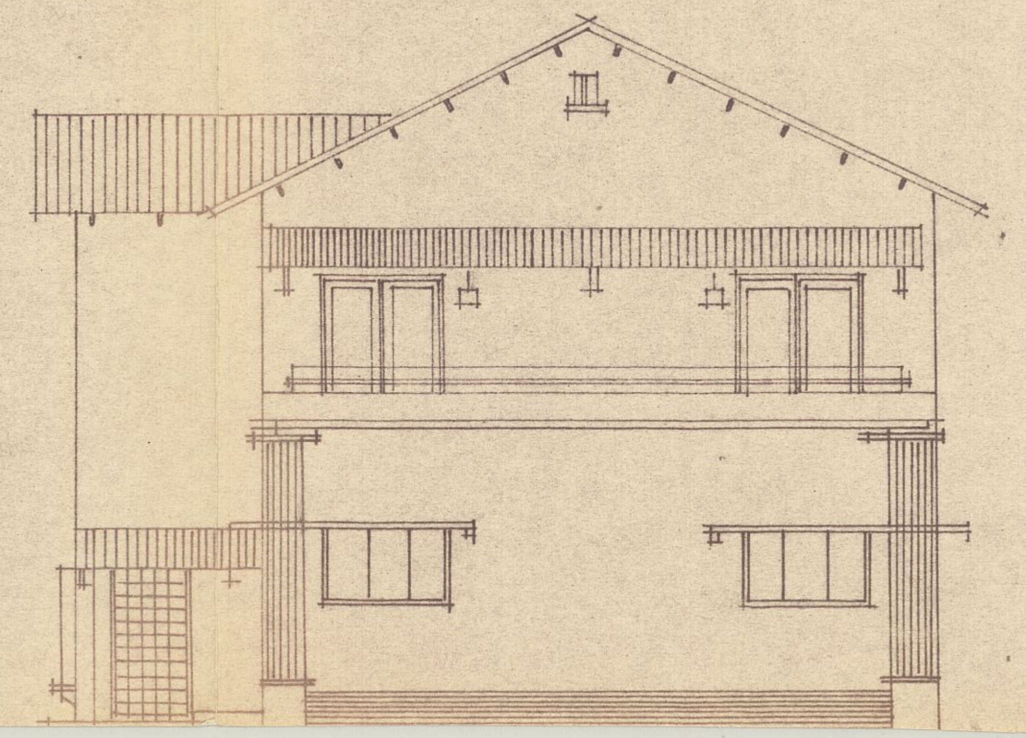

חזית צפונית

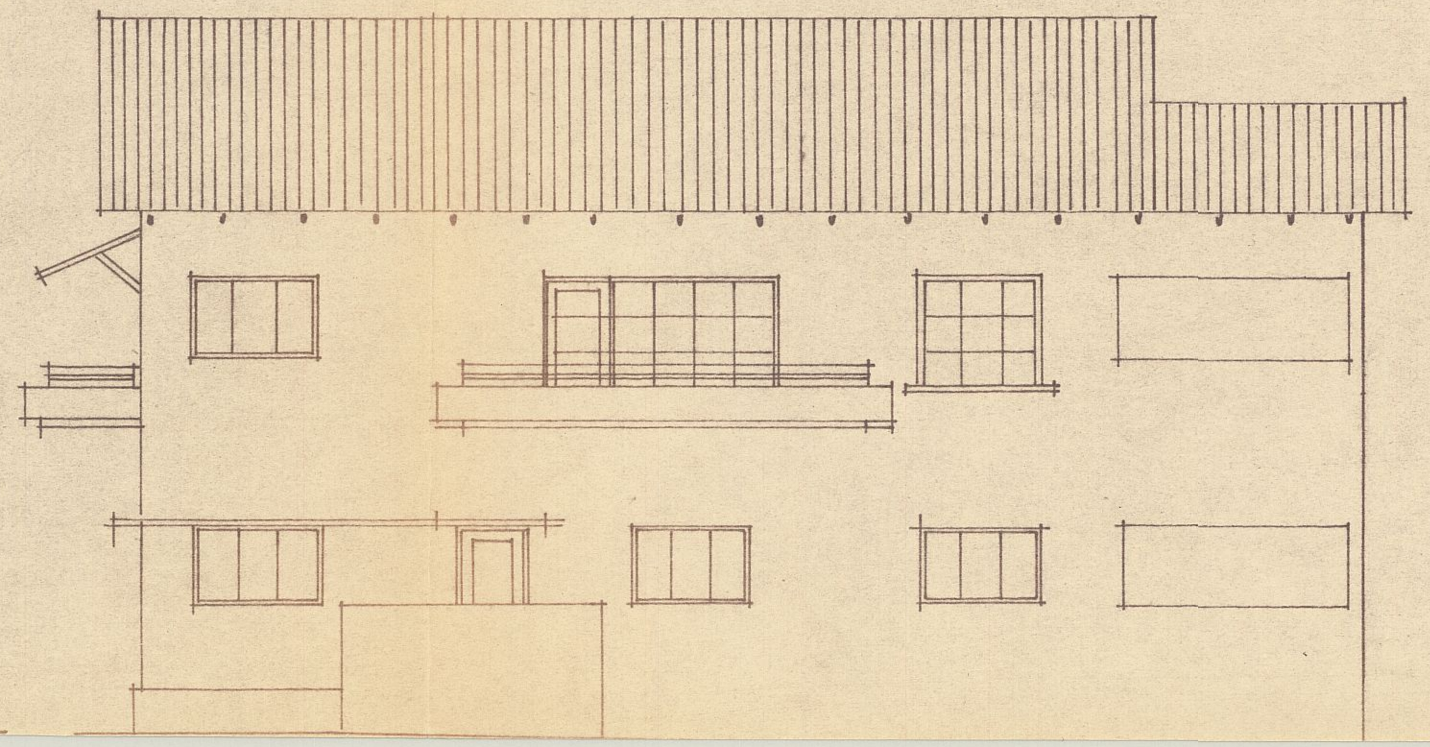

חזית דרומית