הוועדה המקומית לבניה ולתכנון עיר הרצליה

תיק מס׳

נספח לבקשה להיתר בניה (מיפרט)

008

20

א. תאור הבנין

1. המקום	הרצליה	הרחוב ... מס׳ ... גוש 6529 חלקה 157 ת.ב.ע. ... מגרש (2)
	השם	המען / מס׳ טלפון
2. המבקש	ל.מ.פ. בע״מ, קבלנים	ע״י מ. מנקס. הרצליה
3. בעל הנכס	מר שניידרמן	רח׳ הנדיב, הרצליה.
4. עורך התכנית	מהנדס ש. י. יציב	רח׳ עמנואל 19 ת״א / 241941
5. האחראי לביצוע העבודה		
6. אזור הבניה	■ מגורים ☐ מסחר ☐ תעשיה ☐ בנין צבורי ☐ חקלאי ☐	
7. שטח	המגרש / החלקה: 1503.00 ממ״ר. אחוז הבניה המותר: % 70% ב-3 קומות.	
8. מטרת הבנין	■ מגורים ☐ הארחה ☐ עסקים ☐ תעשיה ☐ חקלאי ☐ צבורי	
9. מהות המבנה ותכליתו	בנין מגורים (בית משותף)	
10. תאור העבודה המוצעת	■ בנין חדש ☐ תוספת לבנין קיים ☐ הריסה ☐ תקונים / שינוי בשימוש ממטרה: ... למטרה: ...	
11. האם הבניה היא עבור:	☐ משרד השיכון ☐ הסוכנות היהודית	

עיריית הרצליה
מחלקת ההנדסה
נתקבל ב: 31.1.1969
גרשם
מס׳ סדורי ... מס׳ התיק
נענה ביום
מכתב מס׳

ב. מבנה הבנין

קומה	קיים	מוצע	סך הכל	אחוז הבניה	מגורים בדירות עד 45 ממ״ר	עד 65 ממ״ר	עד 90 ממ״ר	מעל 90 ממ״ר	עסק הארחה וכו׳ עד 20 ממ״ר	מעל 20 ממ״ר	צבורי	שונות	מס׳ חדרים קיים	מוצע
1.	2.	3.	4.	5.	6.	7.	8.	9.	10.	11.	12.	13.	14.	15.
מרתף	—	מקלט	—											
ק׳ קרקע התחתונה	—	—	—											
קרקע	—	—	—											
בינים	—	—	—											
א׳	—	353.1	353.1	23.43									—	17.5
ב׳	—	353.1	353.1	23.43									—	17.5
ג׳	—	353.1	353.1	23.43									—	17.5
ד׳														
ה׳														
ו׳														
מבני עזר														
סך הכל		1059.3	1059.3	70.29									—	52.5

הנפח המוצע לפי ההיתר: של המבנה העיקרי ... ממ״ע. של מבנה העזר ... ממ״ע.

ג. השימוש בבנין

1. הבניה המוצעת למגורים

דירות בנות:	שטח כל דירה-ממ״ר	מס׳ דירות מכל סוג	שטחים ממ״ר: כל הדירות	מזה: רצפות חדרי-דיור בלבד, ומרפסות מקורות	רצפות שרותים ופרוזדורים ר׳ מרפסות מקורות	מרפסות בלתי מקורות	מספר החדרים: דיור	מטבחים	רחצה	ב״ש	אחרים
1.	2.	3.	4.	5.	6.	7.	8.	9.	10.	11.	12.
חדר אחד	ראה הרישום מיוחד של הדירות בכל קומה המציין מספר חדרים ושטח כל דירה	—									
2 חדרים		—									
3 ״		6					18	6	6	6	
4 ״		6					24	6	6	6	
״ 3½		3					10.5	3	3	3	
6 ״											
7 ״ ויותר											
חדרים נוספים לדירות קיימות											
מבני עזר											
סך הכל		15					52.5	15	15	15	

2. הבניה הקיימת והמוצעת לתעשיה ומלאכה

פרטים	קיים: שטח	גובה	נפח	% הבניה	מוצע: שטח	גובה	נפח	% הבניה	סך הכל: שטח	נפח	% הבניה	הערות
1.	2.	3.	4.	5.	6.	7.	8.	9.	10.	11.	12.	13.
אולמי מלאכה												
משרדים												
שירותים												
מכבסת												
מבני עזר												
סך הכל												

3. הבניה המוצעת למטרות אחרות (הארחה, עסקים ומשרדים, בניני צבור, מבני משק חקלאי, מטרות שונות)

השמוש המיועד	שטחים ממ״ר: ס״ה ממ״ר	מזה: חדרים	אולמות	אחסנה	שירותים	מספר חדרים ואולמות: חדרים	אולמות	אחסנה	שירותים
1.	2.	3.	4.	5.	6.	7.	8.	9.	10.
מבני עזר									

4. חלקי בנין אחרים — הבניה המוצעת שטח בממ״ר

חדר מדרגות	מרפסות שלא נכללו בדירות	מעליות	חדרי הסקה	חדרי כביסה	מקלטים	קומת עמודים	מחסנים	מוסכים		סך הכל
1. 38.86	2. 326.01	3. —	4. —	5. —	6. —	7. —	8. —	9. —	10. —	11.
38.86	326.01	—	—	—	—	—	—	—	—	מ״ר 364.86

ד. חומר הבניה

קירות חיצוניים	☐ בטון מזוין ■ לבנין בטון או בלוקים ☐ לבני סליקט ☐ לבנים שרופות ☐ אבן טבעית ☐ אבן מלאכותית ☐ איטונג ☐ עץ ☐ ברזל ☐ חמרים אחרים
תקרות	■ בטון מזוין ☐ עץ ☐ חומר אחר
גג:	■ בטון מזוין ☐ רעפים ☐ אסבסט ☐ פח ☐ חומר אחר

ה. גדרות קיימות — מטר אורך מוצעות 36.00 מטר אורך

ו. מקרא

🟦 בטון או בטון מזוין
🟥 בלוקים או לבנים מבטון
☐ אבן
☐ סיליקט או לבנים אדומות
☐ עץ
☐ חומר אחר
☐ איטונג
☐ להריסה

הערות: ...

הנני מאשר כי הידיעות הנ״ל הן נכונות

תאריך ... חתימת המבקש: ל. מ. פ. חברה לבנין בע״מ ... חתימת עורך התכנית:

חתימת בעל הנכס: ע׳ פרסן שניידרמן

לשימוש הועדה המקומית בלבד	מס׳ ההיתר	תאריך ההיתר	תאריך התחלת בניה	תאריך גמר בניה

אשורים של רשויות חוץ:

הוועדה המקומית לבניה ולתכנון ערים הרצליה
רשיון מס׳: 117 תאריך 5.5.69
נתאשר ע״י הועדה המקומית
בישיבתה מס׳ 32
בתאריך 18.2.69
מזכיר ... יו״ר

מדף 4801/1

1768/ס

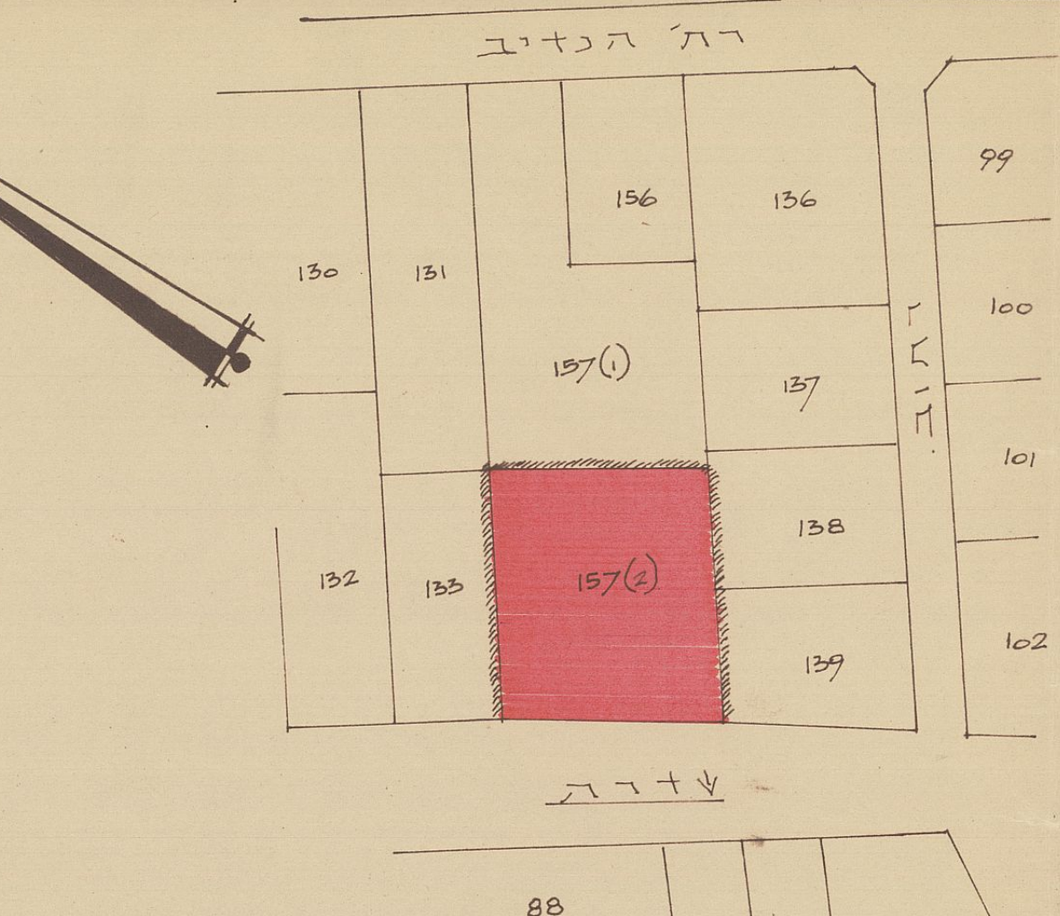

תרשים הסביבה
1:1250

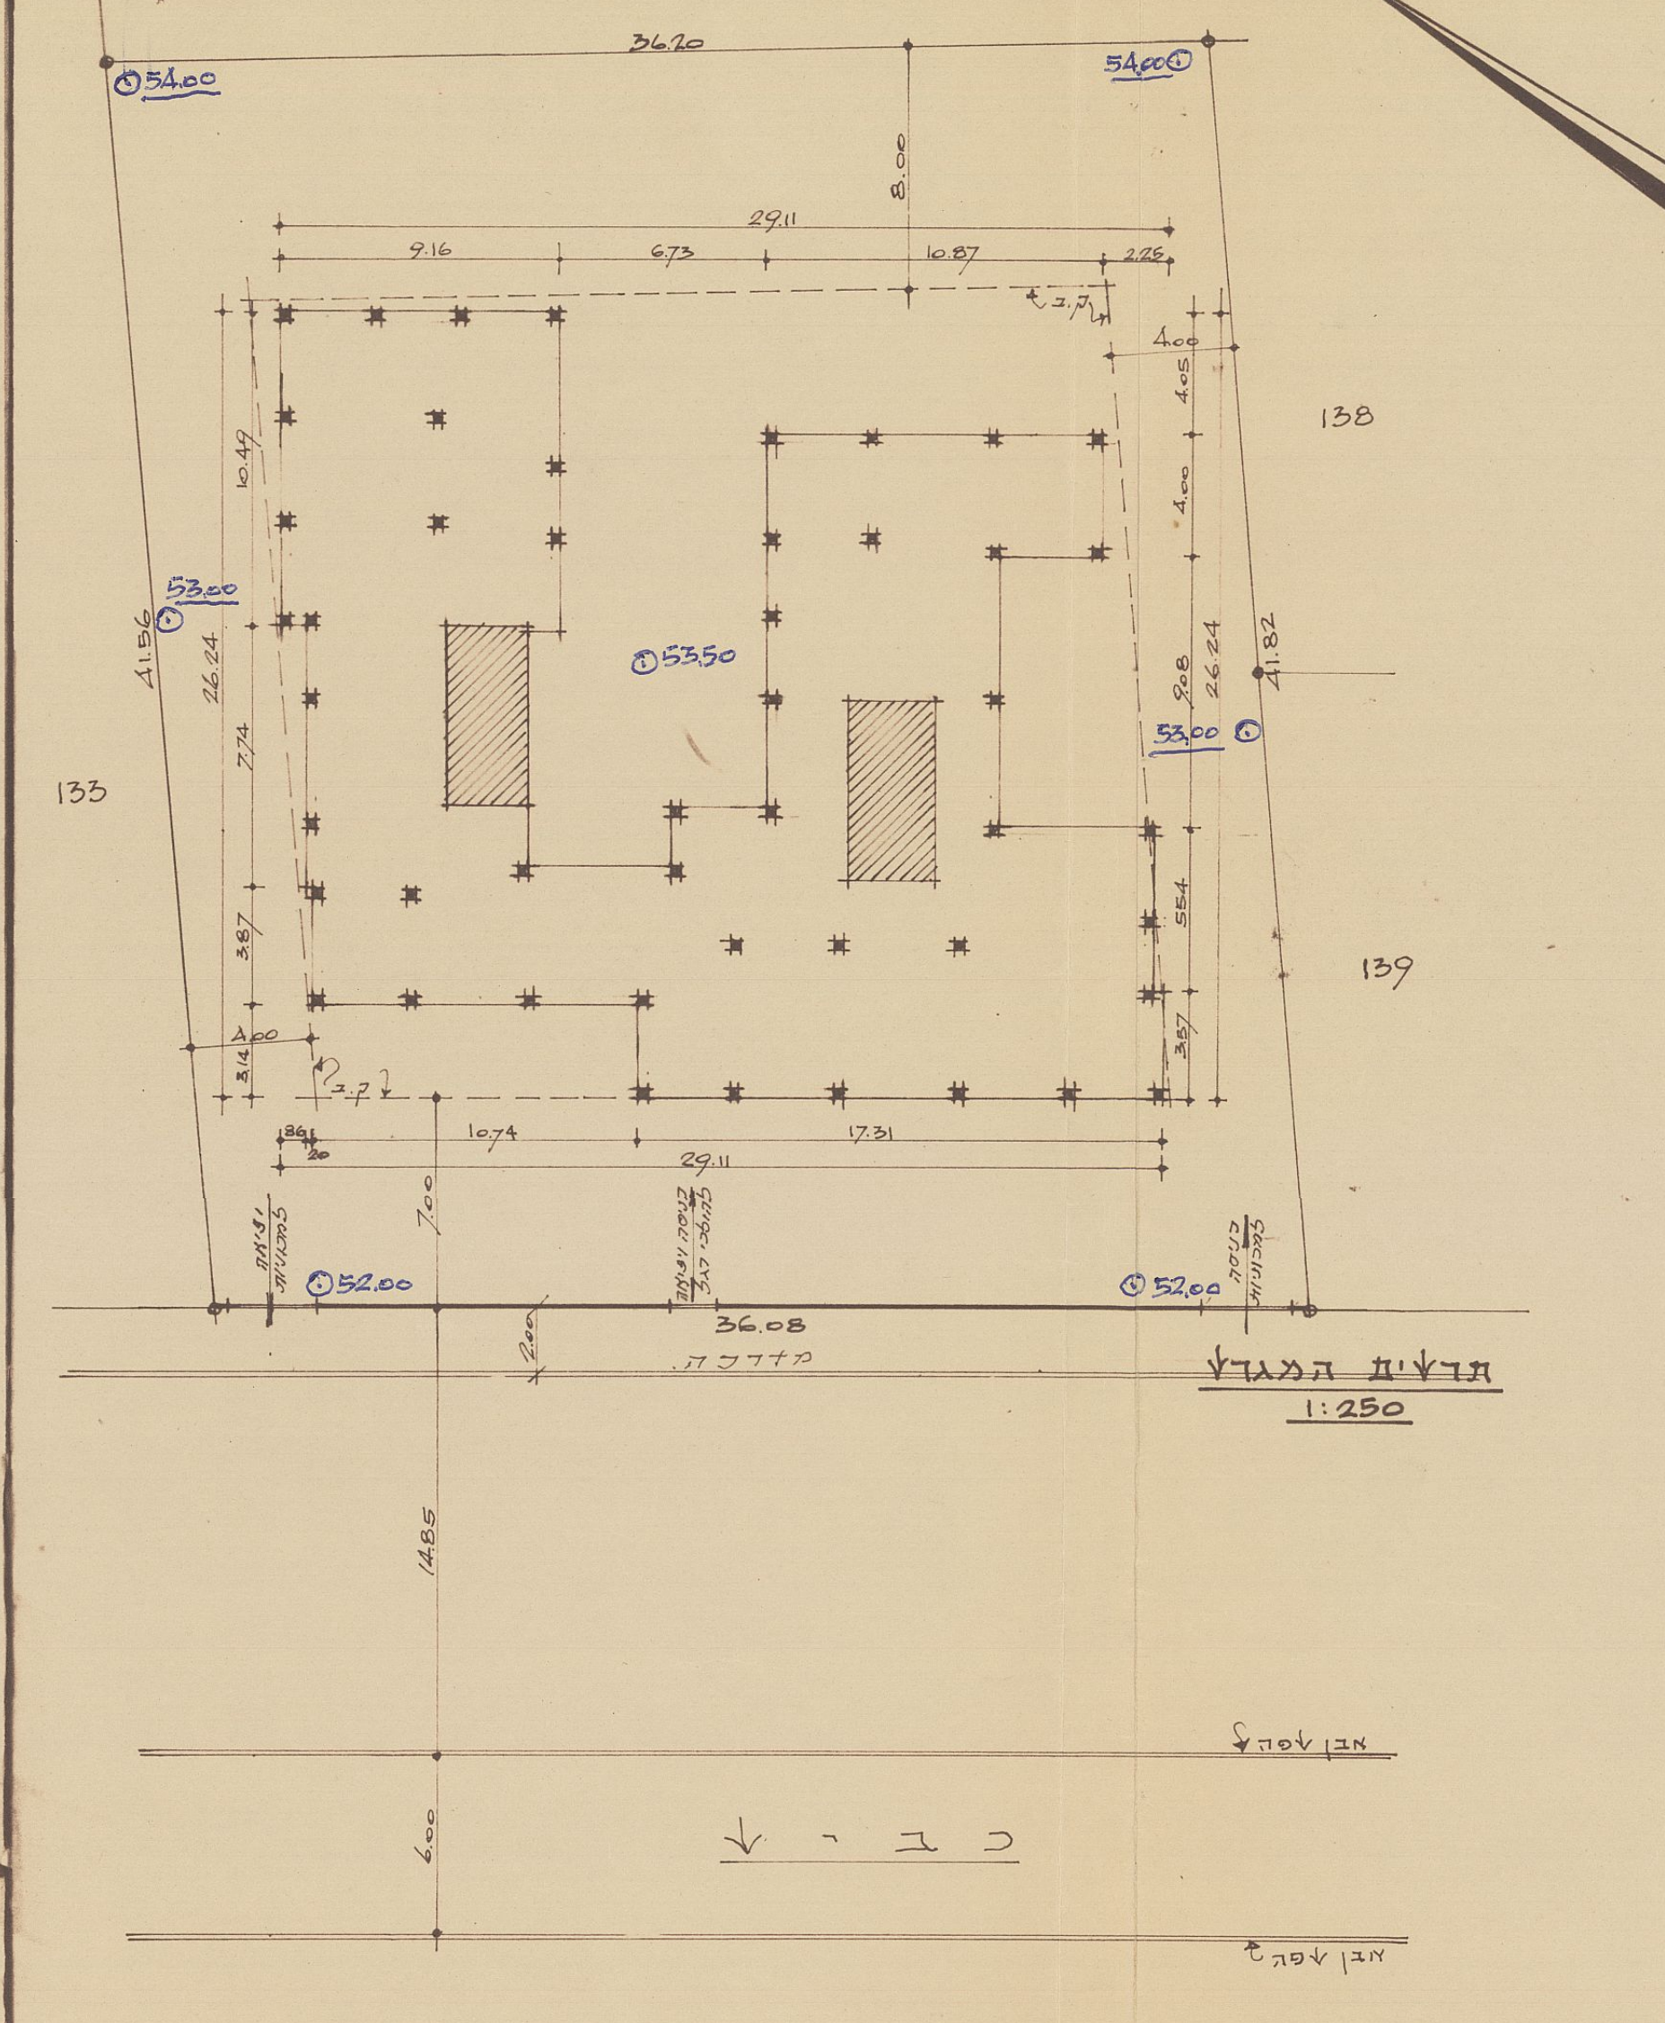

תרשים המגרש
1:250

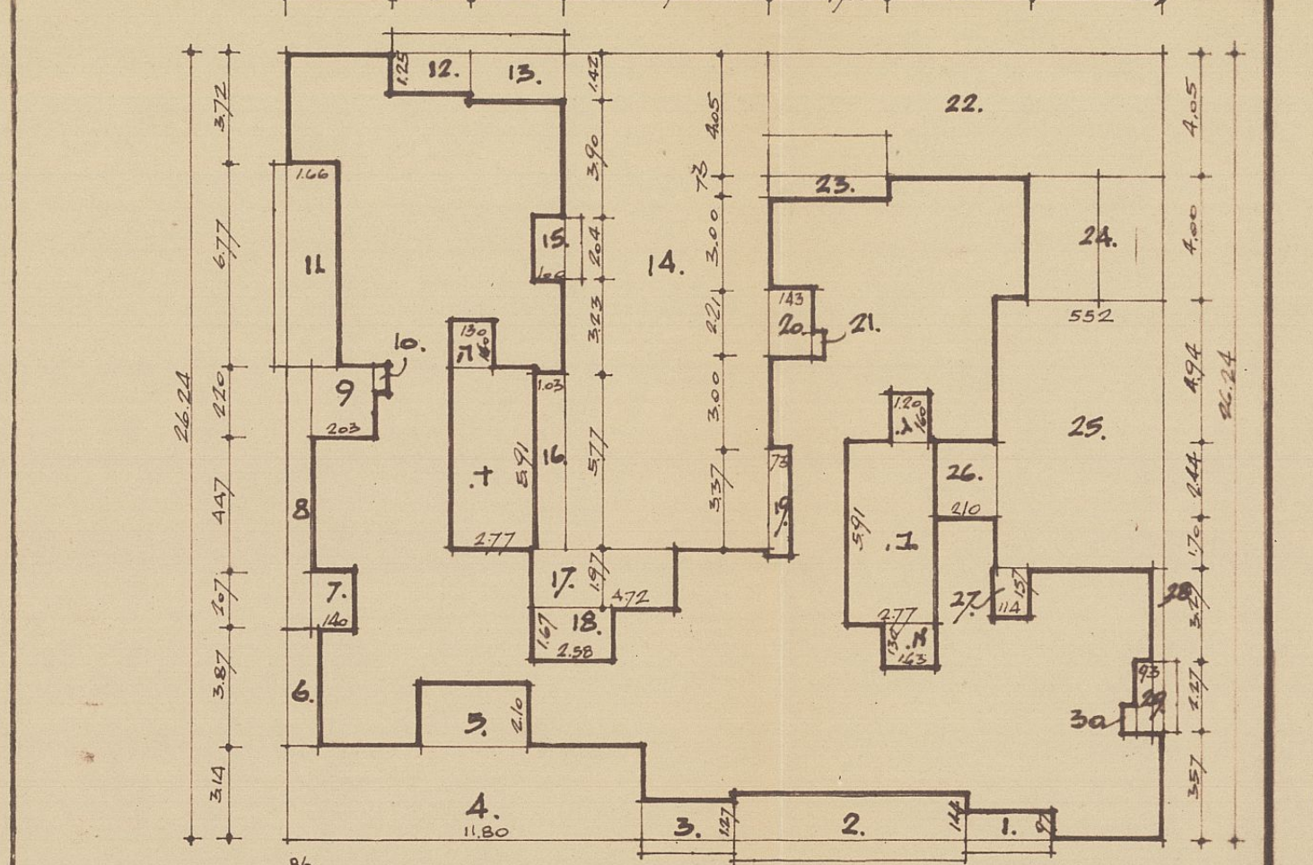

חישוב השטחים והנפחים

קומה טיפוסית: שטח המסגרת: 763.85 = 26.24 × 29.11

מרפסות:	הורדות:
4.34 = 2.89 × 1.50	1. 2.80 = 0.97 × 2.89
16.09 = 2.09 × 7.70	2. 11.09 = 1.44 × 7.70
5.37 = 3.12 × 1.72	3. 3.96 = 3.12 × 1.27
	4. 37.05 = 3.14 × 11.80
7.50	5. 7.50 = 3.57 × 2.10
	6. 4.10 = 3.87 × 1.06
2.90	7. 2.90 = 1.40 × 2.07
	8. 7.52 = 8.74 × 0.86
4.47	9. 4.47 = 2.20 × 2.03
0.22	10. 0.22 = 0.30 × 0.74
13.95 = 6.77 × 2.06	11. 11.24 = 6.77 × 1.66
4.83 = 2.61 × 1.85	12. 3.26 = 2.61 × 1.25
6.26 = 3.10 × 2.02	13. 4.40 = 3.10 × 1.42
	14. 110.10 = 16.36 × 6.73
3.06 = 2.04 × 1.50	15. 2.04 = 2.04 × 1.00
	16. 5.94 = 5.77 × 1.03
	17. 9.30 = 1.97 × 4.72
4.31	18. 4.31 = 1.67 × 2.58
4.27 = 3.47 × 1.23	19. 2.53 = 3.47 × 0.73
4.27 = 2.21 × 1.93	20. 3.16 = 2.21 × 1.43
0.22	21. 0.22 = 0.30 × 0.74
	22. 53.14 = 13.12 × 4.05
8.06 = 3.97 × 2.03	23. 2.90 = 0.73 × 3.97
8.40 = 4.00 × 2.10	24. 17.40 = 4.00 × 4.35
	25. 50.12 = 9.08 × 5.52
5.12	26. 5.12 = 2.44 × 2.10
1.79	27. 1.79 = 1.57 × 1.14
	28. 0.98 = 0.30 × 3.27
3.02 = 2.27 × 1.33	29. 2.11 = 2.27 × 0.93
0.22	30. 0.22 = 0.30 × 0.74
שטח לקומה 108.67 מ״ר	א. 2.12 = 1.30 × 1.63
	ב. 16.37 = 2.77 × 5.91
נפח מרפסות לקומה 332.53 מ״ק	ג. 1.92 = 1.20 × 1.60
	ד. 16.37 = 2.77 × 5.91
שטח 3 קומות 326.01 מ״ר	ה. 2.08 = 1.30 × 1.60
נפח 3 קומות 997.59 מ״ק	410.75

שטח הקומה נטו 353.10 מ״ר

נפח הקומה (H=3.06) 1080.49 מ״ק

שטח 3 קומות 1059.30 = 353.10 × 3 מ״ר; נפח 3 קומות 3241.47 מ״ק

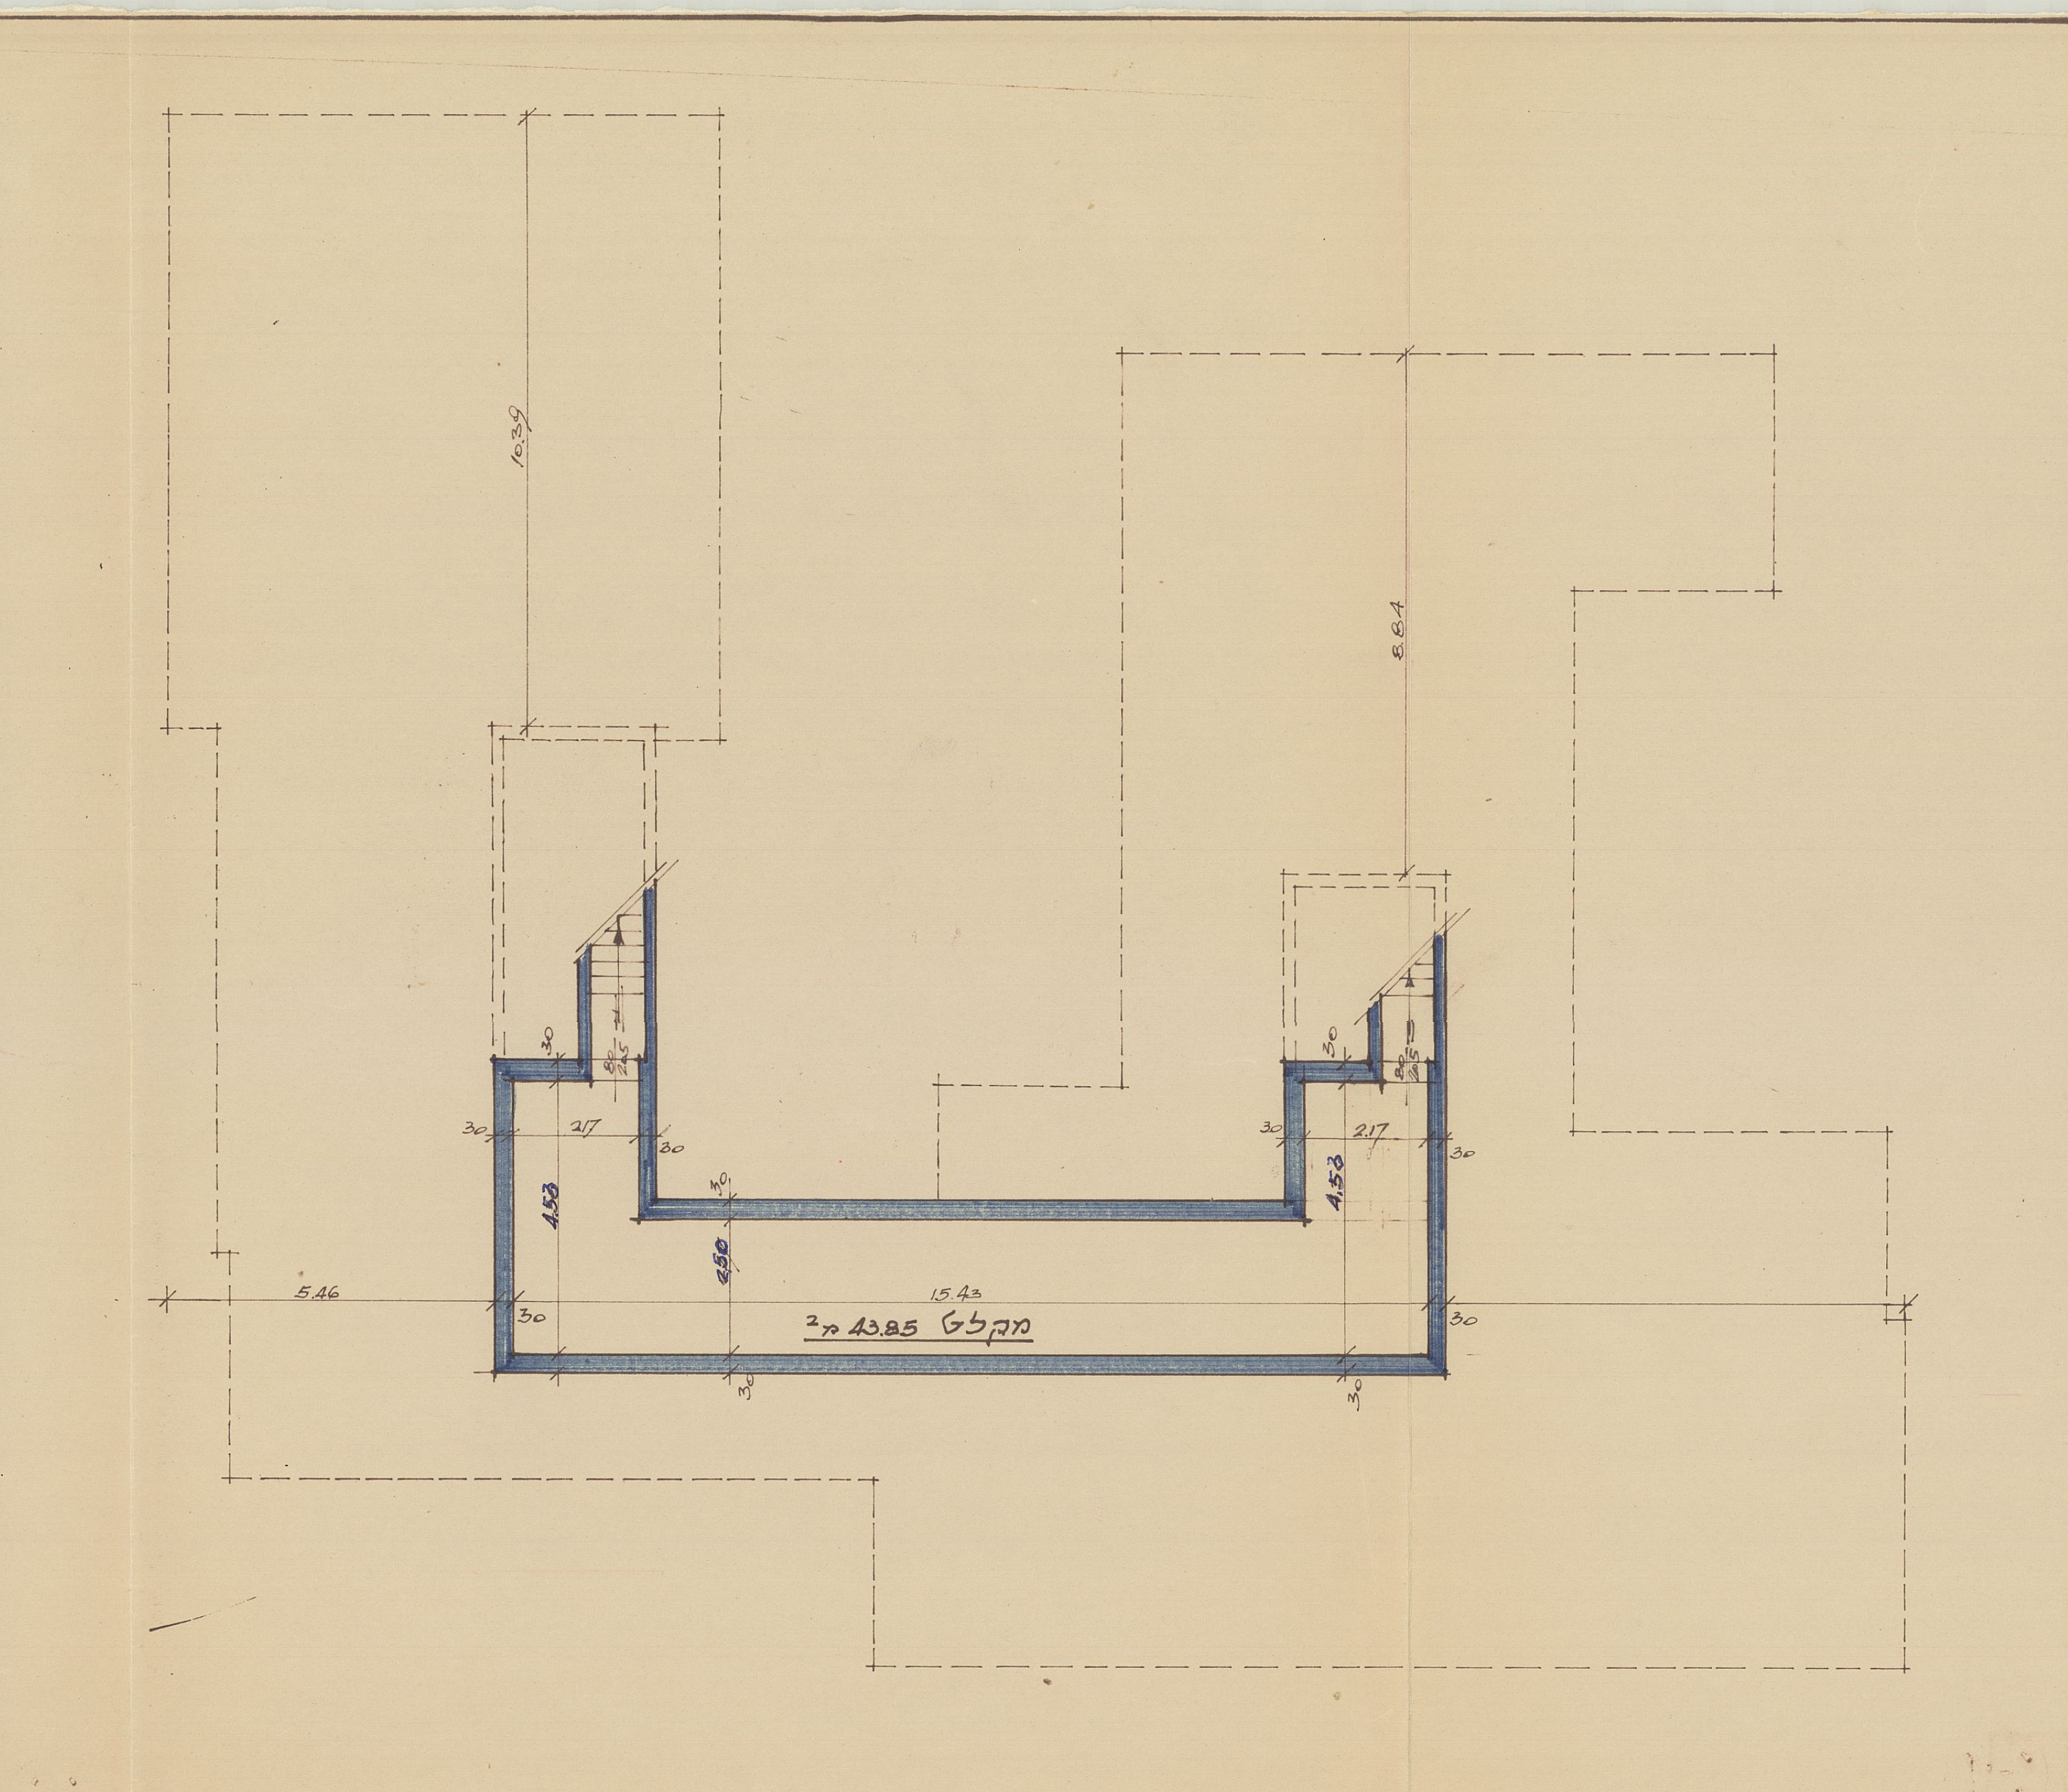

קומת מרתף 1:100

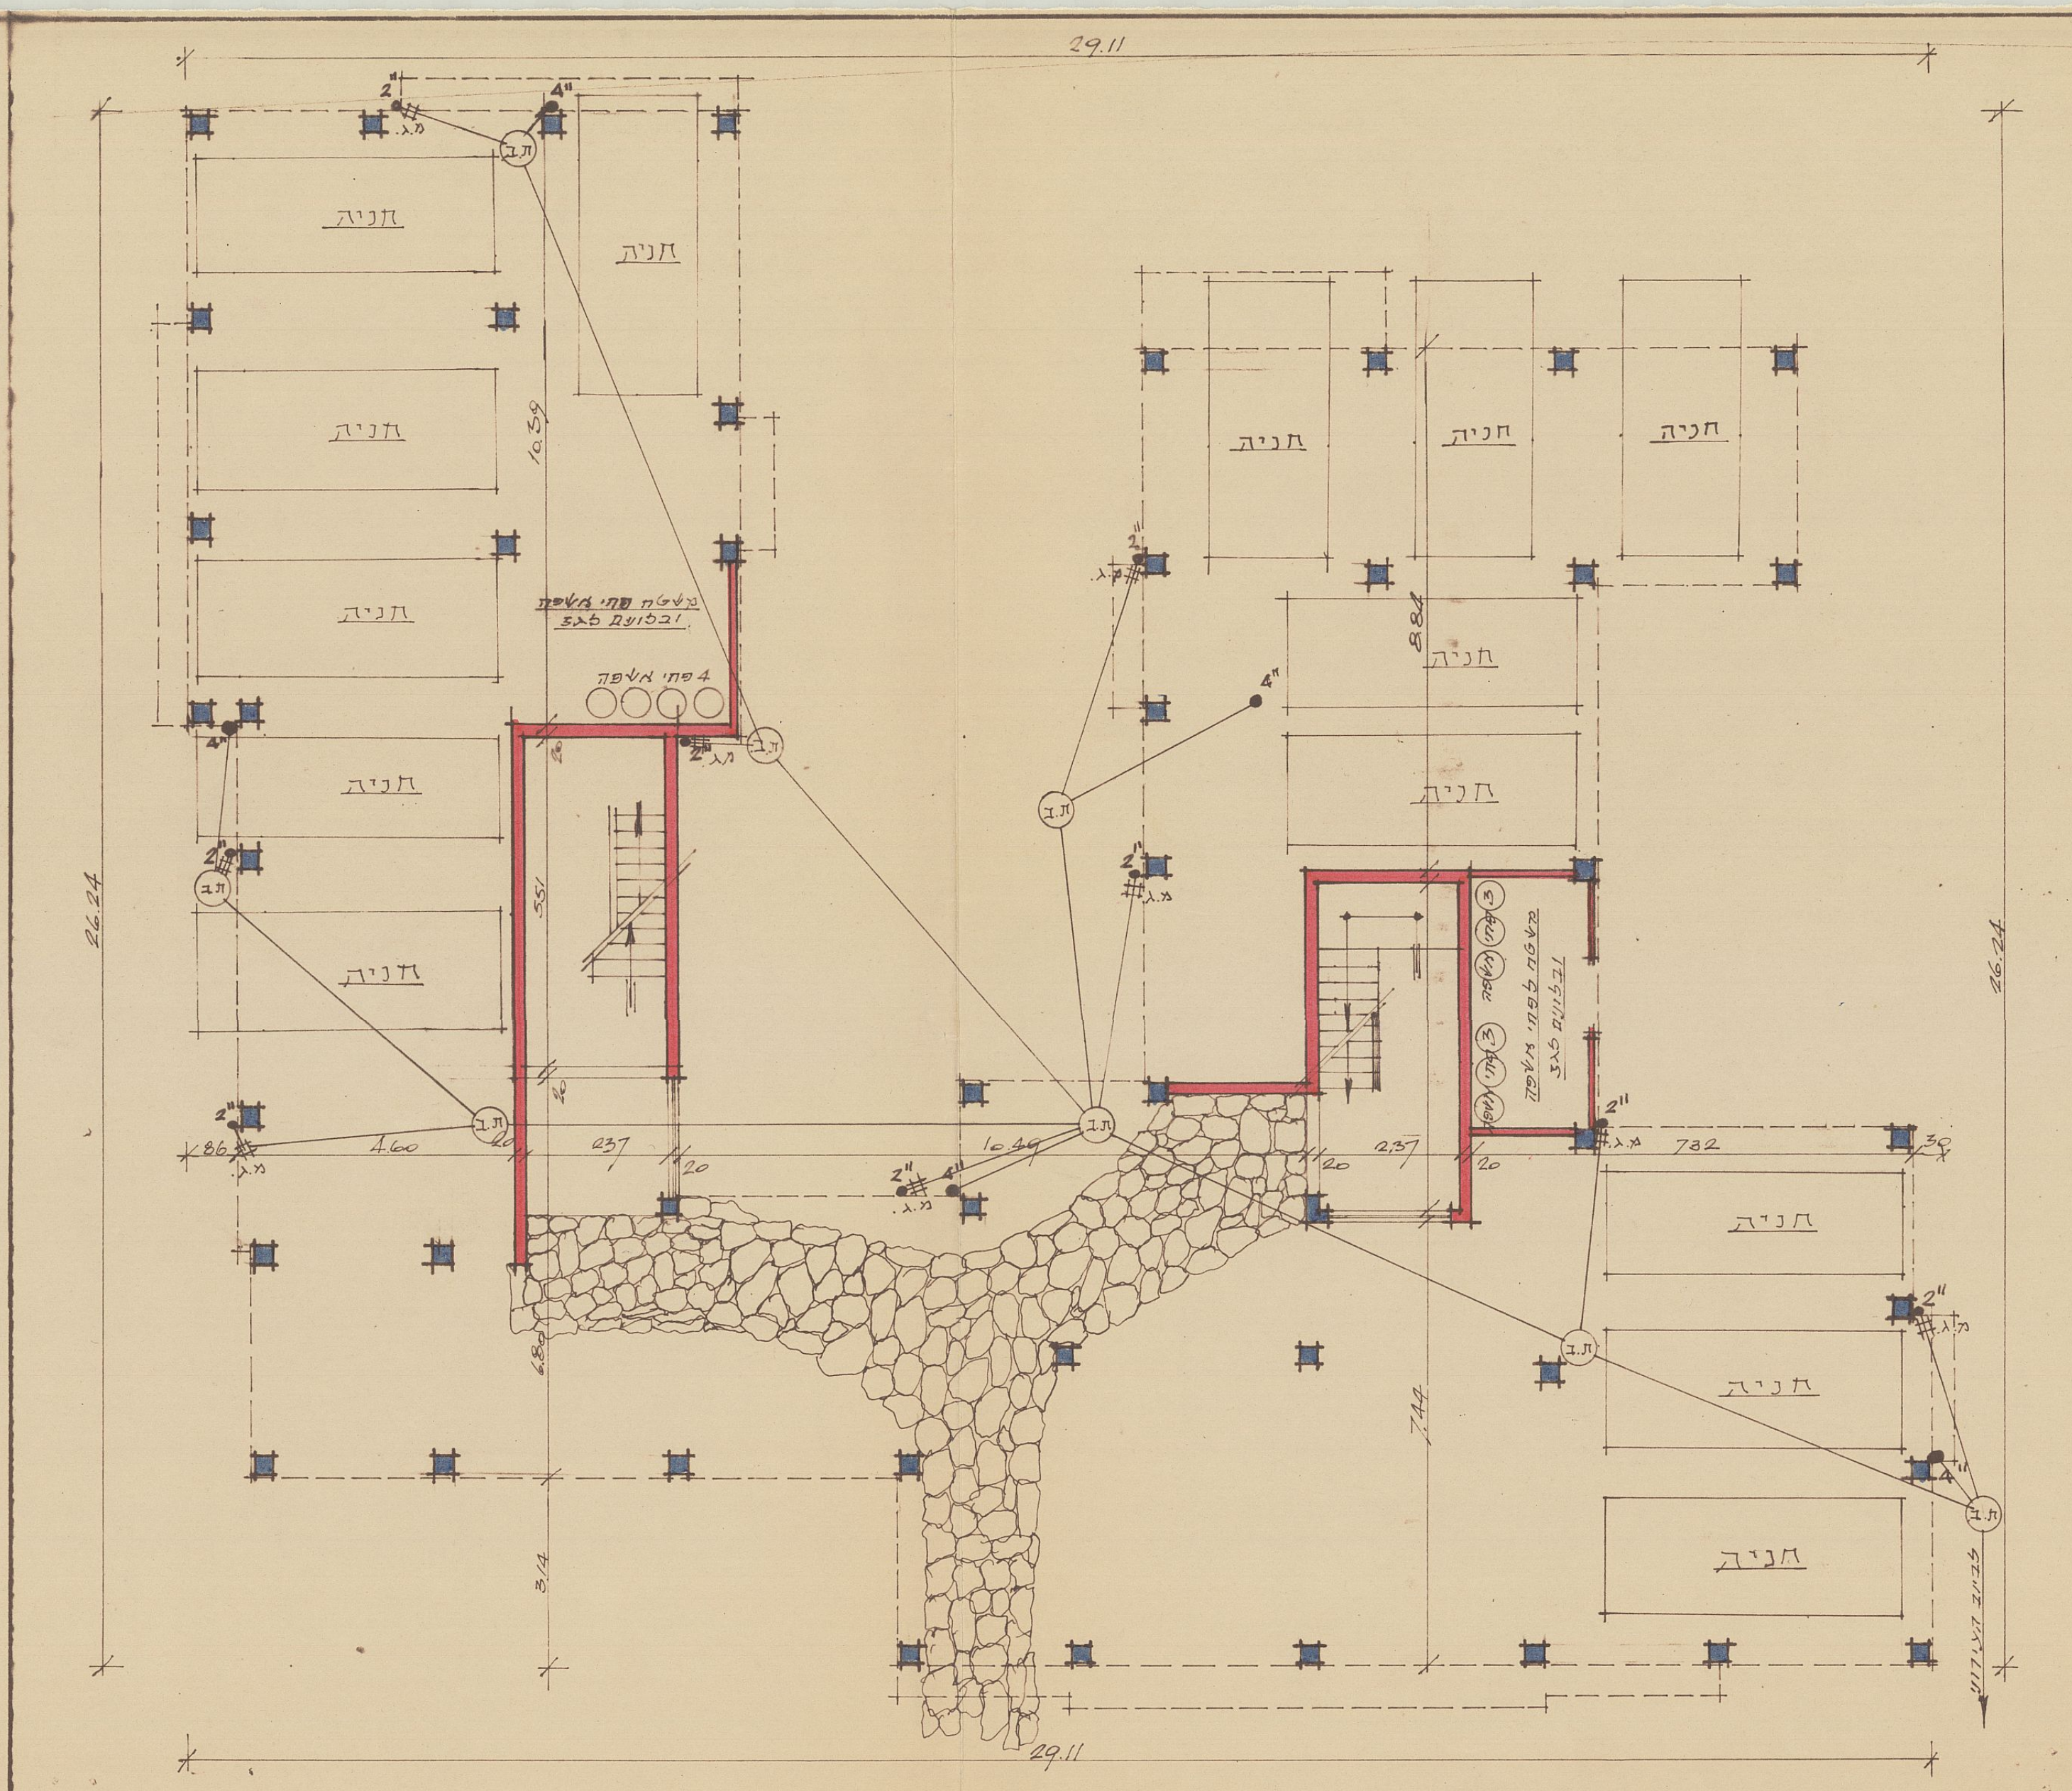

קומת הקרקע 1:100

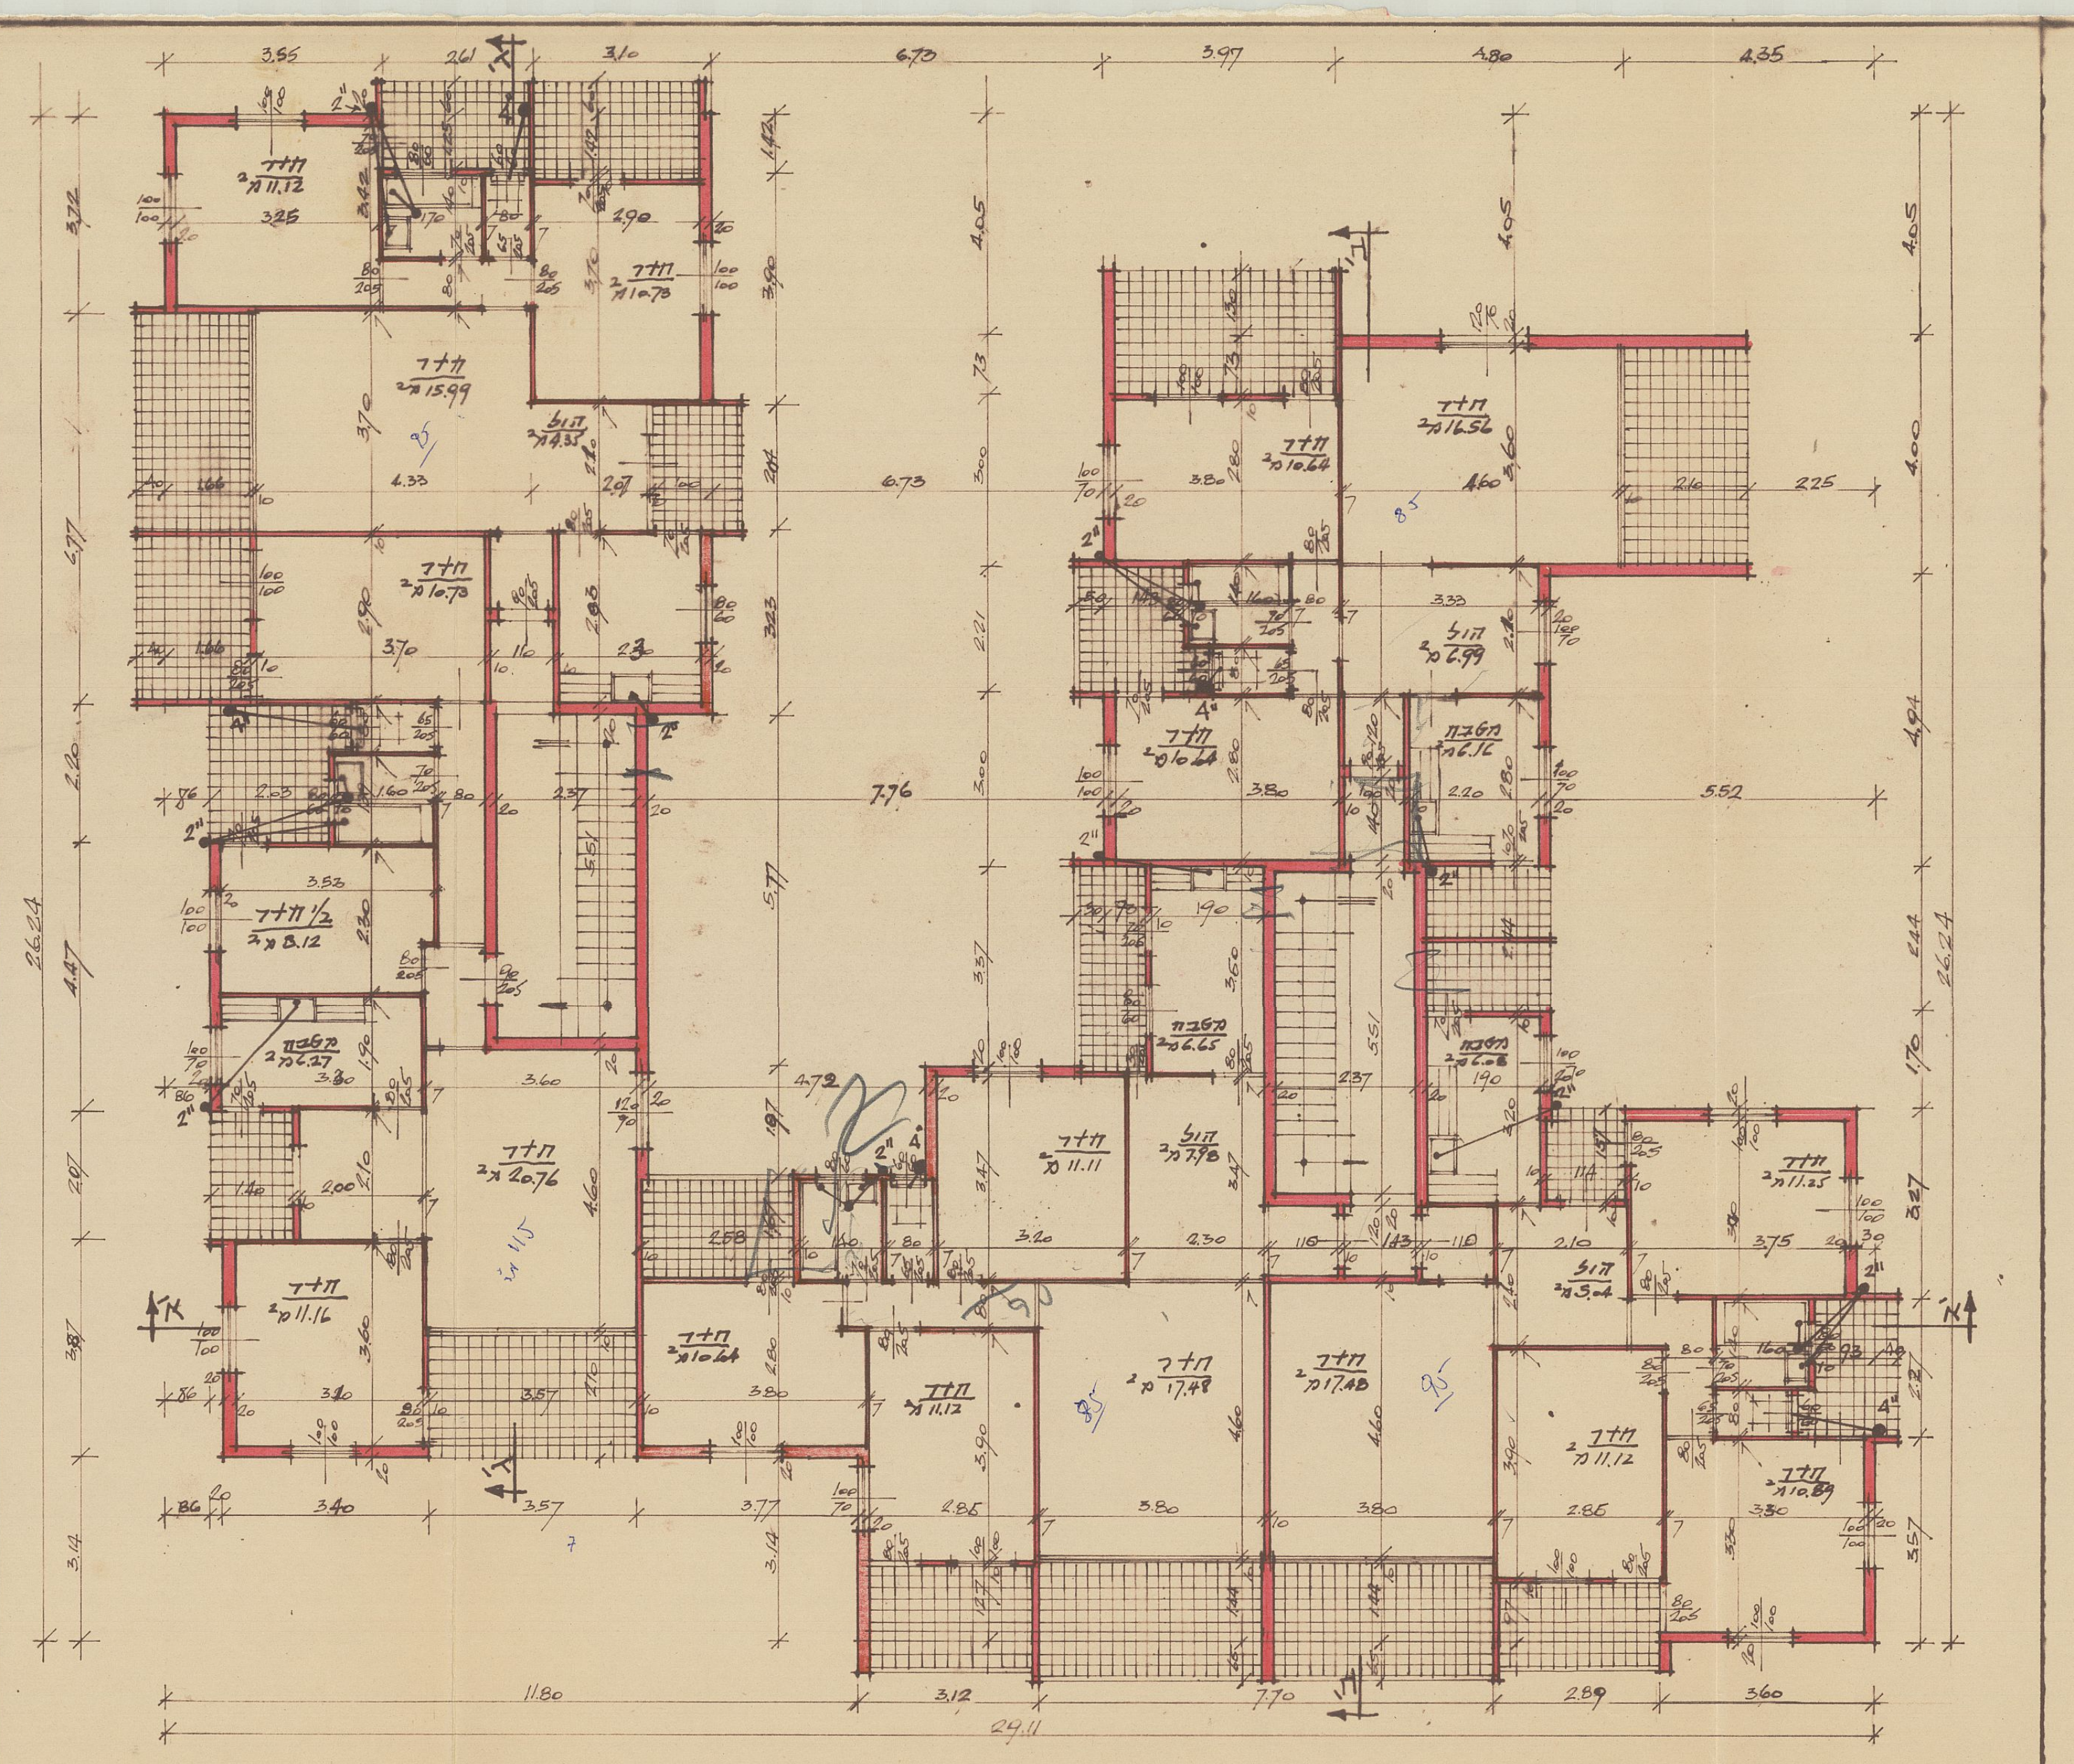

קומות א׳ב׳ג׳ 1:100

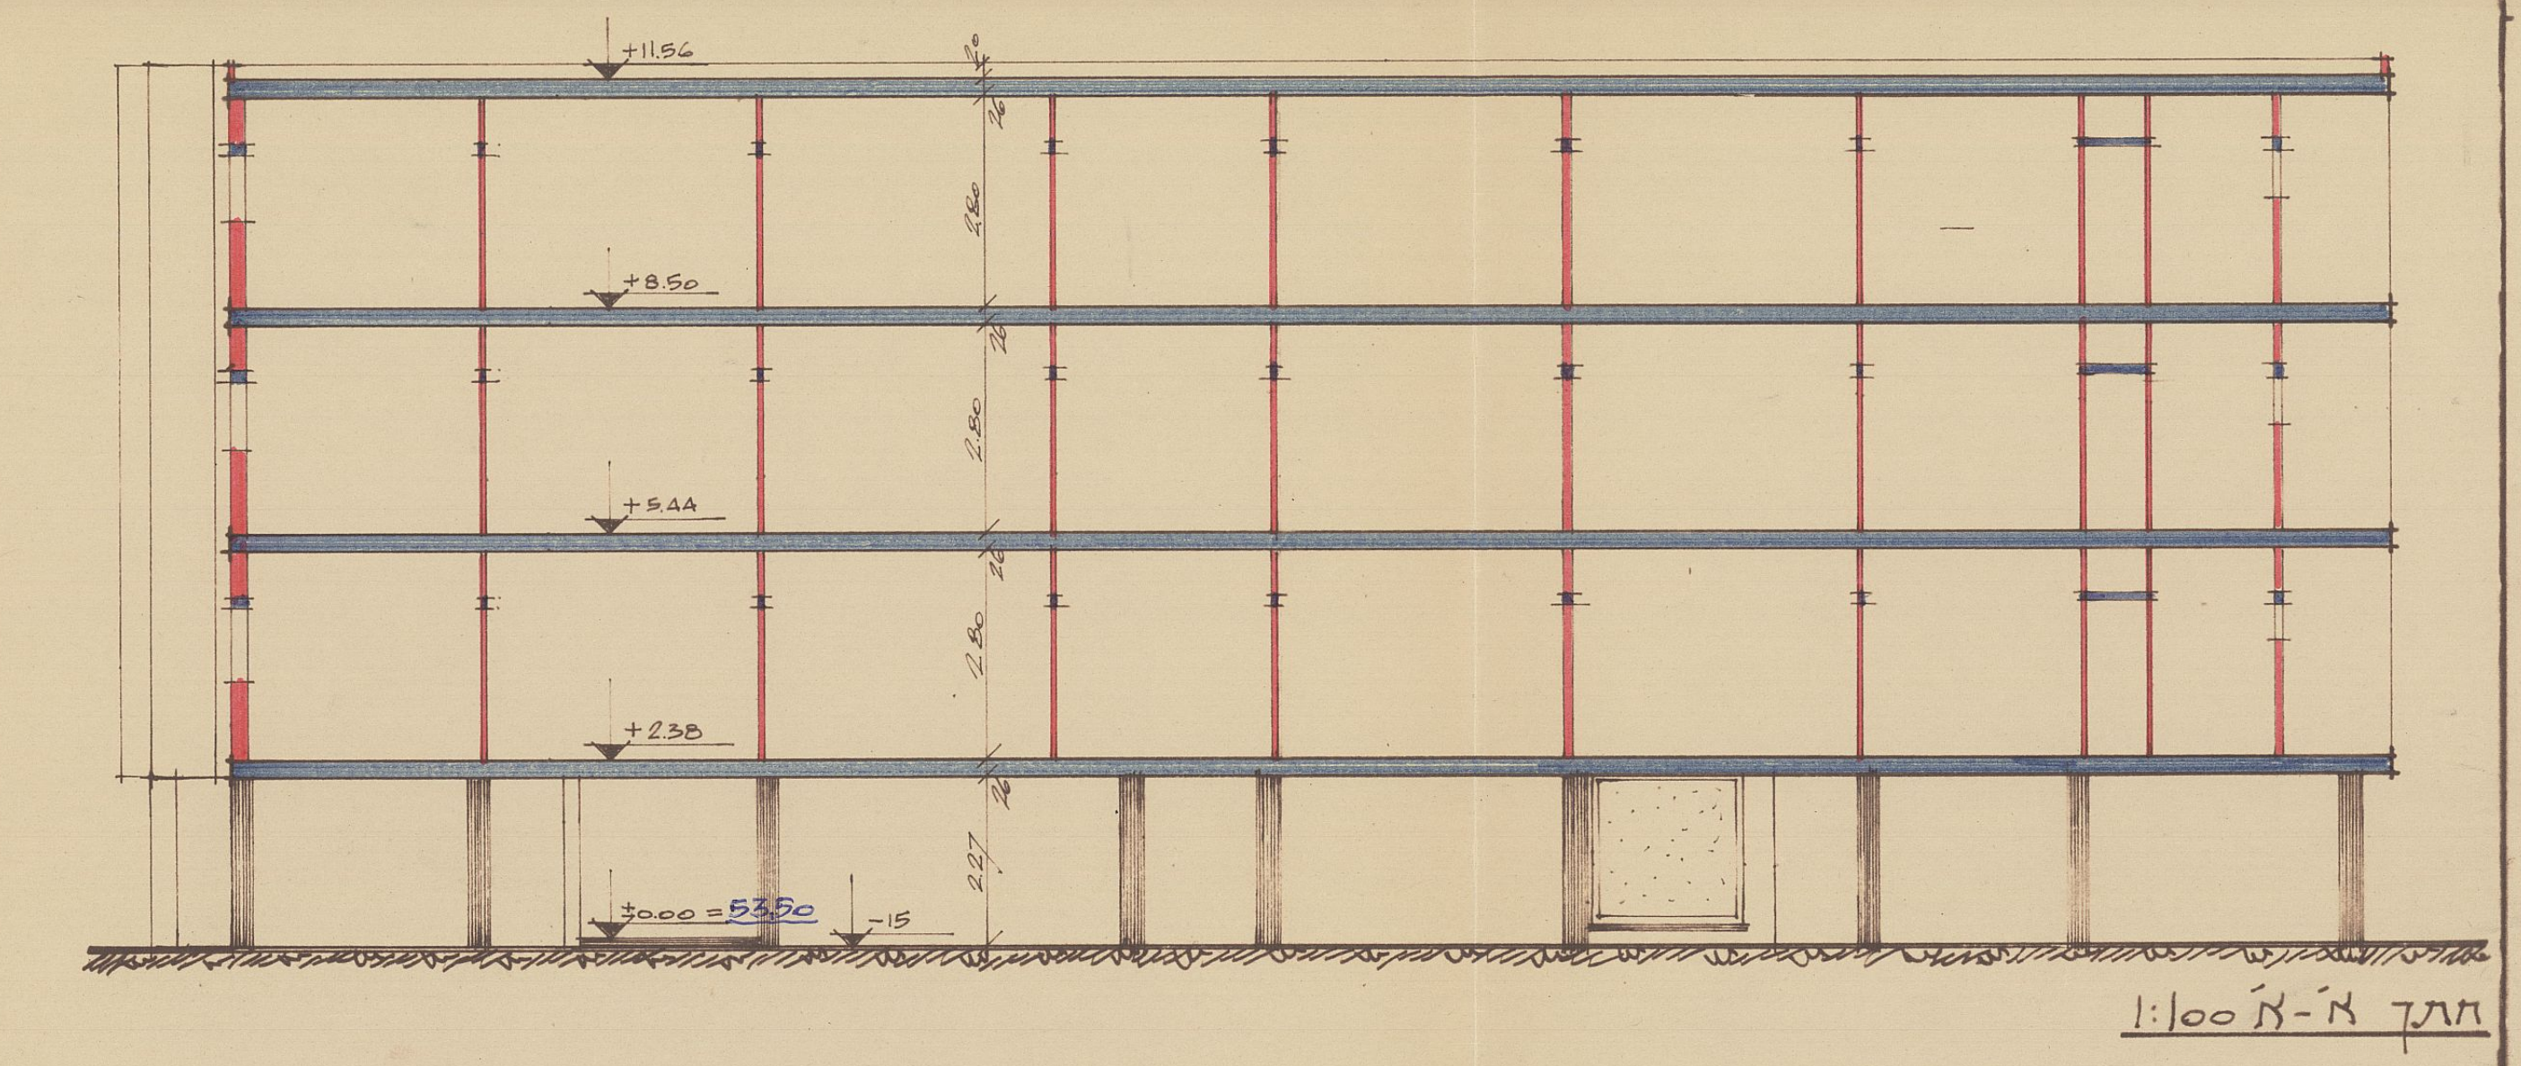

חתך א-א 1:100

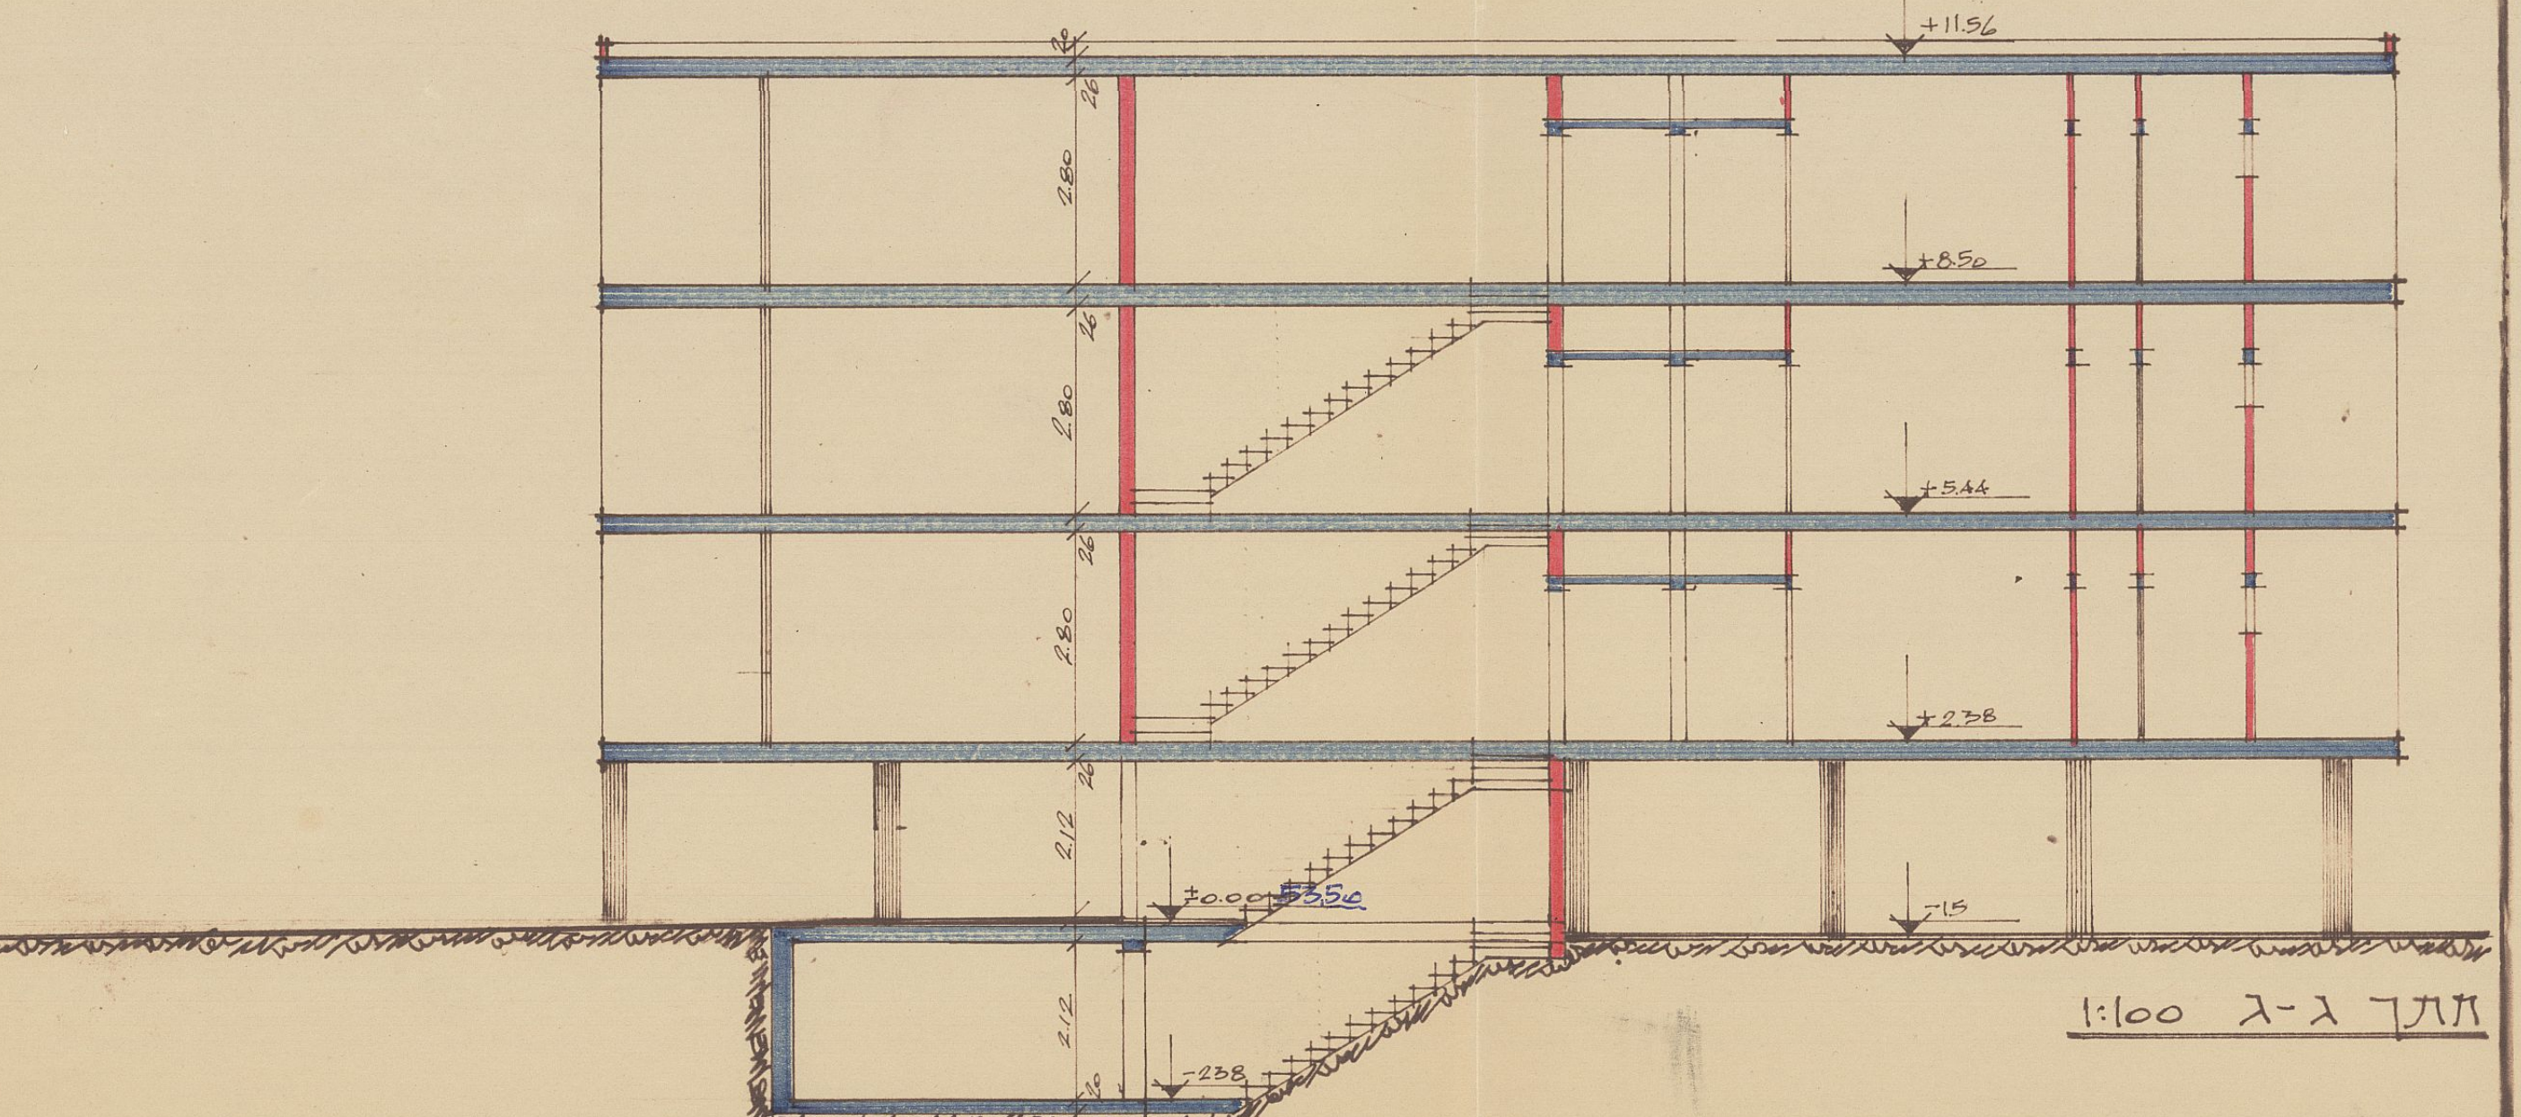

חתך ג-ג 1:100

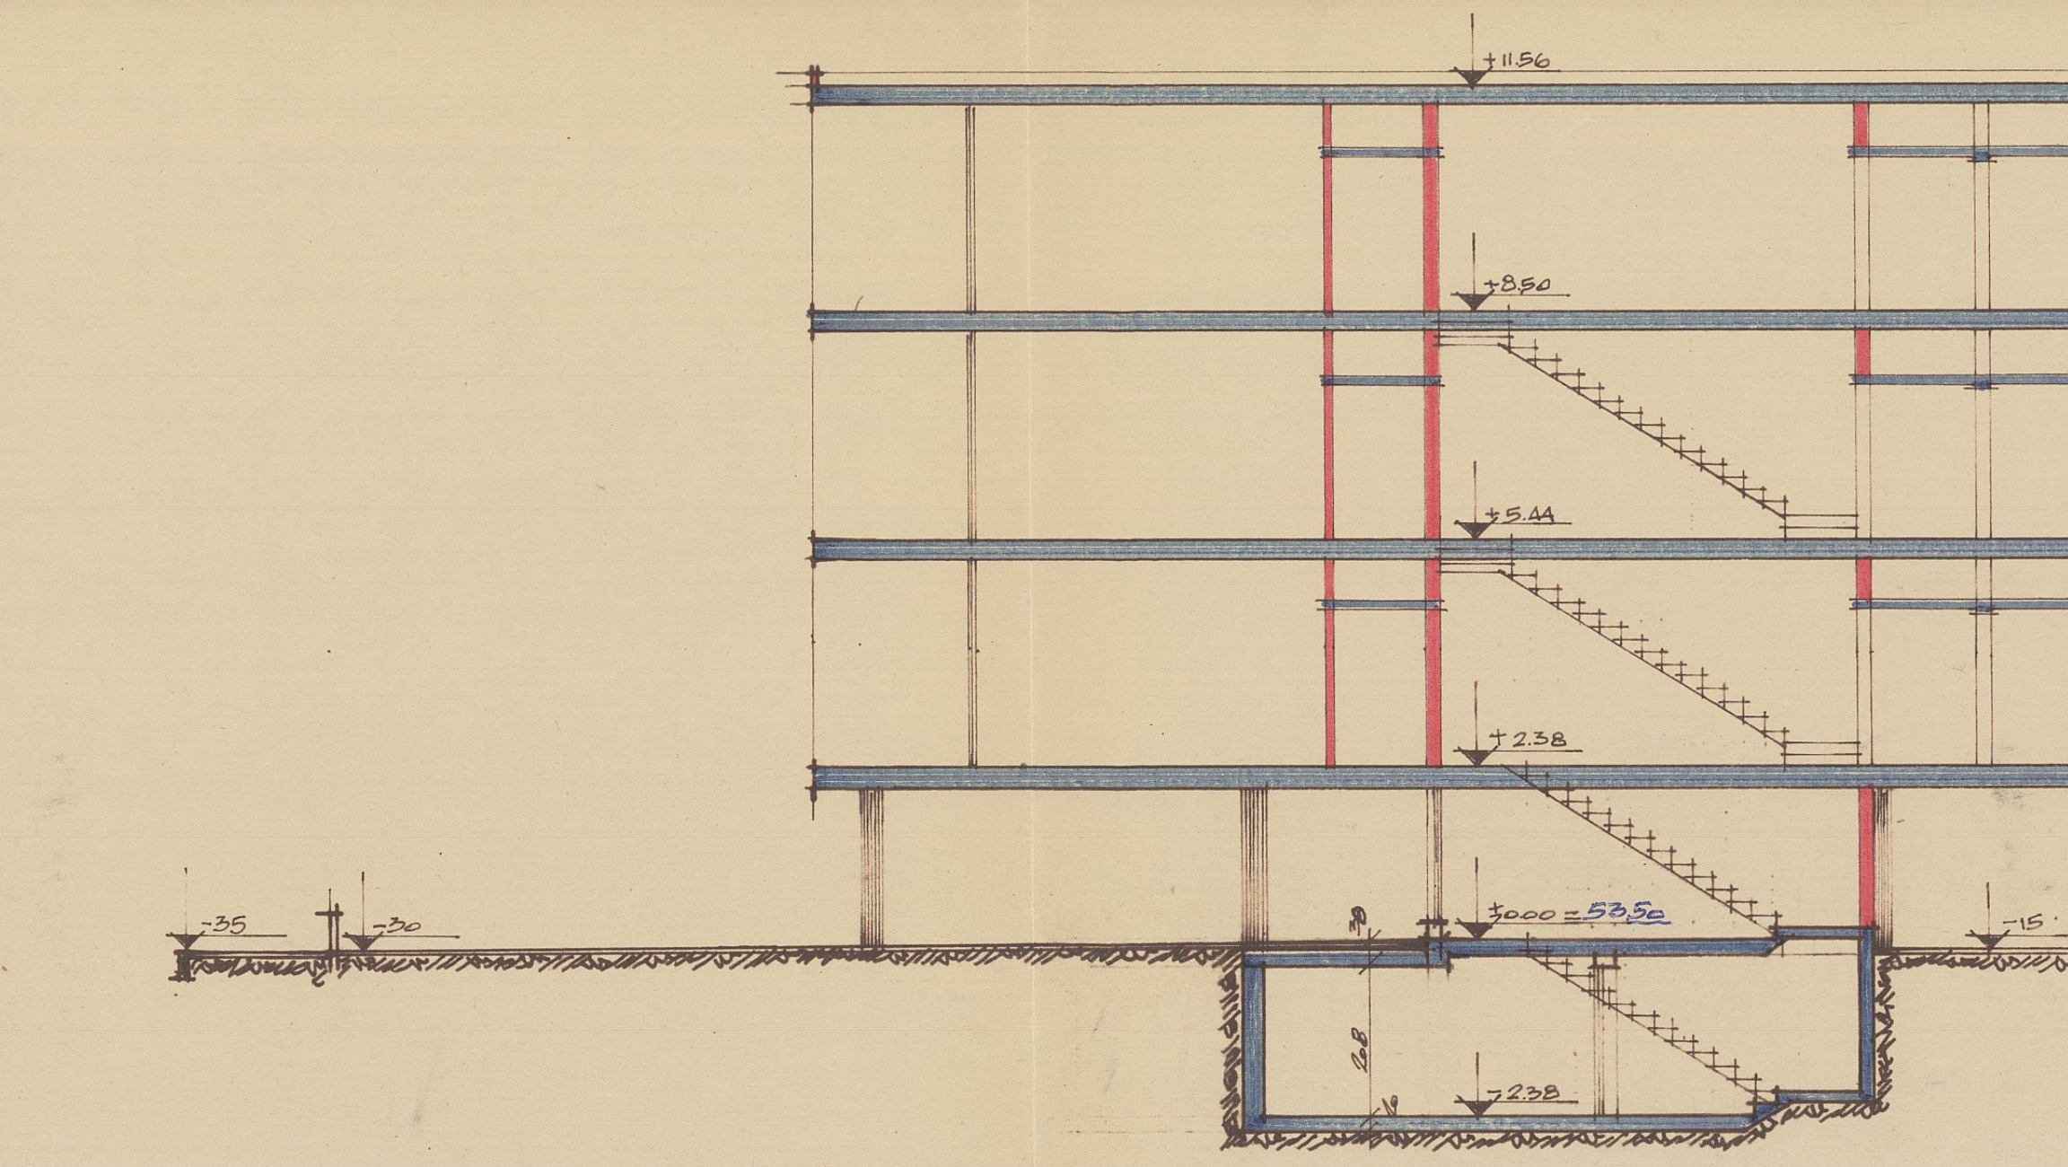

חתך ב-ב 1:100

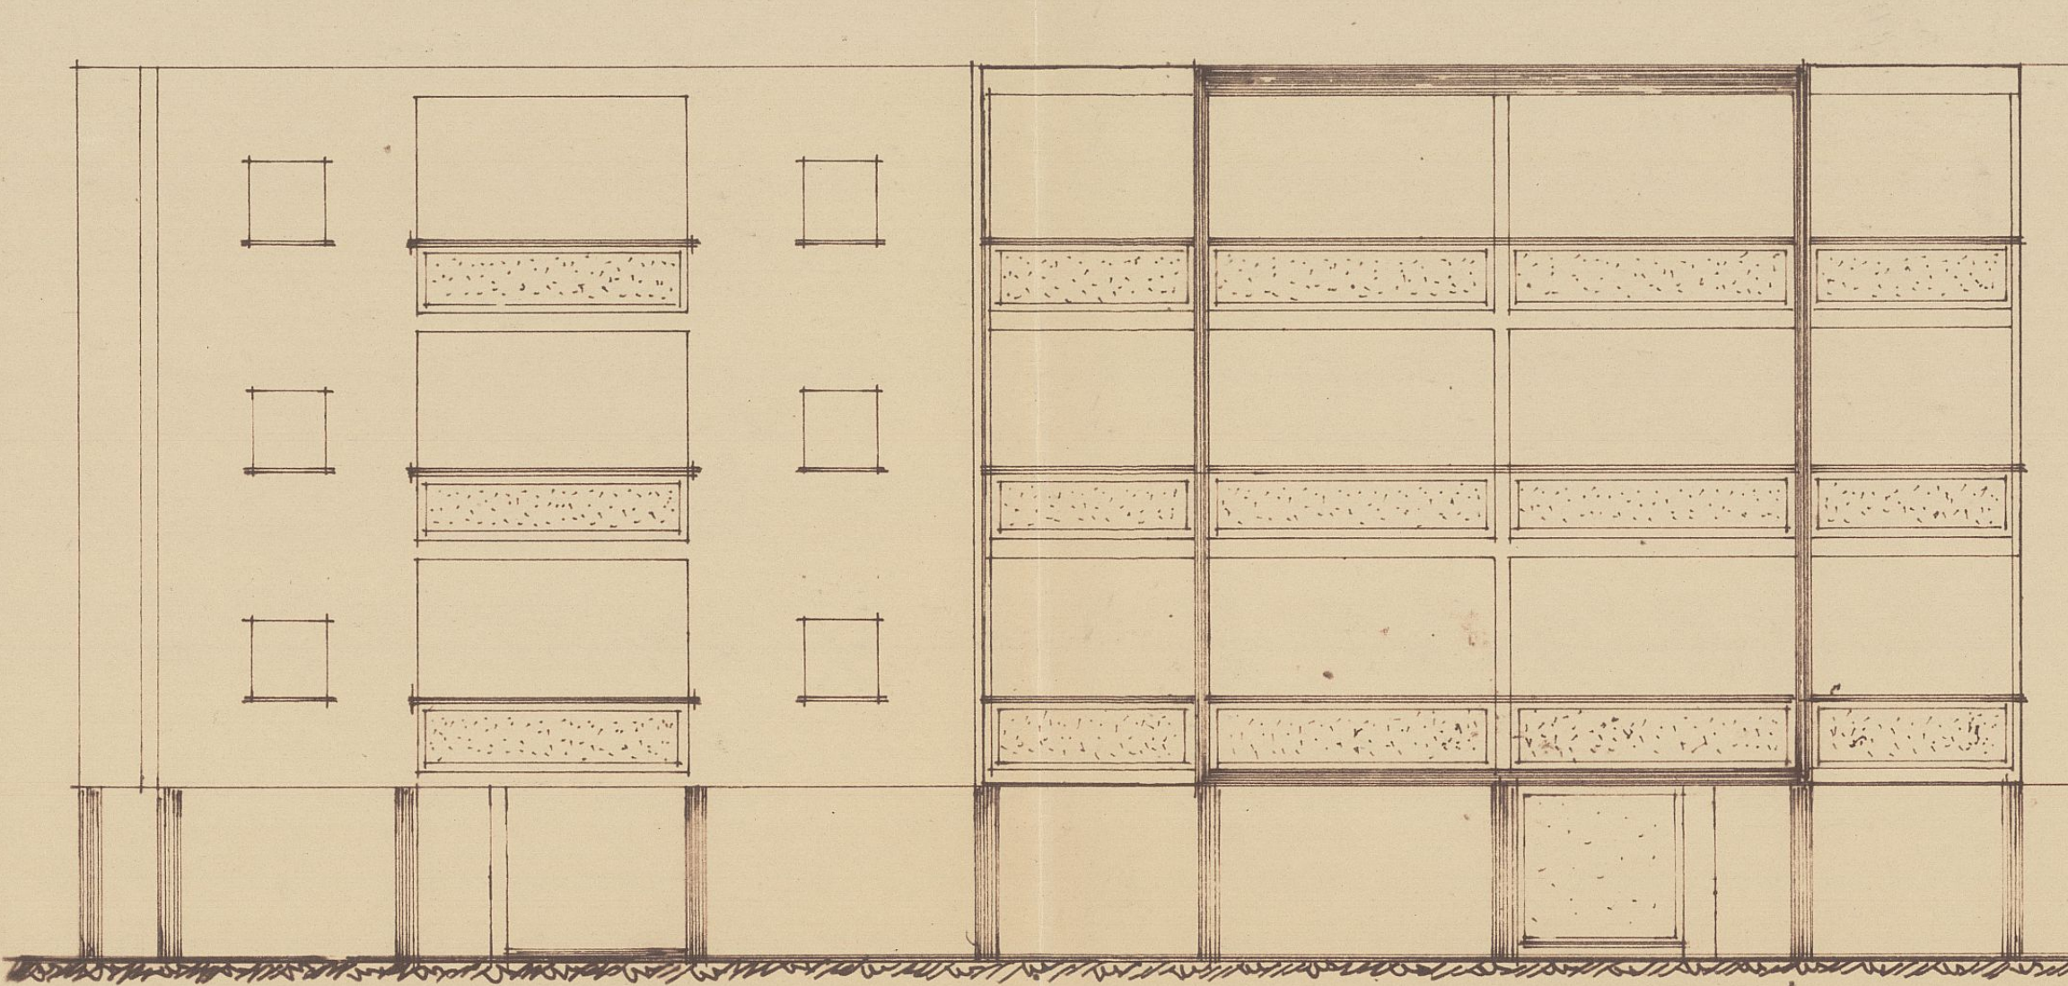

חזית לרחוב 1:100

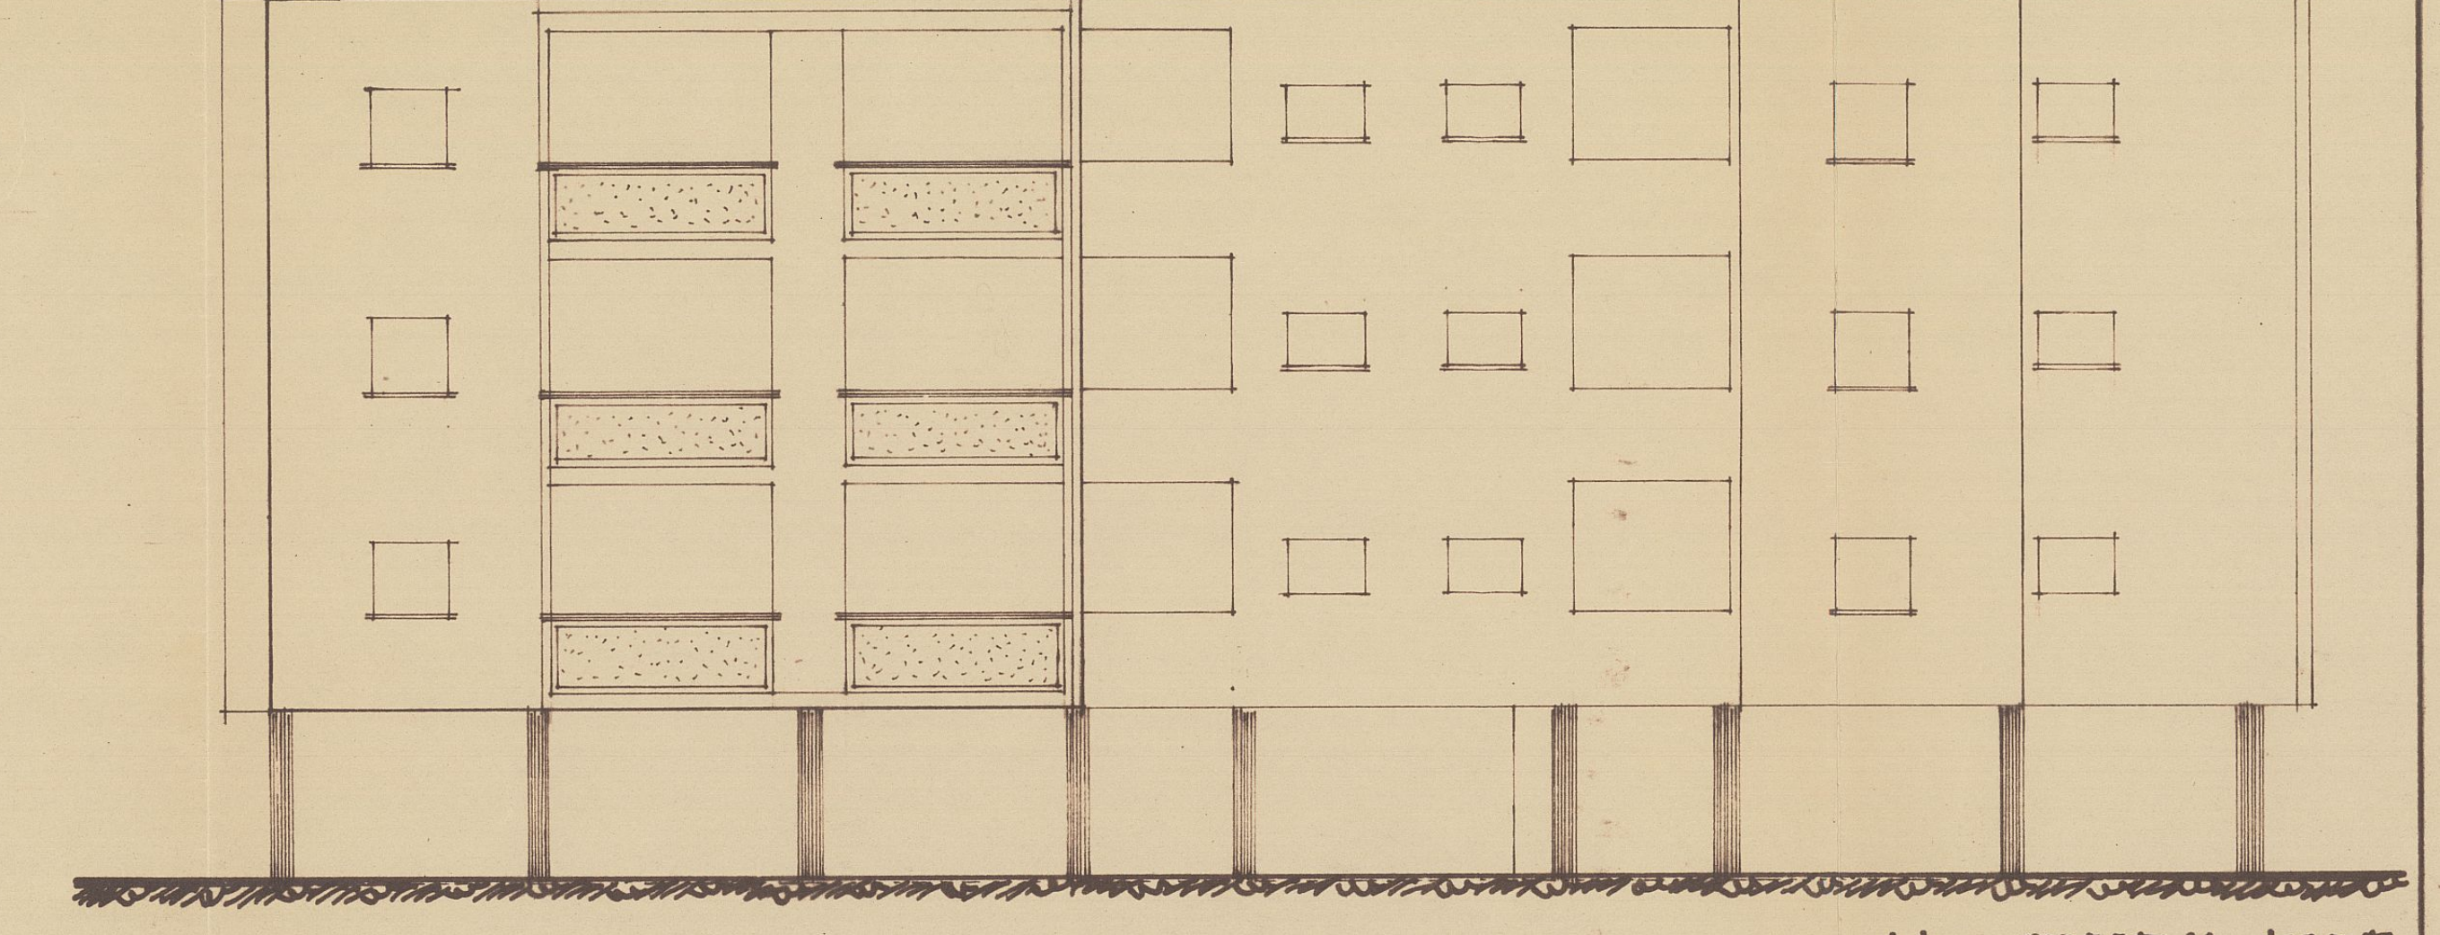

חזית צפונית 1:100

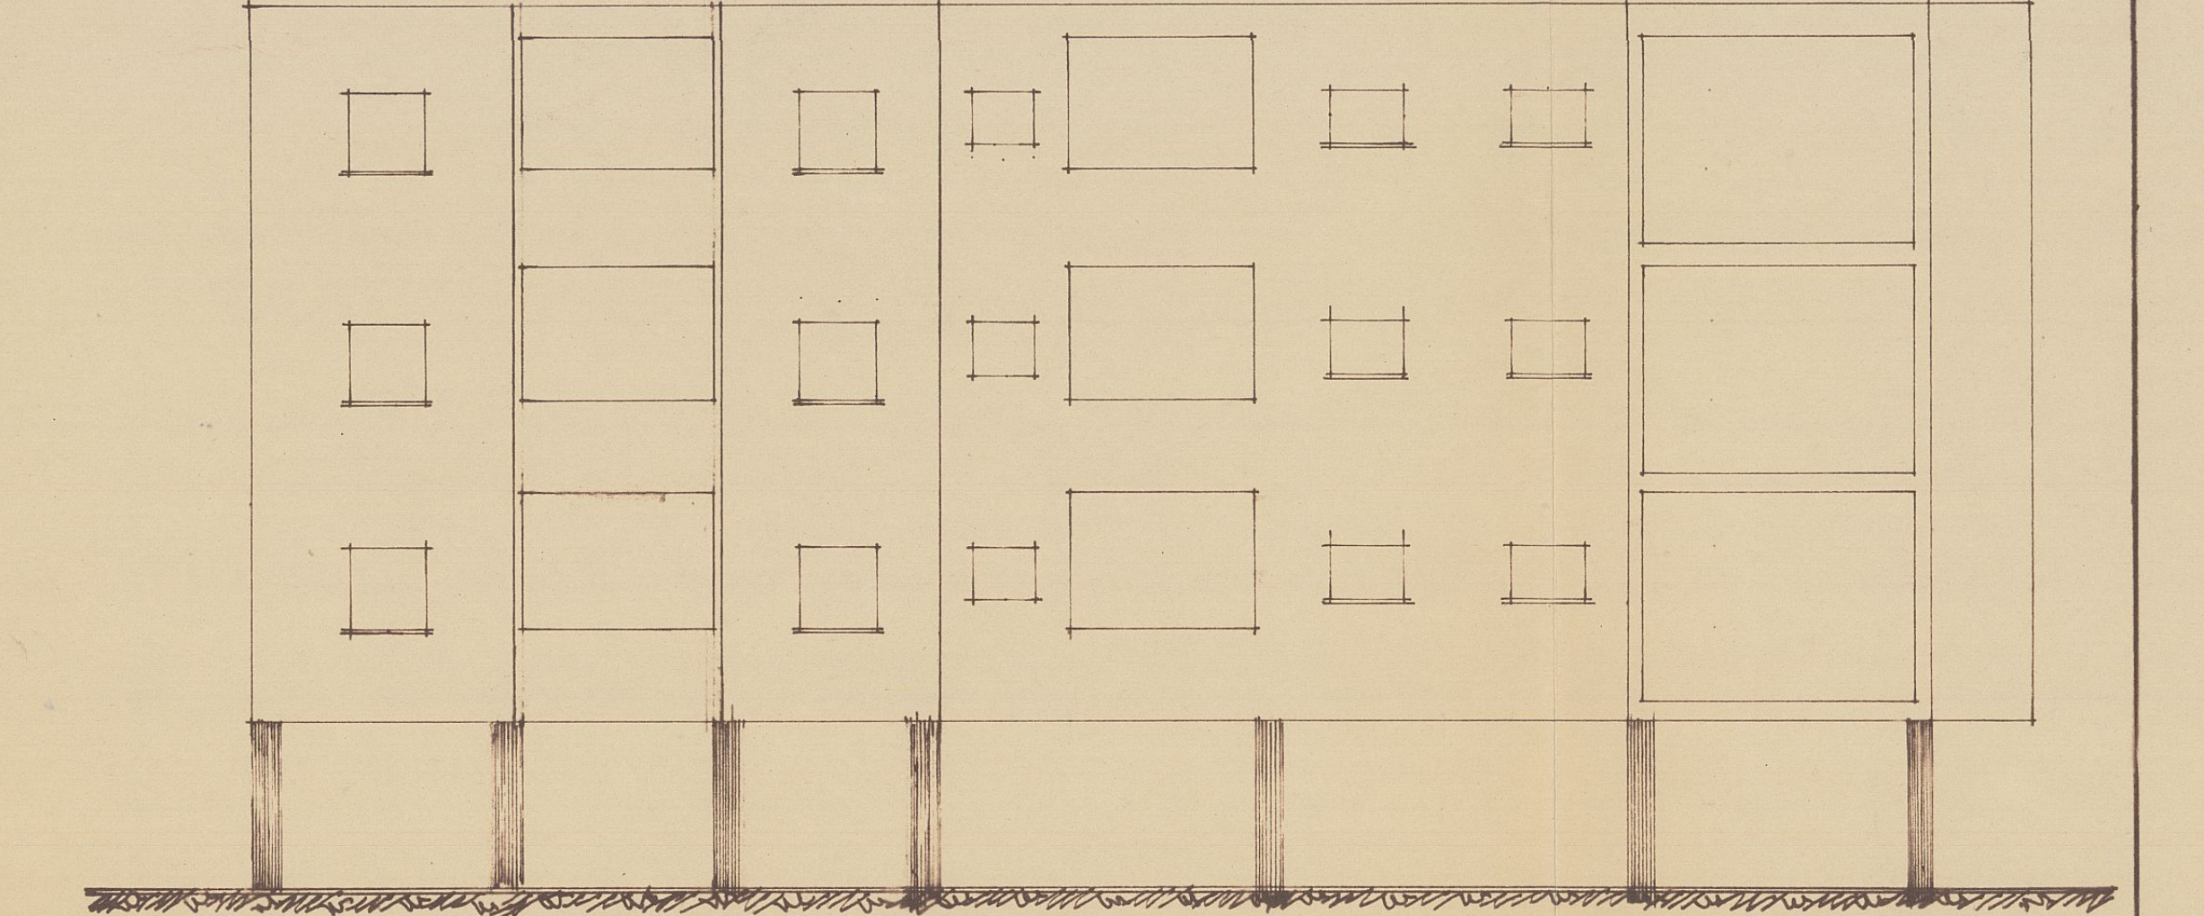

חזית דרומית 1:100

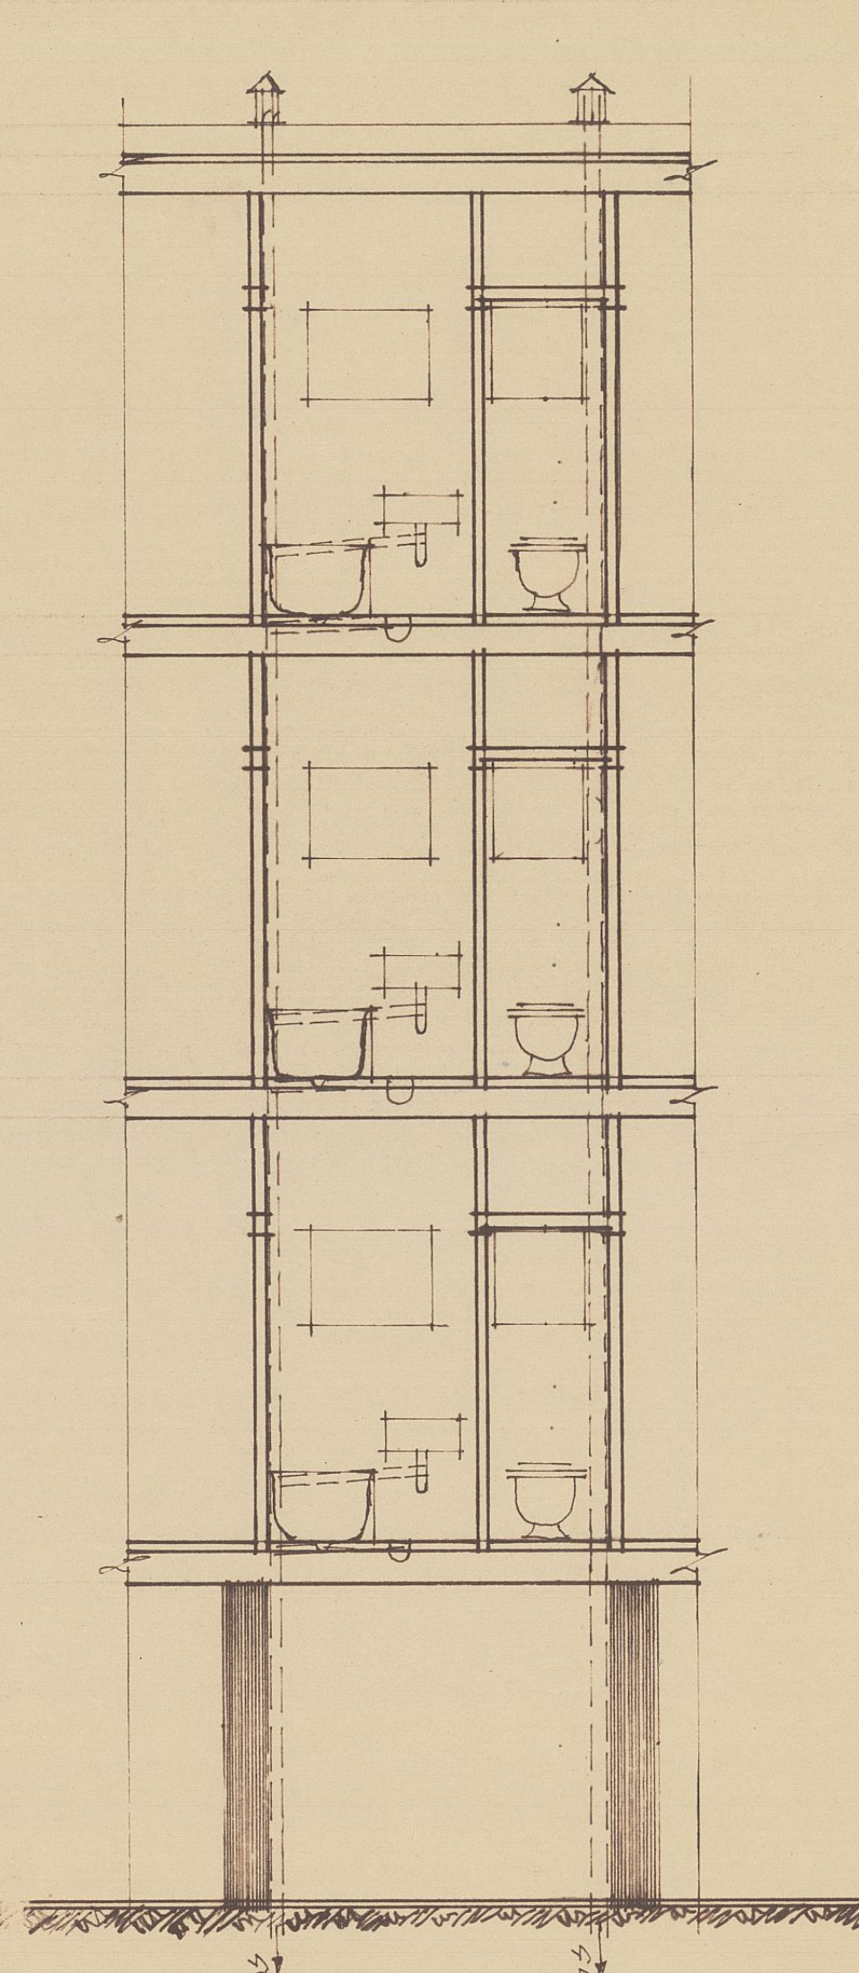

חתך סניטרי טיפוסי דרך הנוחיות
1:50

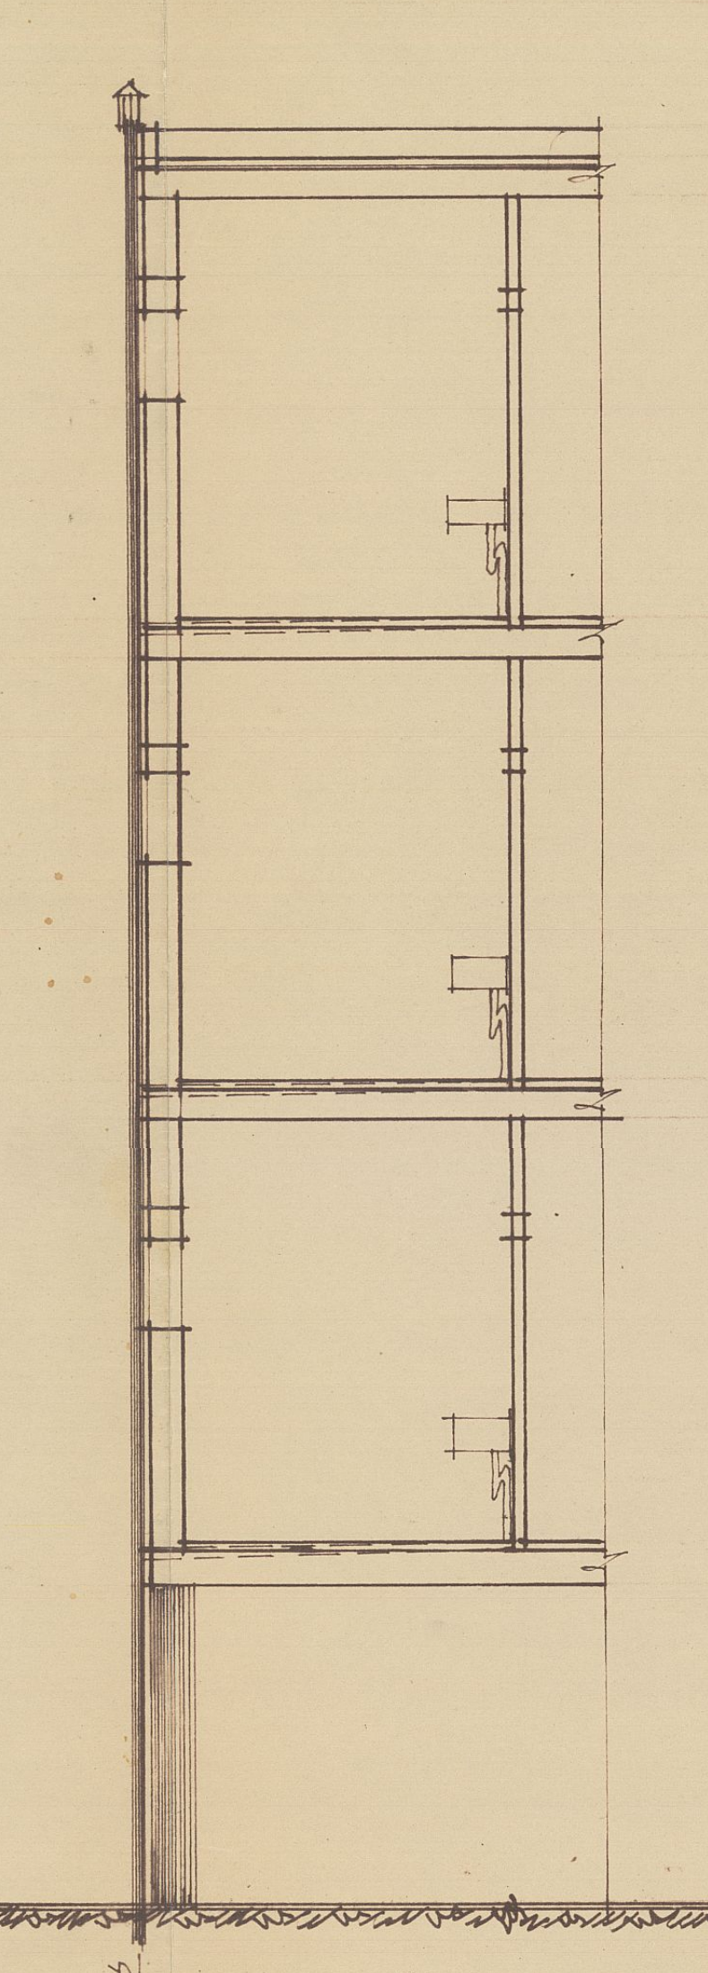

חתך סניטרי טיפוסי דרך המטבחים
1:50