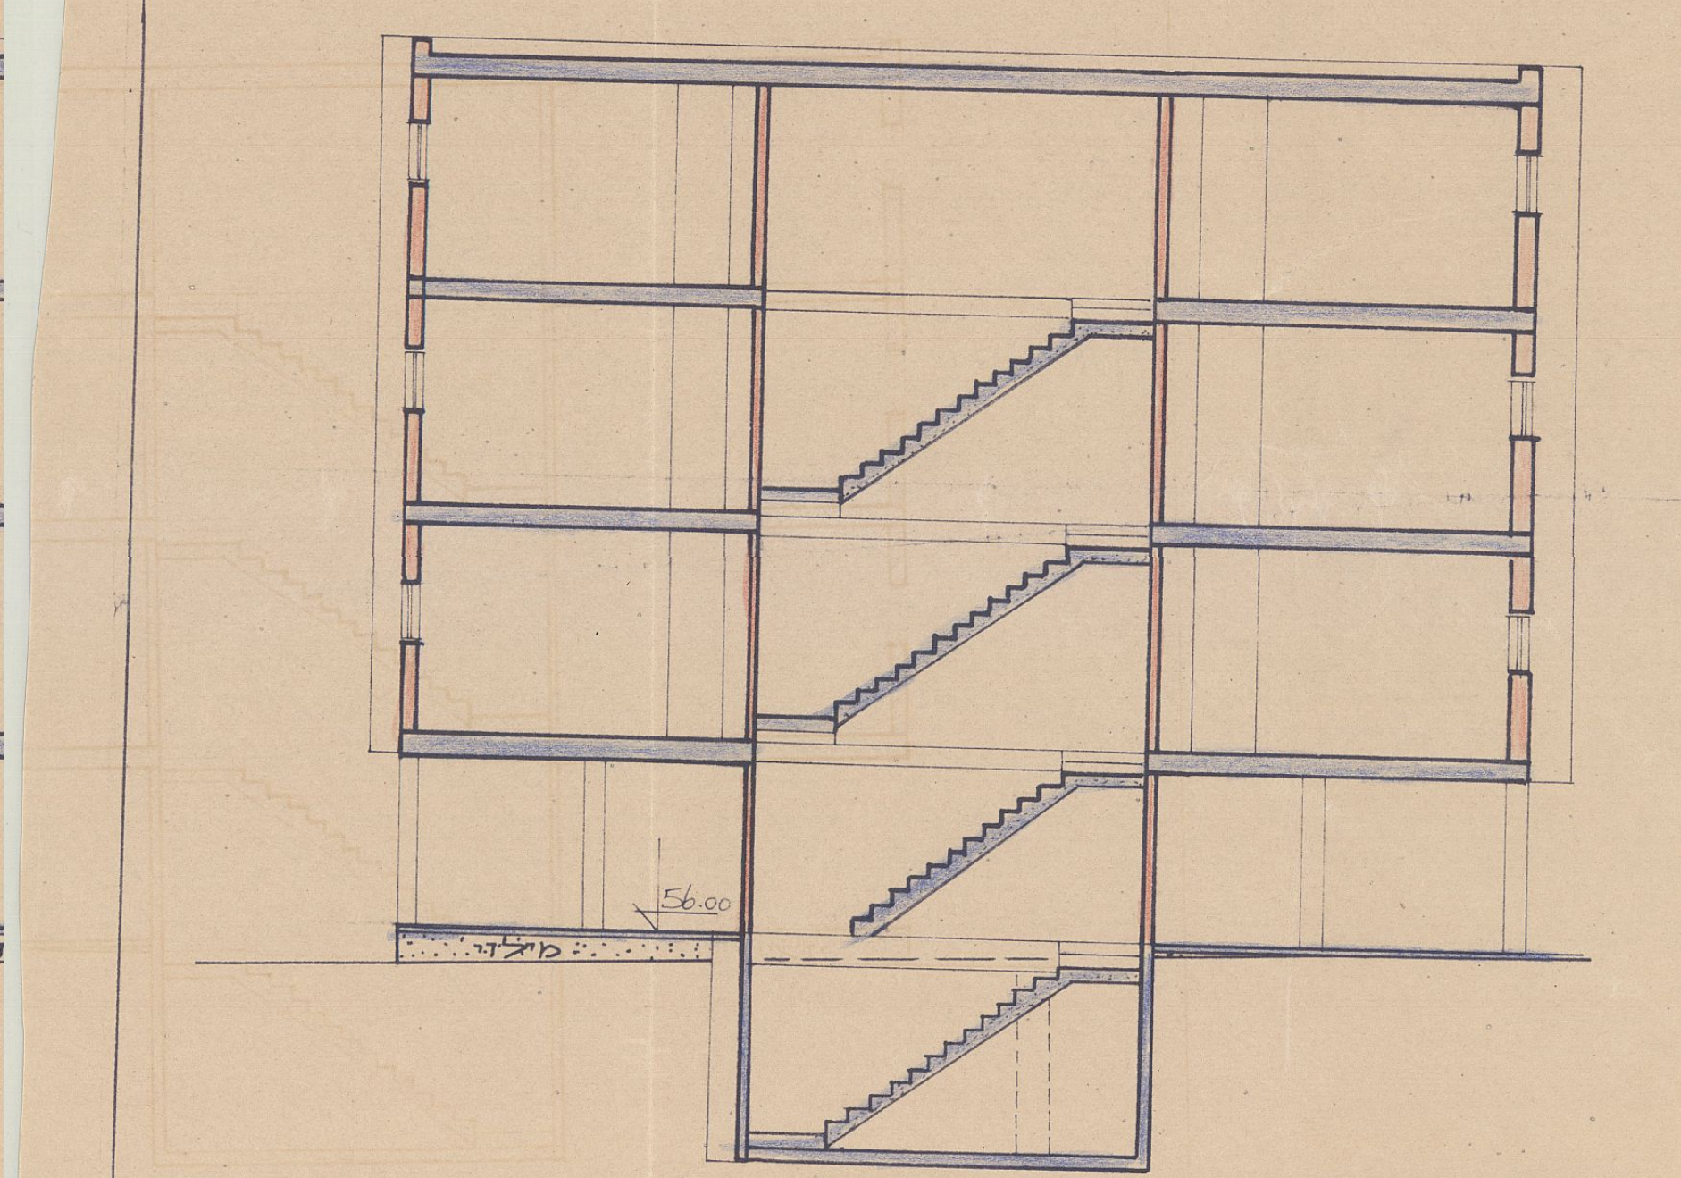

חתך א-א 1:100

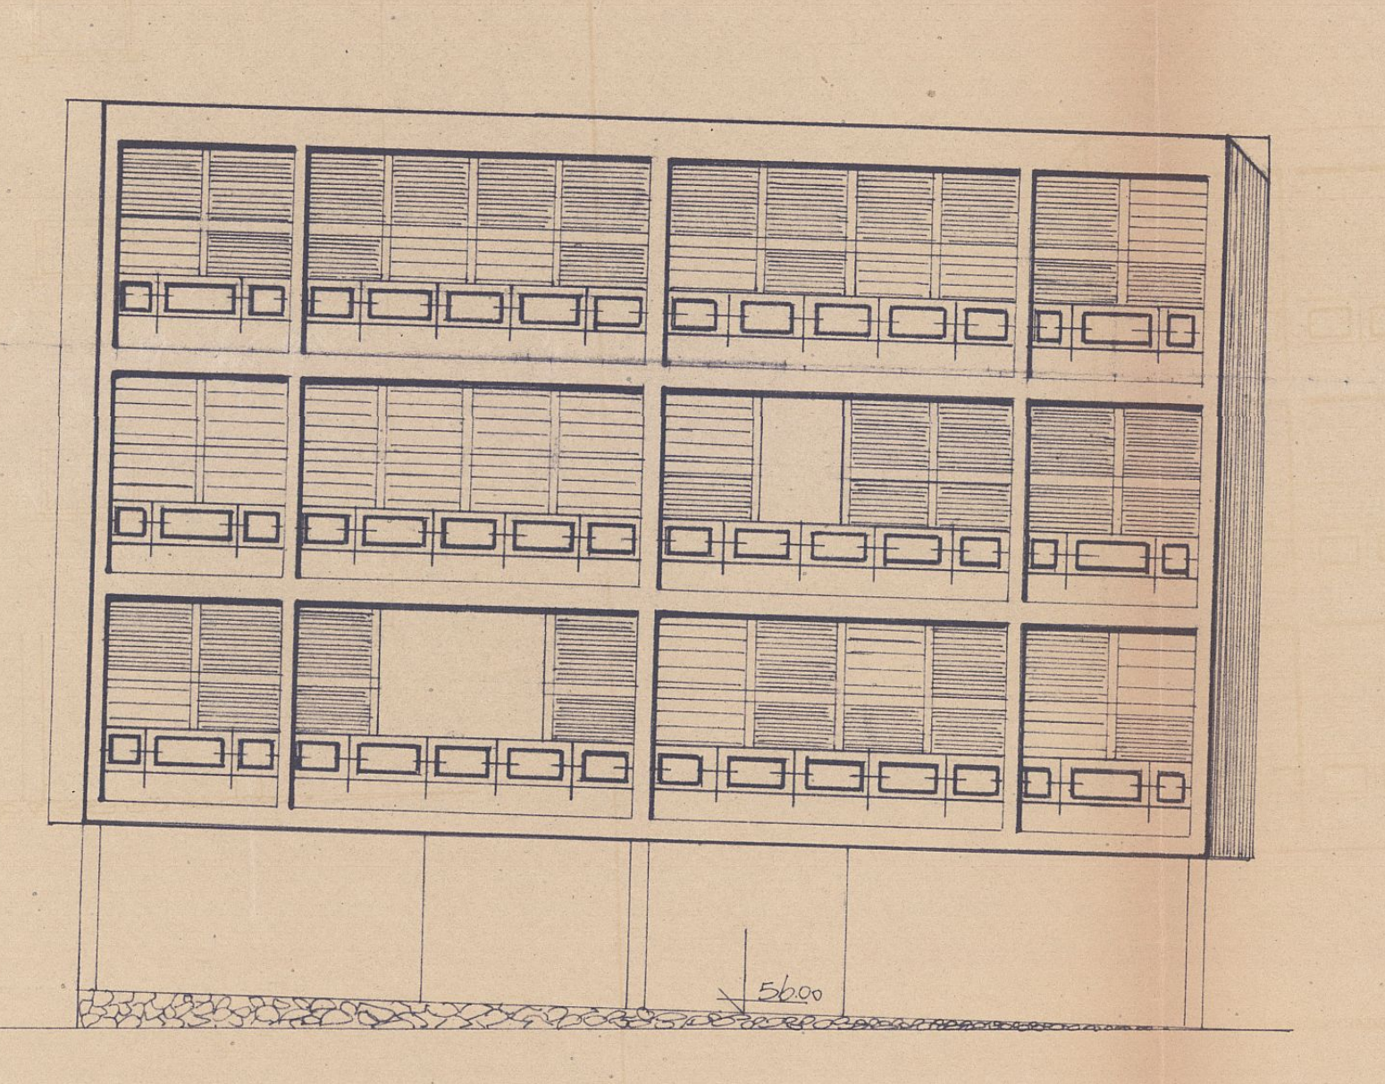

חזית דרומית

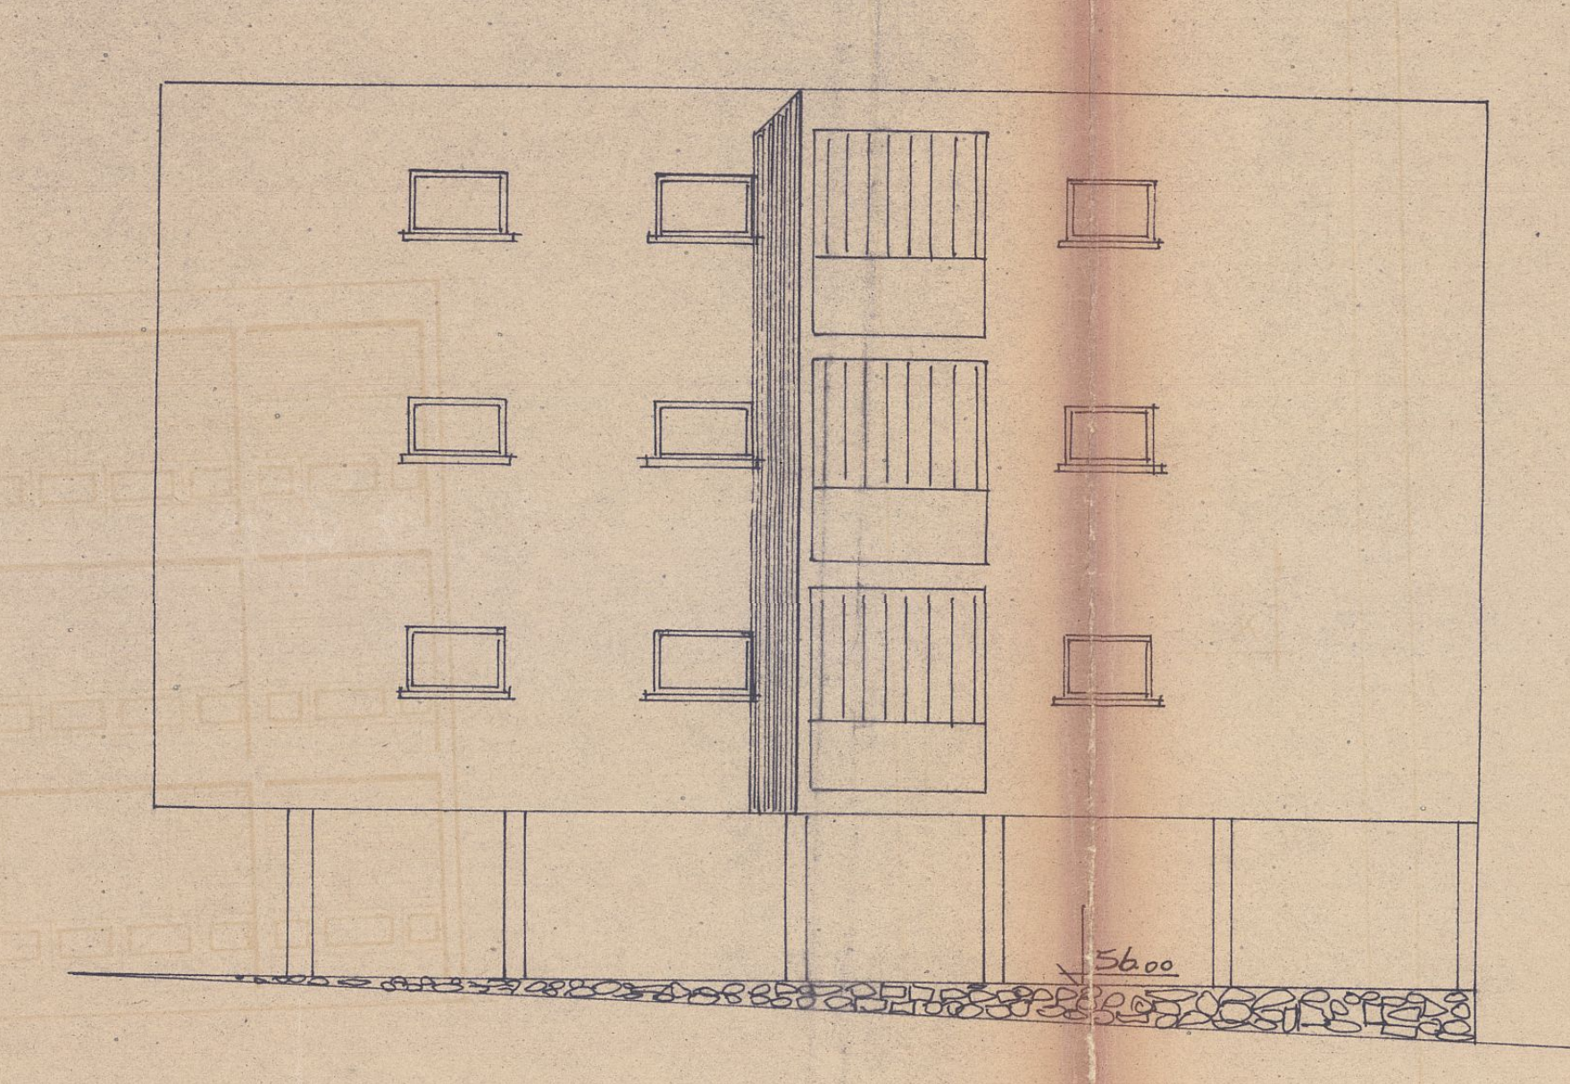

חזית מערבית זהה למזרחית 1:100

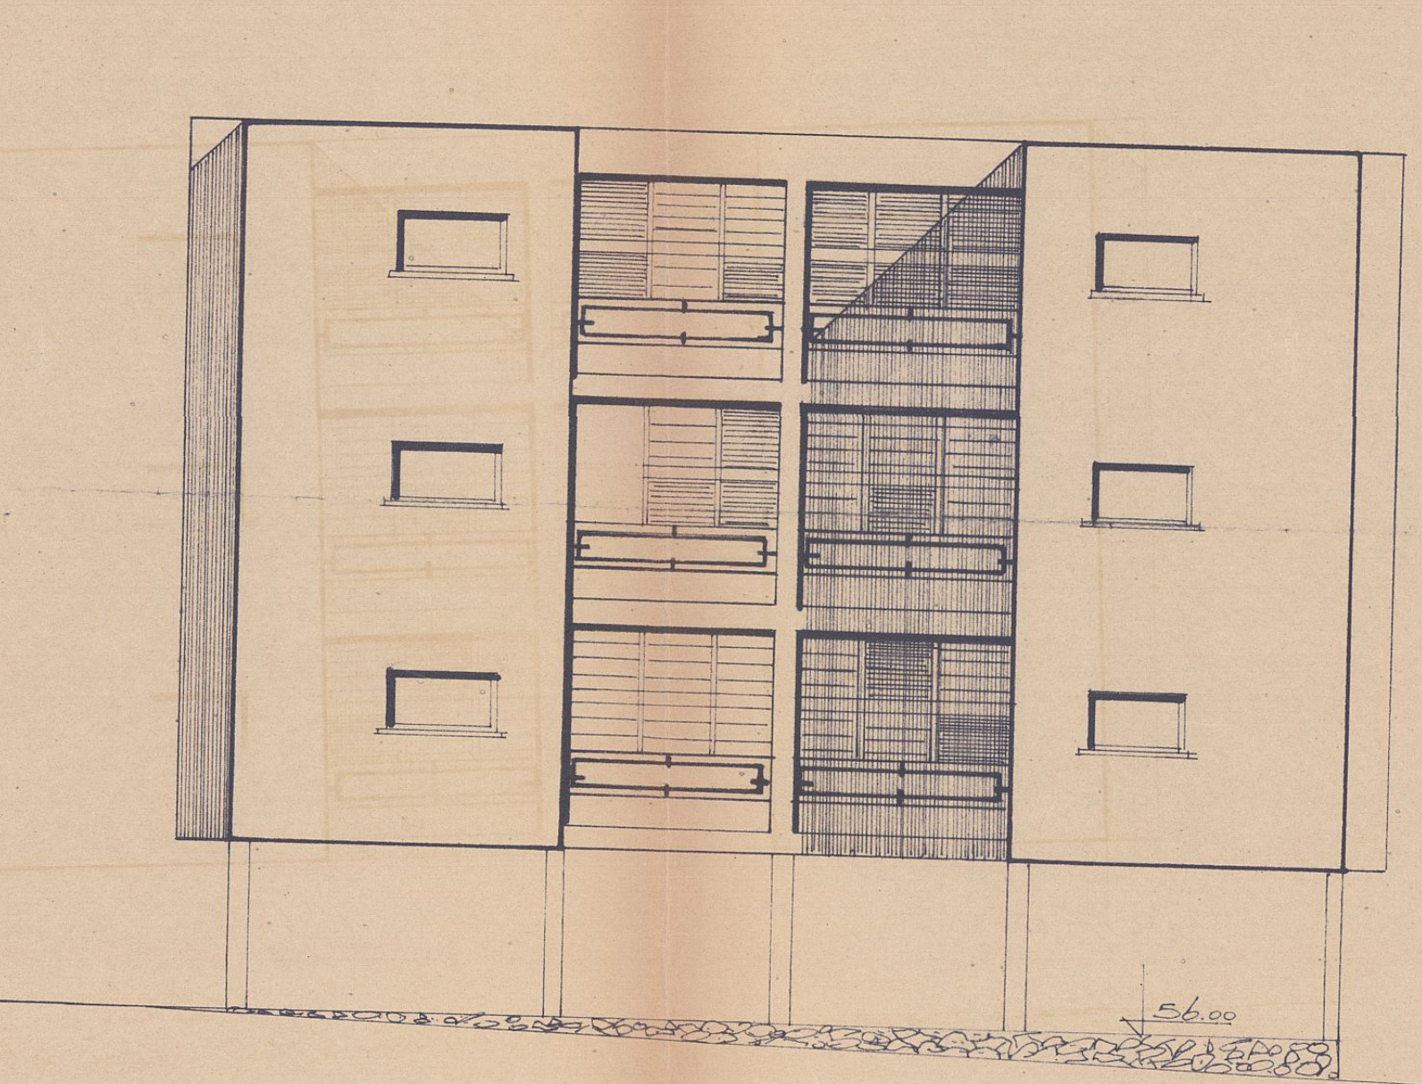

חזית צפונית 1:100

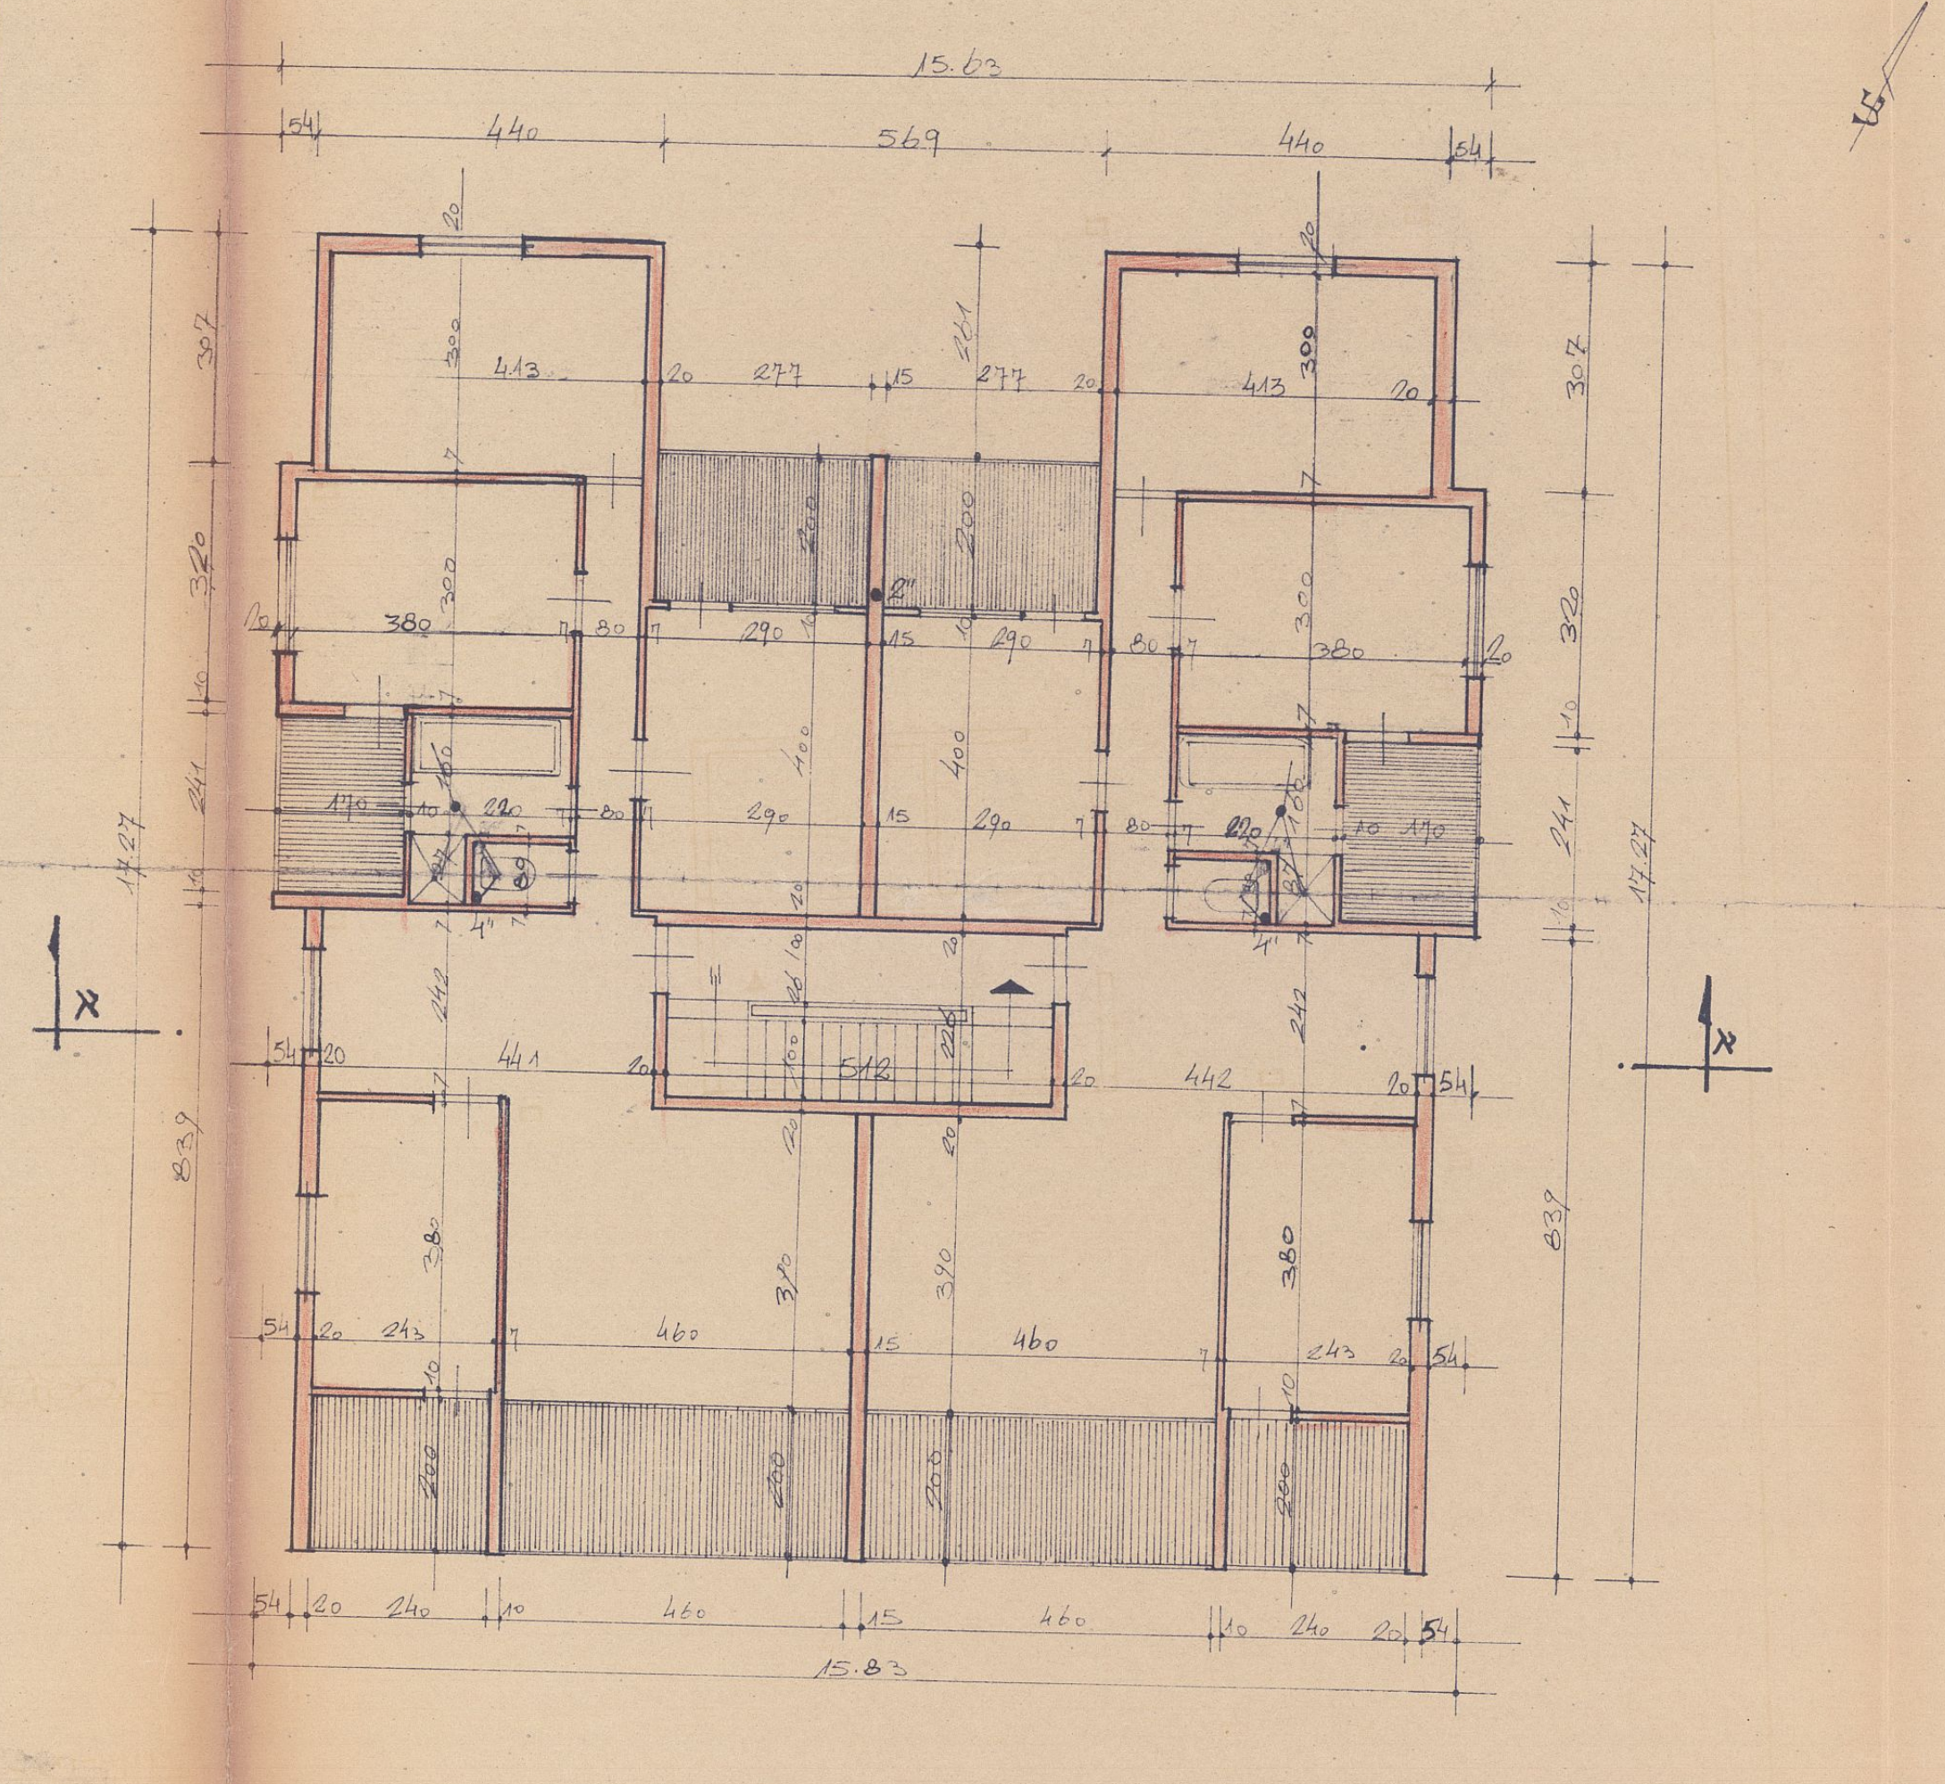

תכנית קומה טיפוסית 1:100

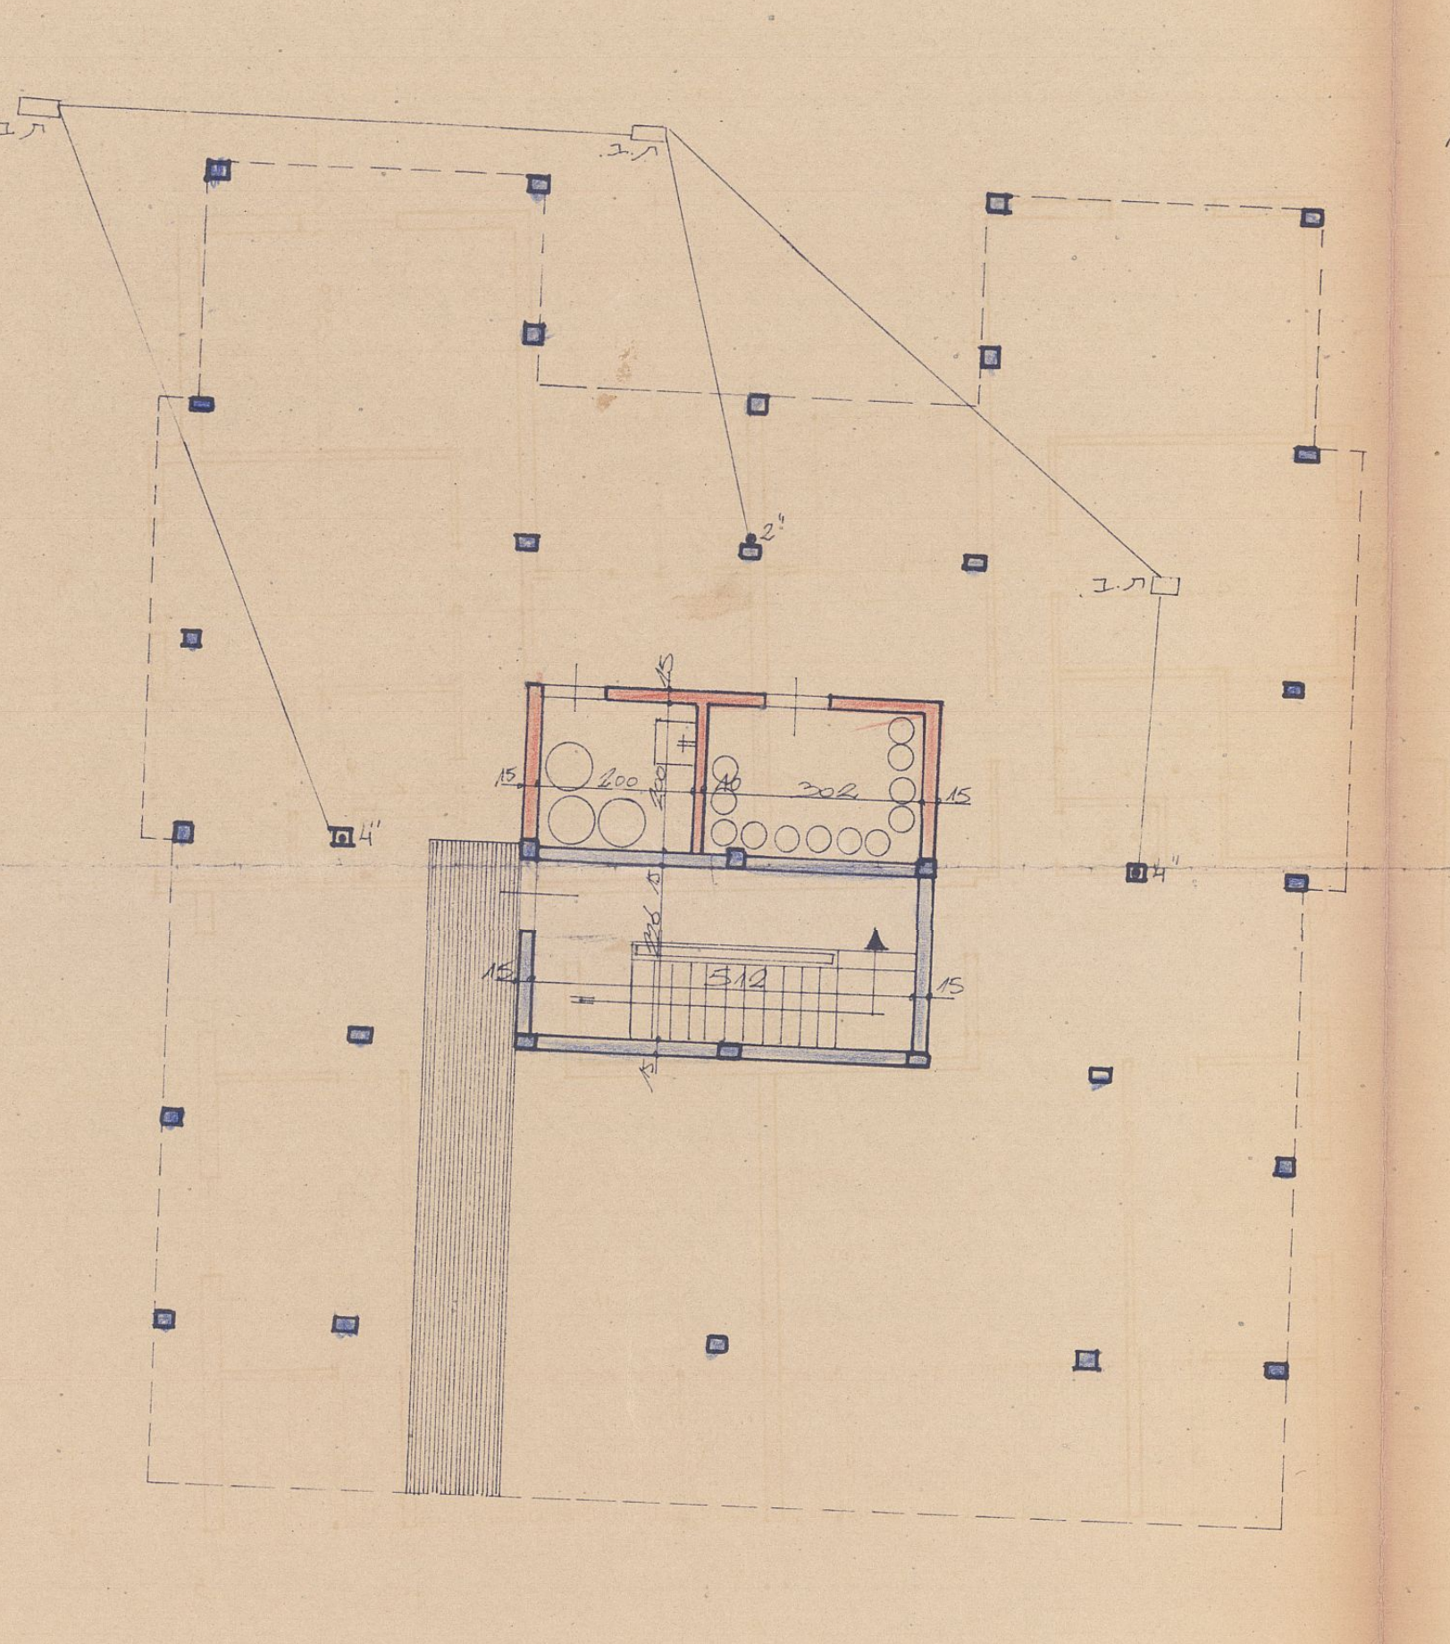

תכנית קומת עמודים
1:100

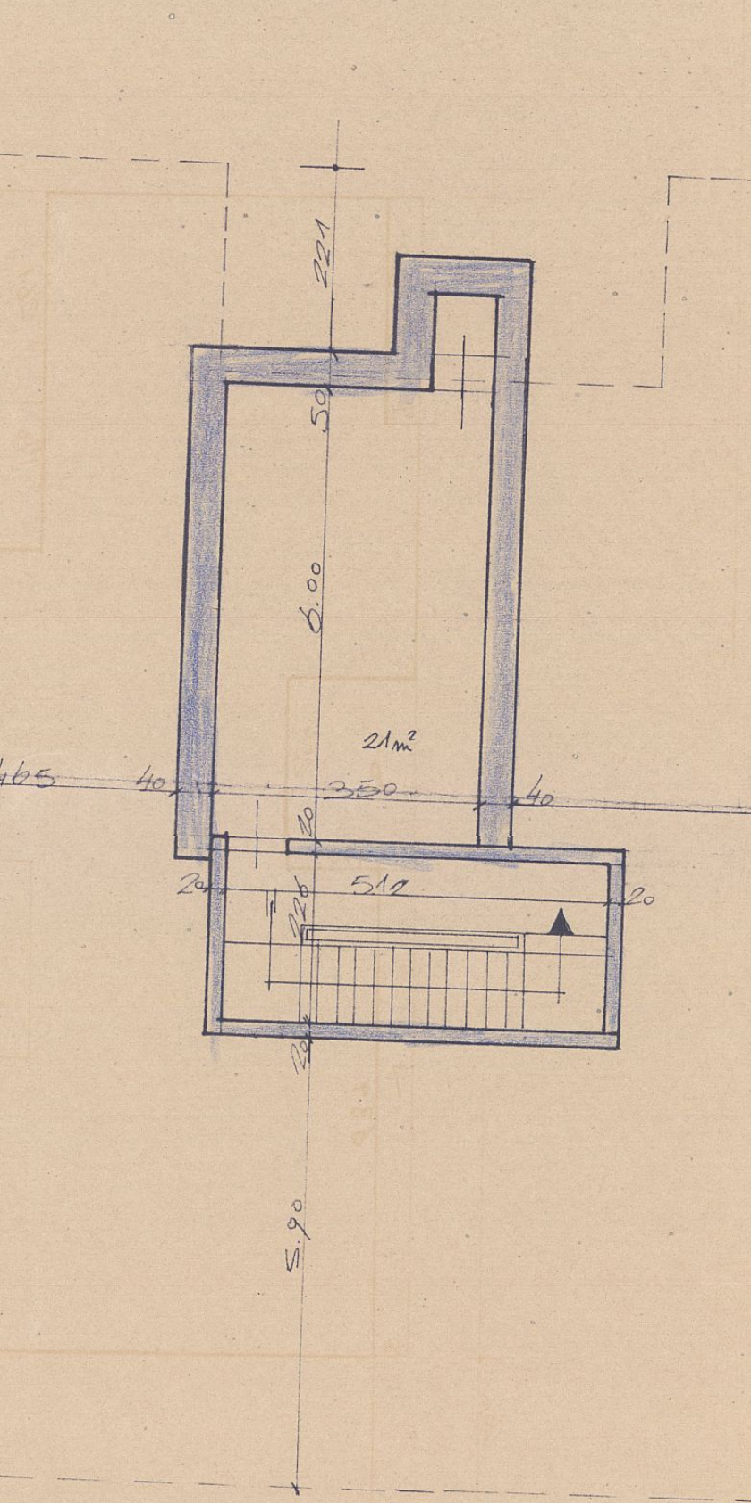

תכנית קומת המקלט
1:100

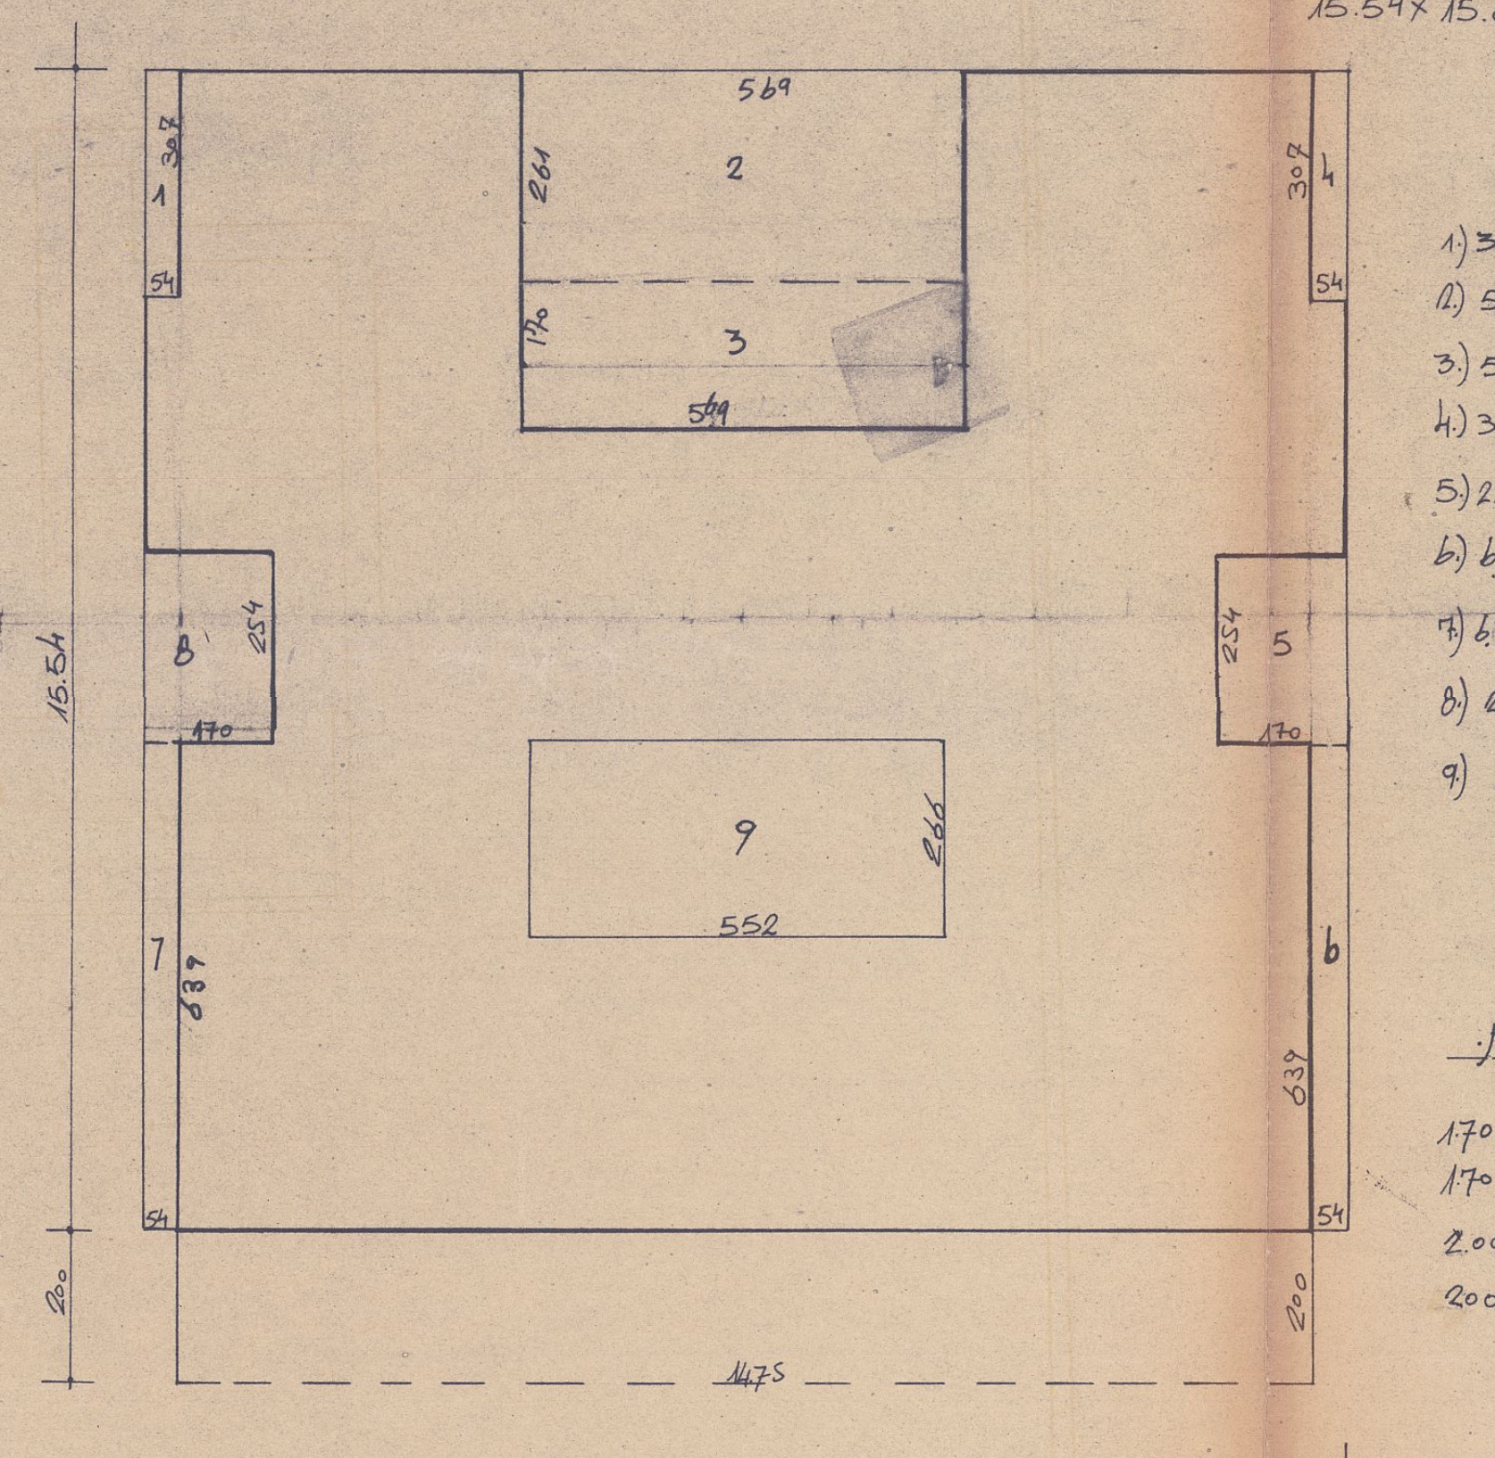

חישוב השטח
$15.54 \times 15.83 = 245.99 - 58.08 = 187.97\ m^2$

הורדות:
1) 3.07 × 0.54 = 1.65
2) 5.69 × 2.61 = 14.85
3) 5.69 × 1.70 = 9.67
4) 3.07 × 0.54 = 1.65
5) 2.54 × 1.70 = 4.31
6) 6.39 × 0.54 = 3.45
7) 6.39 × 0.54 = 3.45
8) 2.54 × 1.70 = 4.31
9) 5.52 × 2.66 = 14.68
58.08

חישוב המרפסות:
1.70 × 2.54 = 4.31
1.70 × 2.54 = 4.31
2.00 × 5.69 = 11.38
2.00 × 14.75 = 29.50
סה"כ: 49.50

בית ב׳ בית ג׳

תרשים המקום - 1:5,000

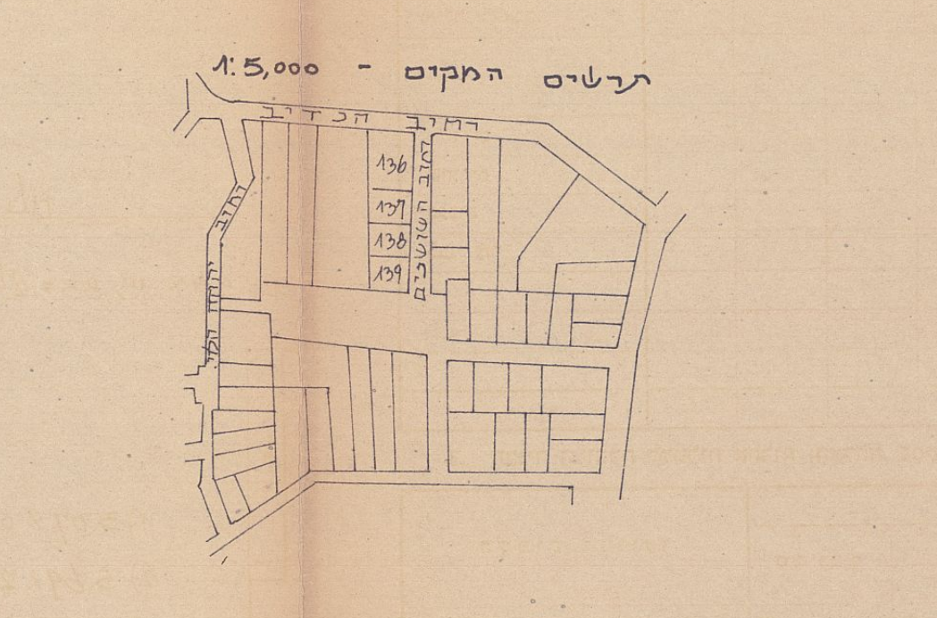

תרשים המגרש 1:250

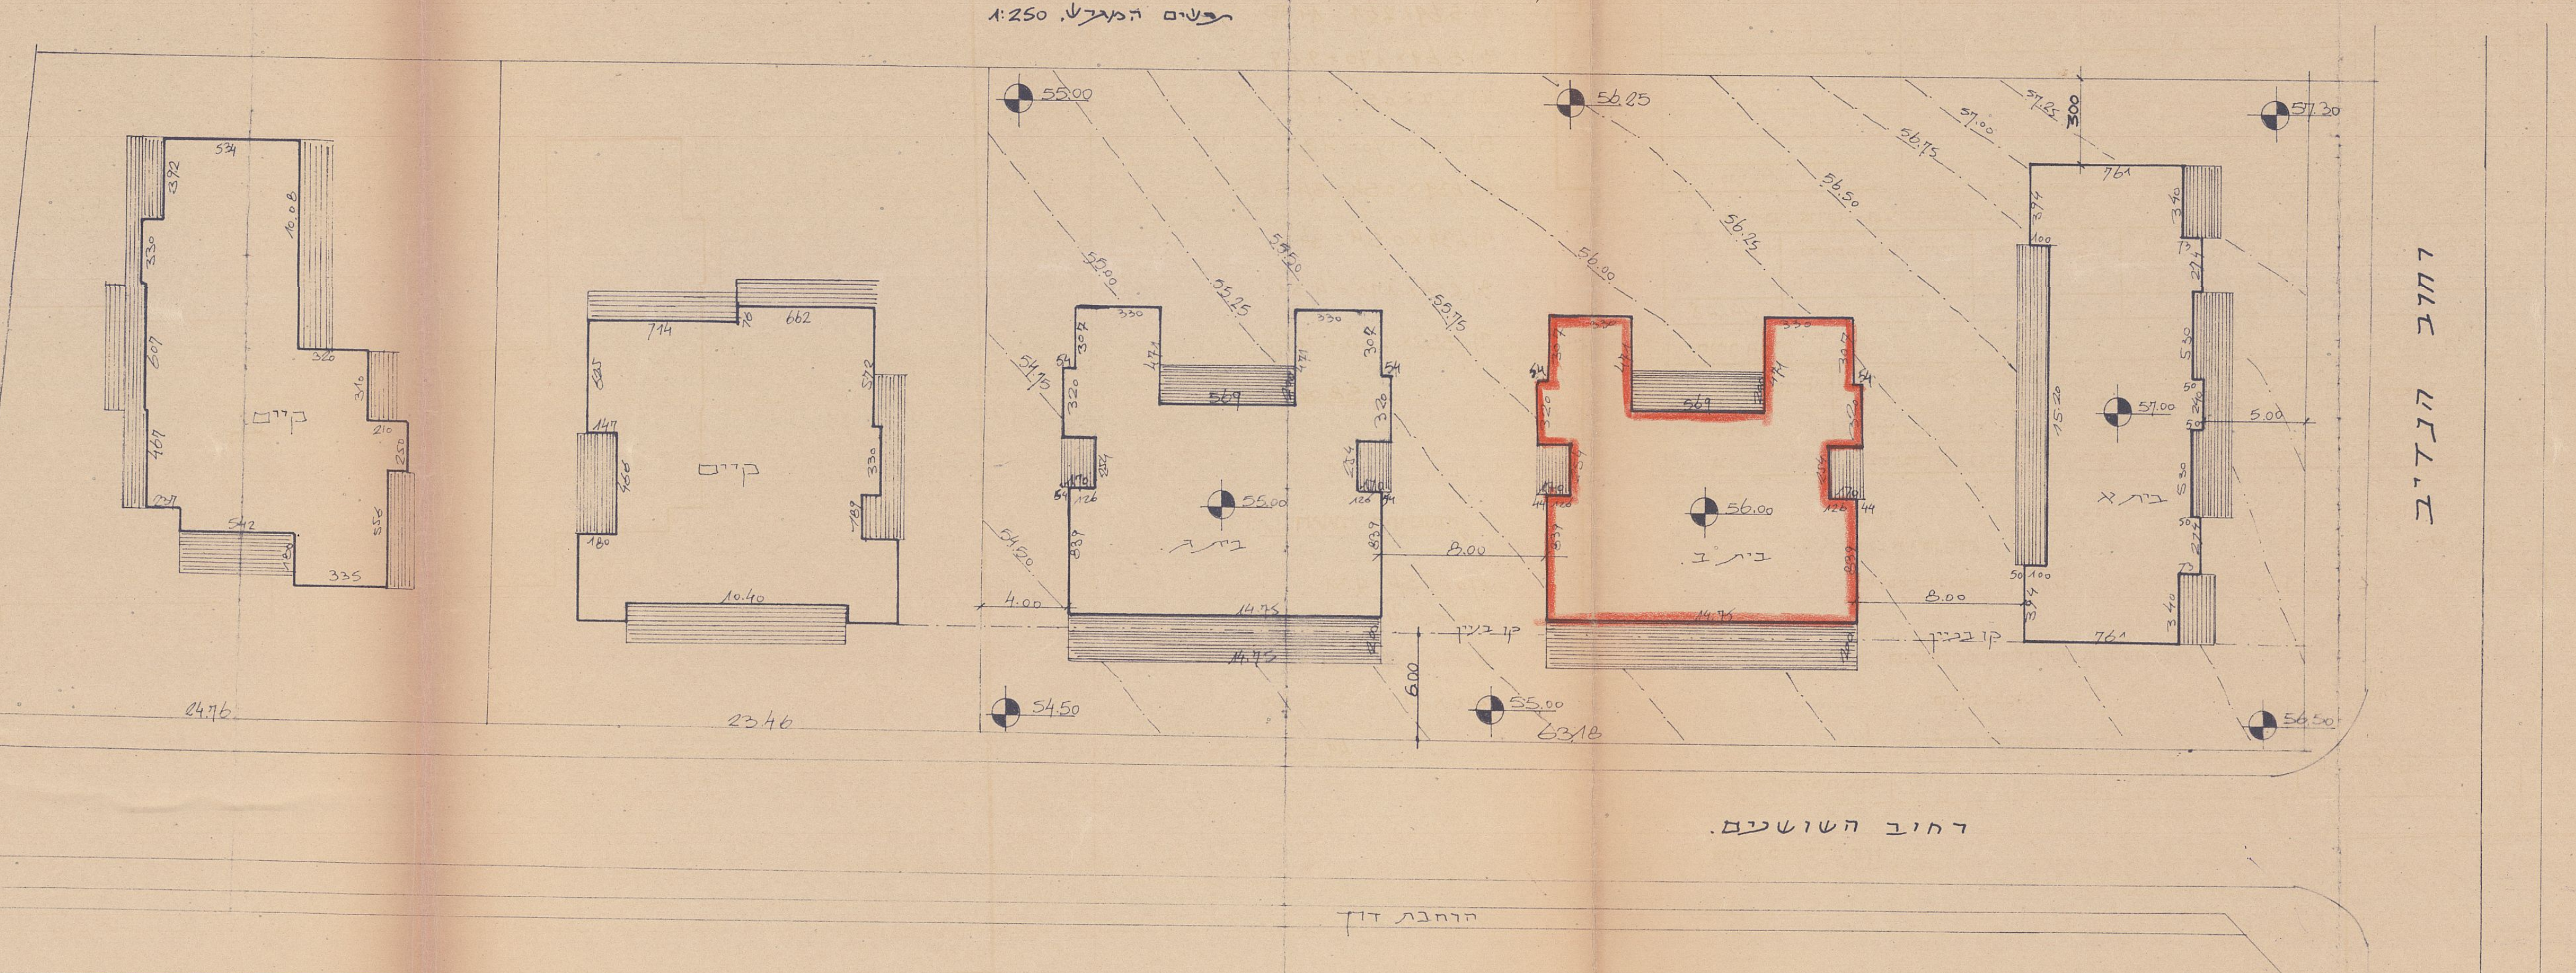

תיק מס׳

90

הוועדה המקומית לבניה ולתכנון עיר ....

נספח לבקשה להיתר בניה (מיפרט)

165/1661 ב

א. תאור הבנין

1. המקום	הרצליה	הרחוב	השושנים	מס׳	גוש 6529	חלקה 136/137
	השם		המען			מס׳ טלפון
2. המבקש	אחים שבתאי בע״מ		ר׳ העצמאות, הרצליה.			
3. בעל הנכס	״ ״		״ ״			
4. עורך התכנית	קורה בע״מ		ר׳ הרצל 29 רג.			736746
5. האחראי לביצוע העבודה						

6. אזור הבניה: ☒ מגורים ☐ מסחר ☐ תעשיה ☐ בנק צבורי ☐ חקלאי ☐ ....

7. שטח: המגרש / החלקה: 2,012 ממ״ר. אחוז הבניה המותר: ....%

8. מטרת הבנין: ☒ מגורים ☐ הארחה ☐ עסקים ☐ תעשיה ☐ חקלאי ☐ צבורי ☐ ....

9. מהות המבנה ותכליתו: בית משותף בן שלוש קומות על קומת עמודים.

10. תאור העבודה המוצעת: ☒ בנין חדש ☐ תוספת לבנין קיים ☐ הריסה ☐ תקונים ☐ שינוי במבנה ☐ ....
שינוי בשימוש ממטרה: .... למטרה: ....

11. האם הבניה היא עבור: ☐ משרד השיכון ☐ הסוכנות היהודית

ב. מבנה הבנין

קומה	קיים	מוצע	סך הכל	אחוז הבניה	מגורים בדירות: עד 45 ממ״ר	עד 65 ממ״ר	עד 90 ממ״ר	מעל 90 ממ״ר	עסק הארחה וכו׳: עד 20 ממ״ר	מעל 20 ממ״ב	צבורי	שונות	מס׳ חדרים: קיים	מוצע
.1	.2	.3	.4	.5	.6	.7	.8	.9	.10	.11	.12	.13	.14	.15
מרתף	מקלט	21.00	21.00									21.00		1
ק׳ קרקע תחתונה														
קרקע														
בינים														
א׳		187.97	187.97	9.3%				187.97						8
ב׳		187.97	187.97	9.3%				187.97						8
ג׳		187.97	187.97	9.3%				187.97						8
ד׳ מרפסות		148.50	148.50					148.50						
ה׳ חדר מדרגות		14.68	14.68									14.68		
ו׳														
מבני עזר														
סך הכל		748.09	748.09					712.41				35.68		25

הנפח המוצע לפי ההיתר: של המבנה העיקרי.......... ממ״ע. של מבנה העזר.......... ממ״ע.

ג. השימוש בבנין

1. הבנייה המוצעת למגורים

דירות בנות:	שטח כל דירה—ממ״ר	מס׳ דירות מכל סוג	כל הדירות	שטחים ממ״ר מזה: רצפות חדרי דיור בלבד, ומרפסות מקורות	רצפות שרותים ופרוזדורים ר׳ מרפסות מקורות	מרפסות בלתי מקורות	מספר חדרים: דיור	מטבחים	רחצה	ב״ש	אחרים
.1	.2	.3	.4	.5	.6	.7	.8	.9	.10	.11	.12
הדר אחד	ראה הרשום מודה של הדירות, בכל קומה, המציין מספר החדרים ושטח כל דירה.										
2 חדרים											
3 ״		6					24	6	6	6	
4 ״											
5 ״											
6 ״											
7 ״ ויותר											
חדרים נוספים לדירות קיימות											
מבני עזר											
סך הכל		6					24	6	6	6	

נפסק

מדף 4801/1

2. הבניה הקיימת והמוצעת לתעשיה ומלאכה

פרטים	קיים: שטח	גובה	נפח	% הבניה	מוצע: שטח	גובה	נפח	% הבניה	סך הכל: שטח	נפח	% הבניה	הערות
.1	.2	.3	.4	.5	.6	.7	.8	.9	.10	.11	.12	.13
אולמי מלאכה												
משרדים												
שרותים												
סככות												
מבני עזר												
סך הכל												

3. הבניה המוצעת למטרות אחרות (הארחה, עסקים ומשרדים, בניני צבור, מבני משק חקלאי, מטרות שונות)

השמוש המיועד	שטחים ממ״ר: ס״ה ממ״ר	מזה: הדרים	אולמות	אחסנה	שירותים	מספר חדרים ואולמות: הדרים	אולמות	אחסנה	שירותים
.1	.2	.3	.4	.5	.6	.7	.8	.9	.10
מבני עזר									

4. חלקי בנין אחרים — הבניה המוצעת, שטח בממ״ר

חדר מדרגות	מרפסות שלא נכללו בדירות	מעליות	חדרי הסקה	חדרי כביסה	מקלטים	קומת עמודים	מחסנים	מוסכים		סך הכל
.1	.2	.3	.4	.5	.6	.7	.8	.9	.10	.11
14.68					21.00					35.68

ד. חומר הבניה

קירות חיצוניים	☐ ביטון מזוין ☒ לבנין ביטון או בלוקים ☐ לבני סליקט ☐ לבנים שרופות ☐ אבן טבעית ☐ אבן מלאכותית ☐ איטונג ☐ עץ ☐ ברזל ☐ חמרים אחרים
תקרות	☒ ביטון מזוין ☐ עץ ☐ חומר אחר..........
גג:	☒ ביטון מזוין ☐ רעפים ☐ אסבסט ☐ פח ☐ חומר אחר..........

ה. גדרות
קיימות.......... מטר אורך מוצעות.......... מטר אורך

ו. מקרא
ביטון או ביטון מזויין: כחול
בלוקים או לבנים מביטון: אדום
אבן ☐ סיליקט או לבנים אדומות ☐ עץ ☐ חומר אחר ☐ איטונג ☐ להריסה ☐

הערות: ....
הנני מאשר כי הידיעות הנ״ל הן נכונות

תאריך.......... חתימת המבקש:.......... חתימת עורך התכנית: ....
חתימת בעל הנכס:..........

לשימוש הועדה המקומית בלבד	מס׳ ההיתר	תאריך ההיתר	תאריך התחלת בניה	תאריך גמר בניה

אשורים של רשויות חוץ:

הוועדה המקומית לבניה ולתכנון ערים
הרצליה
רשיון מס׳ 357 תאריך 9.12.70
נתאשר ע״י הועדה המקומית
בישיבתה מס׳ 42
בתאריך 5.4.70
מהנדס העיר .... יו״ר
מזכיר הועדה